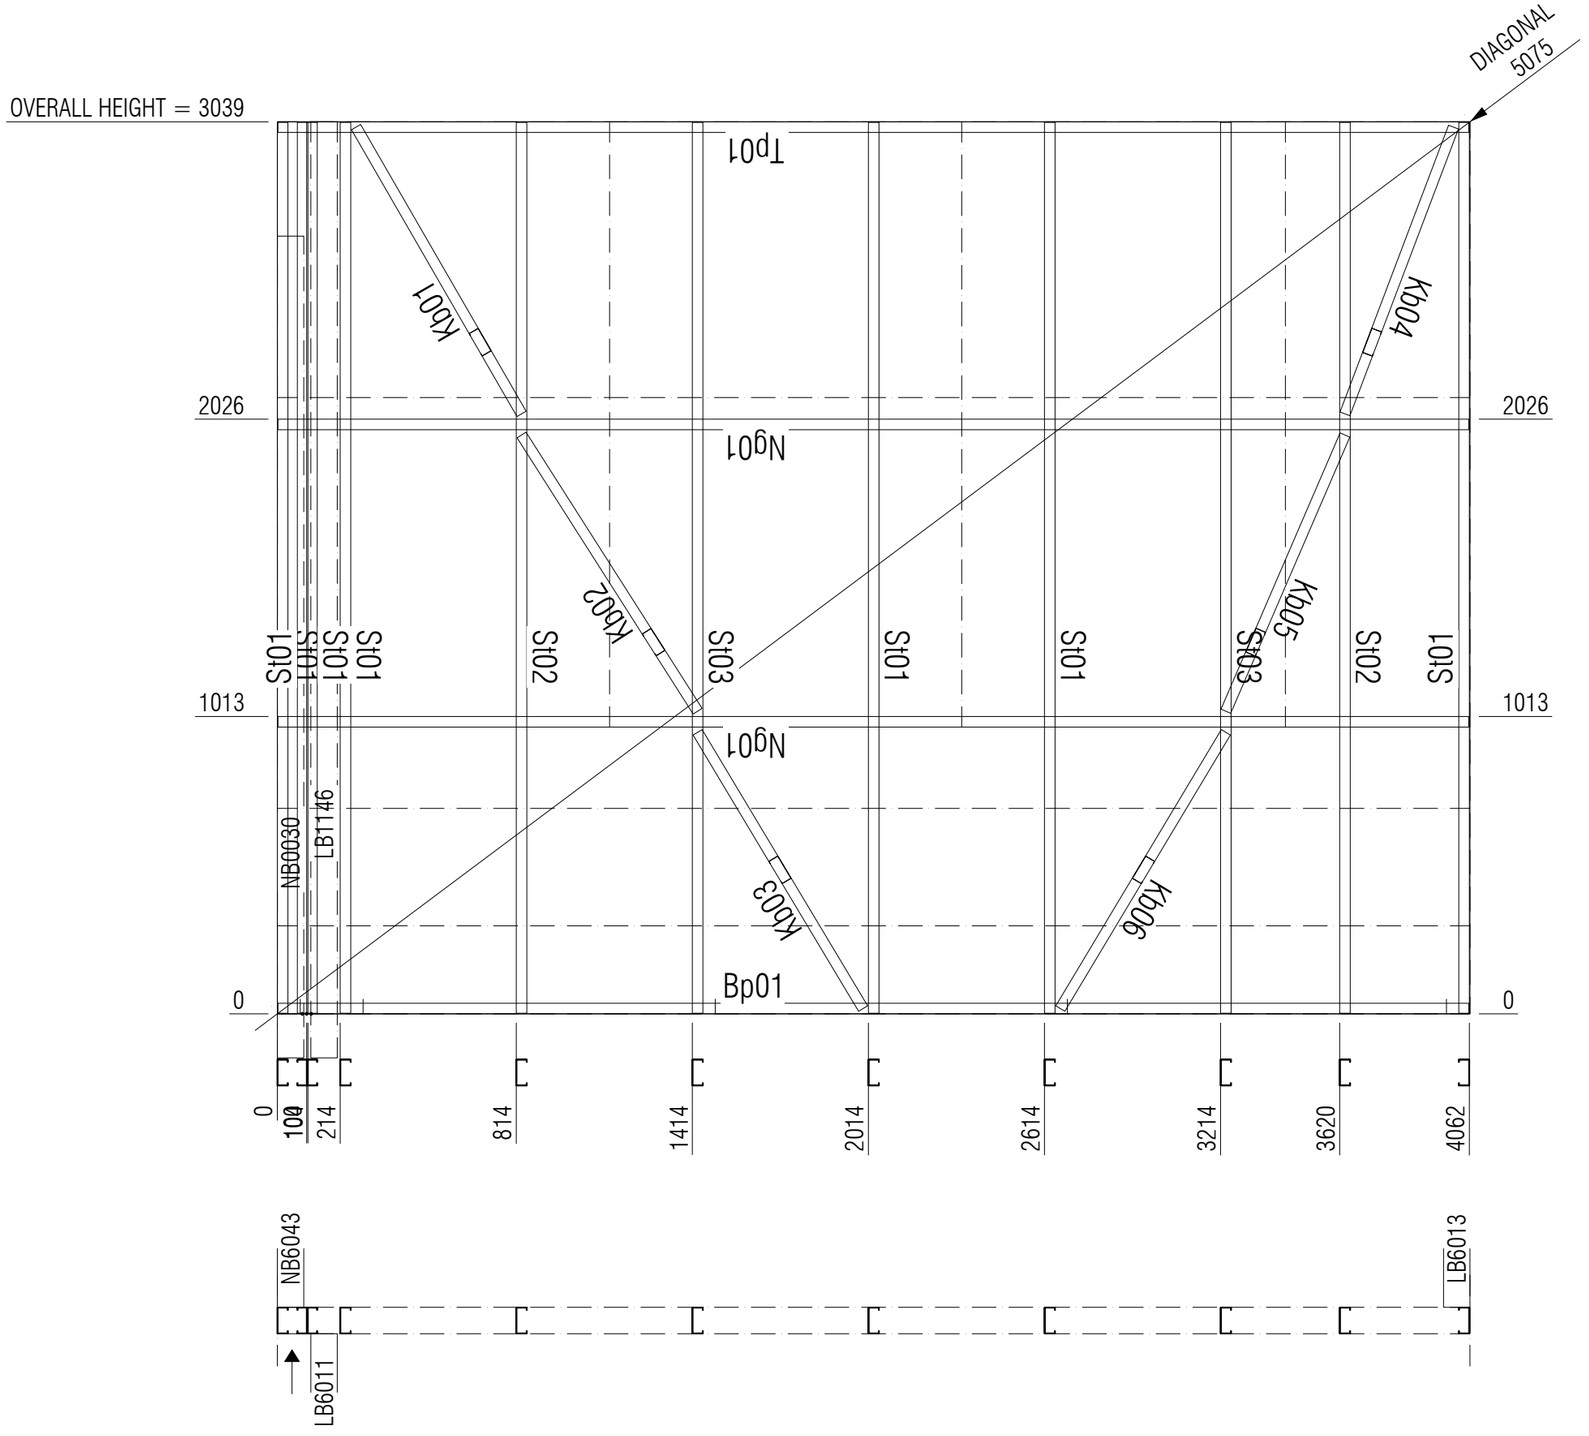


FRAME STICKS

NAME	LENGTH	WT	QTY	PROFILE
Tp01	4058	5.2	1	89S36-950-500
Bp01	4058	5.2	1	89S36-950-500
St01	3035	3.9	7	89S36-950-500
St02	3035	3.9	2	89S36-950-500
St03	3035	3.9	2	89S36-950-500
Ng01	4058	5.2	2	89S36-950-500
Kb01	1128	1.4	1	89S36-950-500
Kb02	1116	1.4	1	89S36-950-500
Kb03	1097	1.4	1	89S36-950-500
Kb04	1045	1.3	1	89S36-950-500
Kb05	1025	1.3	1	89S36-950-500
Kb06	1097	1.4	1	89S36-950-500
TOTAL	56131	71.8	21	


LB6012

AUSTRUSS
www.austruss.com.au (02) 4860 1400
DWG FILE: ####

DRAWN Mitchell.H
Ph:02 4860 1426

ISSUE	DATE	DESCRIPTION OF REVISION
0	05/03/26	IFA
A	03/05/26	IFC
B	06/05/26	IFC
C	08/05/26	IFC
D	11/05/26	IFC

Client/Company Name: Taylor
Project Name: Blayney
Project Address: 3 Osman st, Blayney NSW 2799
NOTE: USE PROVIDED DIMENSIONS ONLY. IF NOT PROVIDED, ASK.
Scale: NTS
Building / Zone / Area: Zone 6
Job Number: 23314
Drawing Name: 90mm LB Wall production
Drawing Number: LGS-6-201
Revision: D

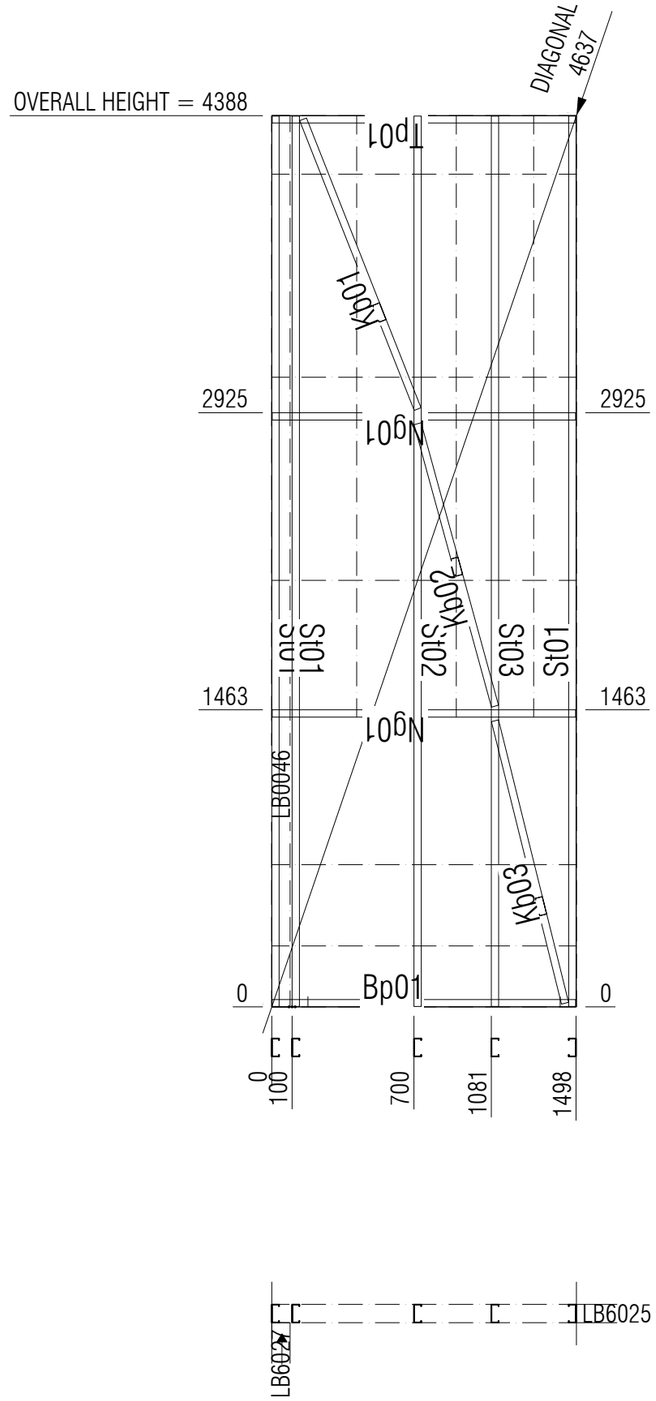

FRAME STICKS

NAME	LENGTH	WT	QTY	PROFILE
Tp01	1494	1.9	1	89S36-950-500
Bp01	1494	1.9	1	89S36-950-500
St01	4384	5.6	3	89S36-950-500
St02	4384	5.6	1	89S36-950-500
St03	4384	5.6	1	89S36-950-500
Ng01	1494	1.9	2	89S36-950-500
Kb01	1534	2.0	1	89S36-950-500
Kb02	1442	1.8	1	89S36-950-500
Kb03	1433	1.8	1	89S36-950-500
TOTAL	32305	41.3	12	


LB6026

AUSTRUSS
www.austruss.com.au (02) 4860 1400
DWG FILE: ####

DRAWN Mitchell.H
Ph:02 4860 1426

ISSUE	DATE	DESCRIPTION OF REVISION
0	05/03/26	IFA
A	03/05/26	IFC
B	06/05/26	IFC
C	08/05/26	IFC
D	11/05/26	IFC

Client/Company Name: Taylor
Project Name: Blayney
Building / Zone / Area: Zone 6
Job Number: 23314
Project Address: 3 Osman st, Blayney NSW 2799
Drawing Name: 90mm LB Wall production
Drawing Number: LGS-6-201
Revision: D
NOTE: USE PROVIDED DIMENSIONS ONLY. IF NOT PROVIDED, ASK.
Scale: NTS

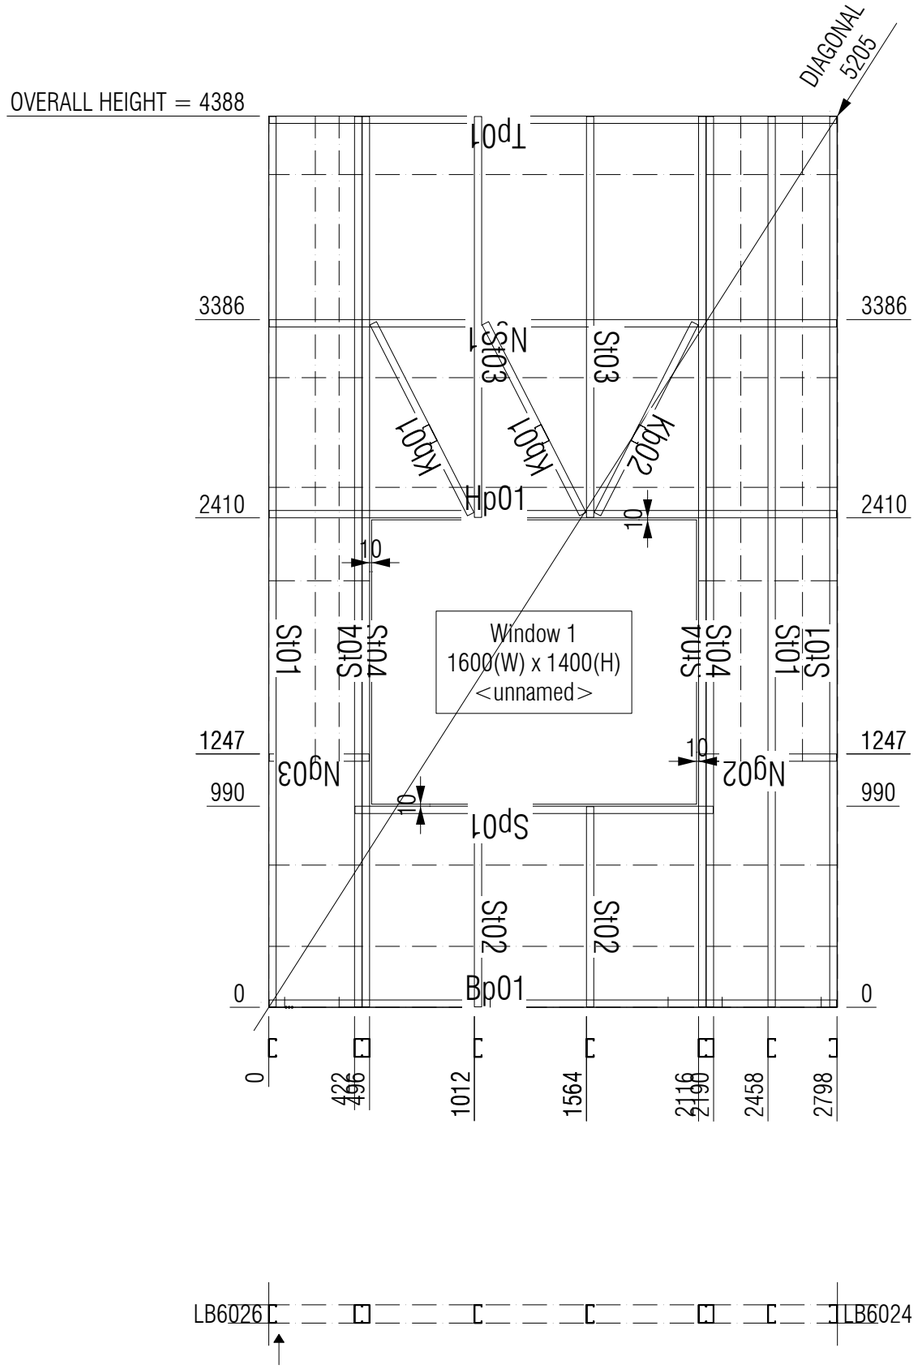

FRAME STICKS

NAME	LENGTH	WT	QTY	PROFILE
Tp01	2794	3.6	1	89S36-950-500
Bp01	2794	3.6	1	89S36-950-500
St01	4384	5.6	3	89S36-950-500
St02	986	1.3	2	89S36-950-500
St03	1974	2.5	2	89S36-950-500
St04	4384	5.6	4	89S36-950-500
Ng01	2794	3.6	1	89S36-950-500
Ng02	678	0.9	1	89S36-950-500
Ng03	492	0.6	1	89S36-950-500
Kb01	1055	1.4	2	89S36-950-500
Kb02	1055	1.4	1	89S36-950-500
Hp01	2794	3.6	1	89S36-950-500
Sp01	1764	2.3	1	89S36-950-500
TOTAL	53883	69.0	21	

LB6025

AUSTRUSS
www.austruss.com.au (02) 4860 1400

DRAWN Mitchell.H Ph:02 4860 1426

DWG FILE: ####

ISSUE	DATE	DESCRIPTION OF REVISION
0	05/03/26	IFA
A	03/05/26	IFC
B	06/05/26	IFC
C	08/05/26	IFC
D	11/05/26	IFC

Client/Company Name: Taylor

Project Name: Blayney

Project Address: 3 Osman st, Blayney NSW 2799

NOTE: USE PROVIDED DIMENSIONS ONLY. IF NOT PROVIDED, ASK.

Scale: NTS


Building / Zone / Area: Zone 6

Drawing Name: 90mm LB Wall production

Job Number: 23314

Drawing Number: LGS-6-201

Revision: D

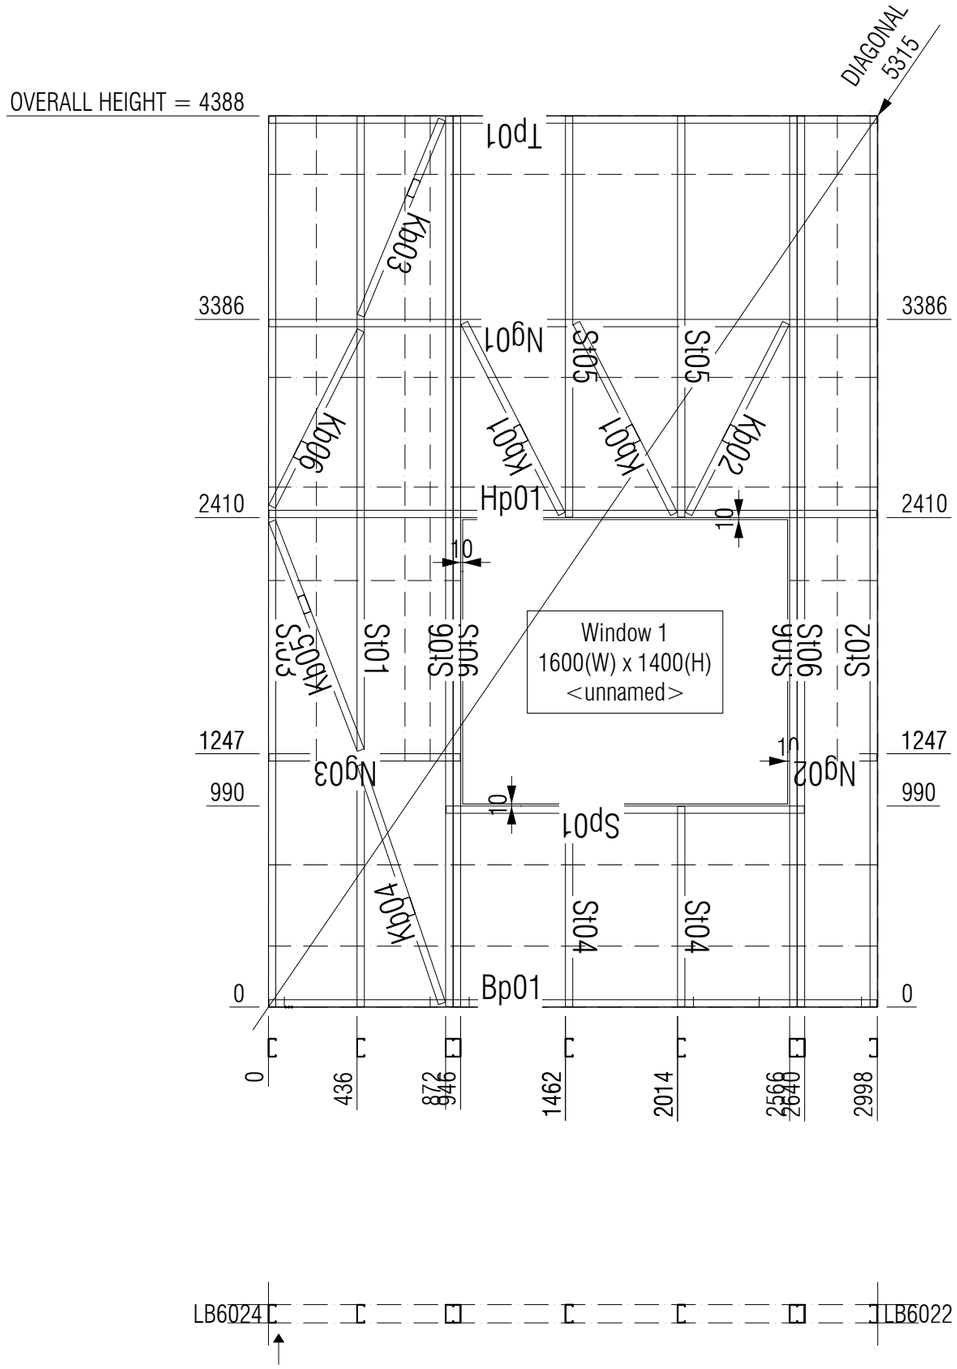

FRAME STICKS

NAME	LENGTH	WT	QTY	PROFILE
Tp01	2994	3.8	1	89S36-950-500
Bp01	2994	3.8	1	89S36-950-500
St01	4384	5.6	1	89S36-950-500
St02	4384	5.6	1	89S36-950-500
St03	4384	5.6	1	89S36-950-500
St04	986	1.3	2	89S36-950-500
St05	1974	2.5	2	89S36-950-500
St06	4384	5.6	4	89S36-950-500
Ng01	2994	3.8	1	89S36-950-500
Ng02	428	0.5	1	89S36-950-500
Ng03	942	1.2	1	89S36-950-500
Kb01	1055	1.4	2	89S36-950-500
Kb02	1055	1.4	1	89S36-950-500
Kb03	1046	1.3	1	89S36-950-500
Kb04	1242	1.6	1	89S36-950-500
Kb05	1208	1.5	1	89S36-950-500
Kb06	971	1.2	1	89S36-950-500
Hp01	2994	3.8	1	89S36-950-500
Sp01	1764	2.3	1	89S36-950-500
TOTAL	59350	76.0	25	

LB6023


AUSTRUSS
www.austruss.com.au (02) 4860 1400

DWG FILE: ####

DRAWN Mitchell.H
Ph:02 4860 1426

ISSUE	DATE	DESCRIPTION OF REVISION
0	05/03/26	IFA
A	03/05/26	IFC
B	06/05/26	IFC
C	08/05/26	IFC
D	11/05/26	IFC

Client/Company Name: Taylor
Project Name: Blayney
Building / Zone / Area: Zone 6
Job Number: 23314
Project Address: 3 Osman st, Blayney NSW 2799
Drawing Name: 90mm LB Wall production
Drawing Number: LGS-6-201
Revision: D
NOTE: USE PROVIDED DIMENSIONS ONLY. IF NOT PROVIDED, ASK.
Scale: NTS

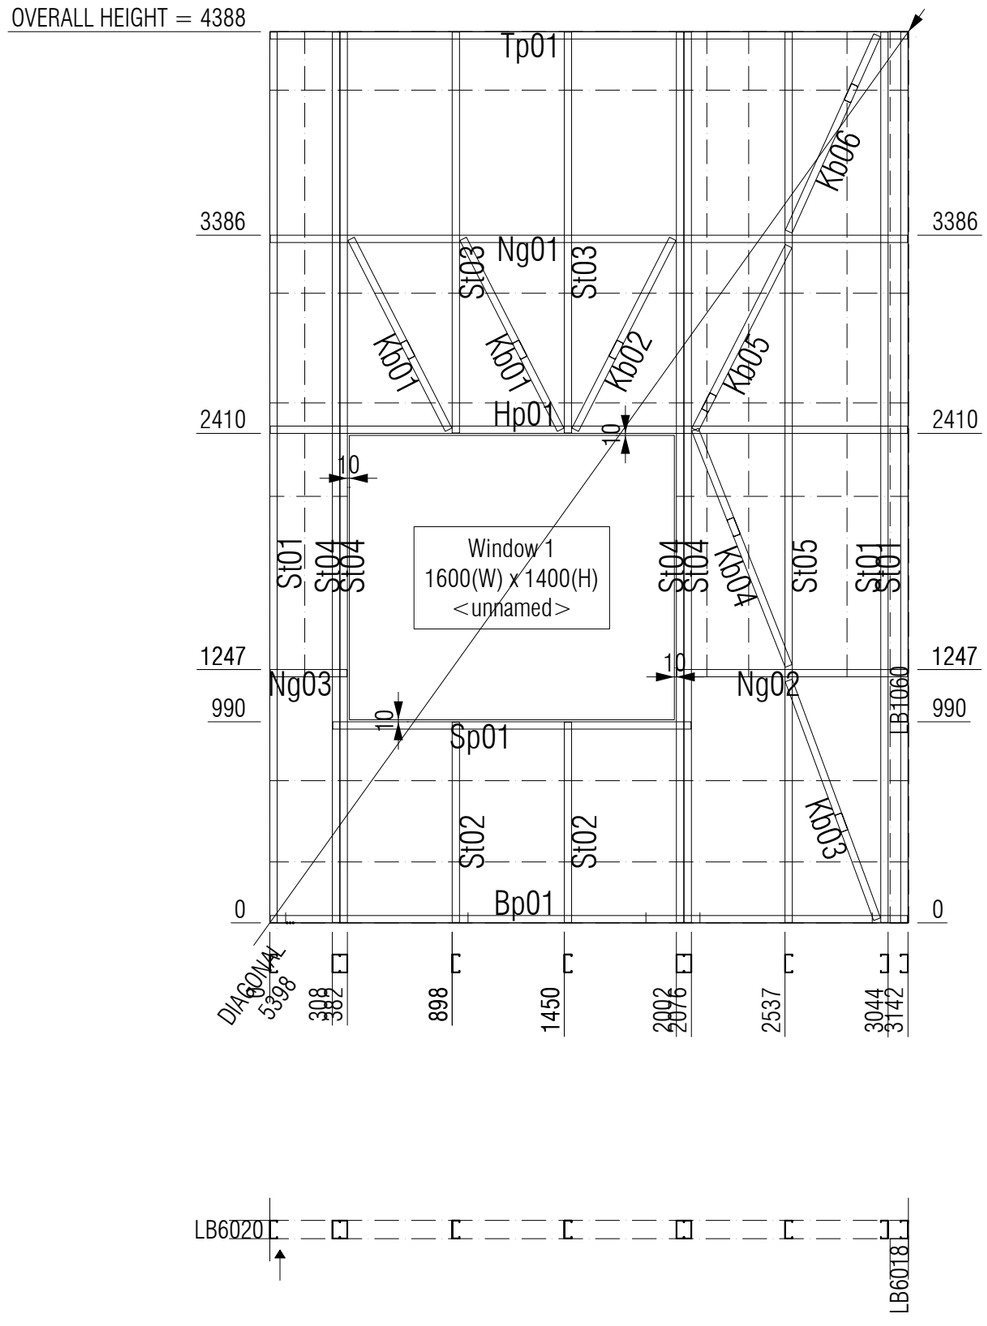

FRAME STICKS

NAME	LENGTH	WT	QTY	PROFILE
Tp01	3138	4.0	1	89S36-950-500
Bp01	3138	4.0	1	89S36-950-500
St01	4384	5.6	3	89S36-950-500
St02	986	1.3	2	89S36-950-500
St03	1974	2.5	2	89S36-950-500
St04	4384	5.6	4	89S36-950-500
St05	4384	5.6	1	89S36-950-500
Ng01	3138	4.0	1	89S36-950-500
Ng02	1136	1.5	1	89S36-950-500
Ng03	378	0.5	1	89S36-950-500
Kb01	1055	1.4	2	89S36-950-500
Kb02	1055	1.4	1	89S36-950-500
Kb03	1253	1.6	1	89S36-950-500
Kb04	1251	1.6	1	89S36-950-500
Kb05	1015	1.3	1	89S36-950-500
Kb06	1060	1.4	1	89S36-950-500
Hp01	3138	4.0	1	89S36-950-500
Sp01	1764	2.3	1	89S36-950-500
TOTAL	64568	82.6	26	


LB6019

AUSTRUSS
www.austruss.com.au (02) 4860 1400
DWG FILE: ####

DRAWN Mitchell.H
Ph:02 4860 1426

ISSUE	DATE	DESCRIPTION OF REVISION
0	05/03/26	IFA
A	03/05/26	IFC
B	06/05/26	IFC
C	08/05/26	IFC
D	11/05/26	IFC

Client/Company Name: Taylor
Project Name: Blayney
Project Address: 3 Osman st, Blayney NSW 2799
NOTE: USE PROVIDED DIMENSIONS ONLY. IF NOT PROVIDED, ASK.
Scale: NTS
Building / Zone / Area: Zone 6
Job Number: 23314
Drawing Name: 90mm LB Wall production
Drawing Number: LGS-6-201
Revision: D

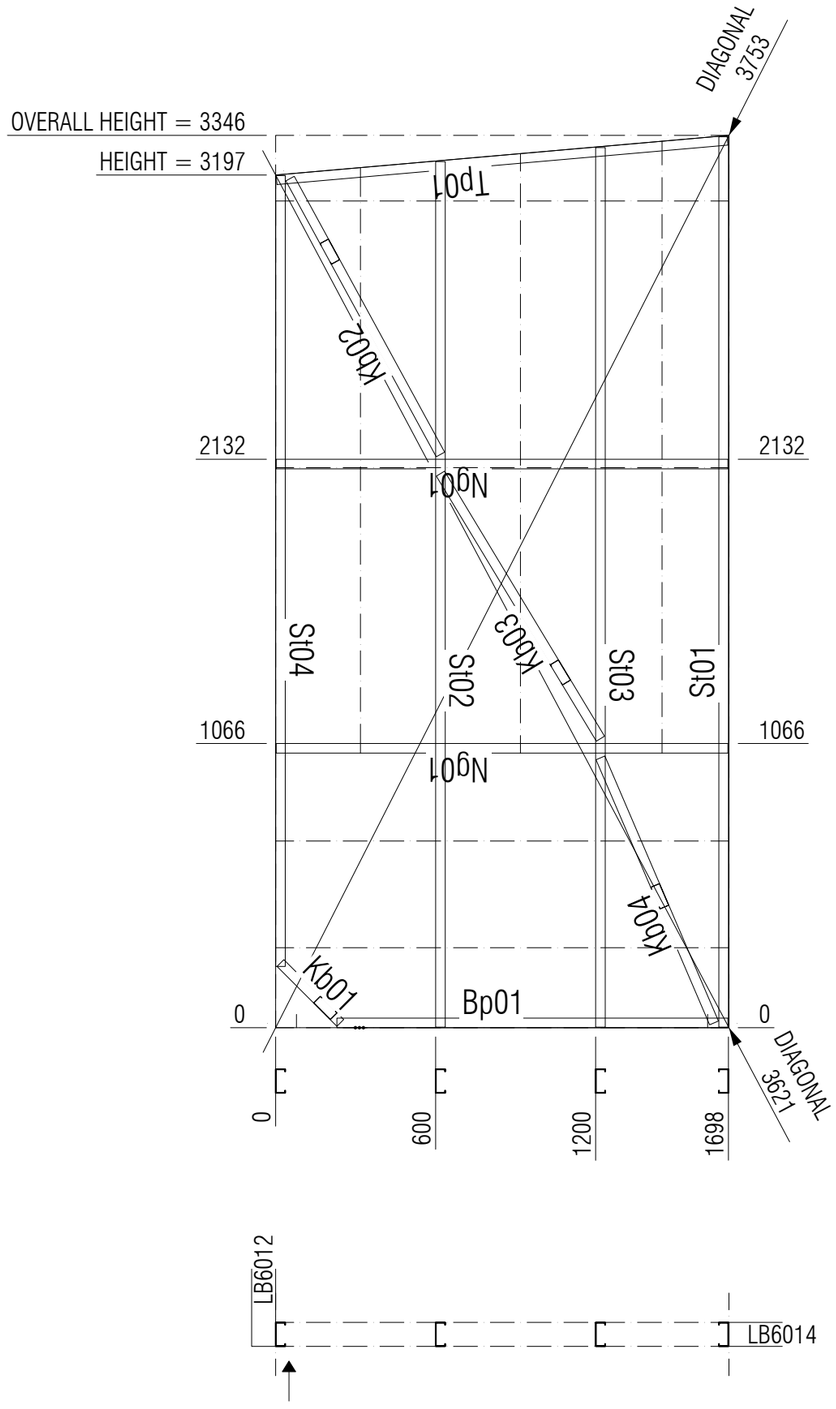

FRAME STICKS

NAME	LENGTH	WT	QTY	PROFILE
Tp01	1697	2.2	1	89S36-950-500
Bp01	1466	1.9	1	89S36-950-500
St01	3339	4.3	1	89S36-950-500
St02	3246	4.2	1	89S36-950-500
St03	3298	4.2	1	89S36-950-500
St04	2966	3.8	1	89S36-950-500
Ng01	1694	2.2	2	89S36-950-500
Kb01	317	0.4	1	89S36-950-500
Kb02	1178	1.5	1	89S36-950-500
Kb03	1161	1.5	1	89S36-950-500
Kb04	1081	1.4	1	89S36-950-500
TOTAL	23138	29.6	12	

LB6013


AUSTRUSS
www.austruss.com.au (02) 4860 1400

DWG FILE: ####

DRAWN
Mitchell.H
Ph:02 4860 1426

ISSUE	DATE	DESCRIPTION OF REVISION
0	05/03/26	IFA
A	03/05/26	IFC
B	06/05/26	IFC
C	08/05/26	IFC
D	11/05/26	IFC

Client/Company Name: Taylor
Project Name: Blayney
Building / Zone / Area: Zone 6
Job Number: 23314
Project Address: 3 Osman st, Blayney NSW 2799
NOTE: USE PROVIDED DIMENSIONS ONLY. IF NOT PROVIDED, ASK.
Scale: NTS
Drawing Name: 90mm LB Wall production
Drawing Number: LGS-6-201
Revision: D

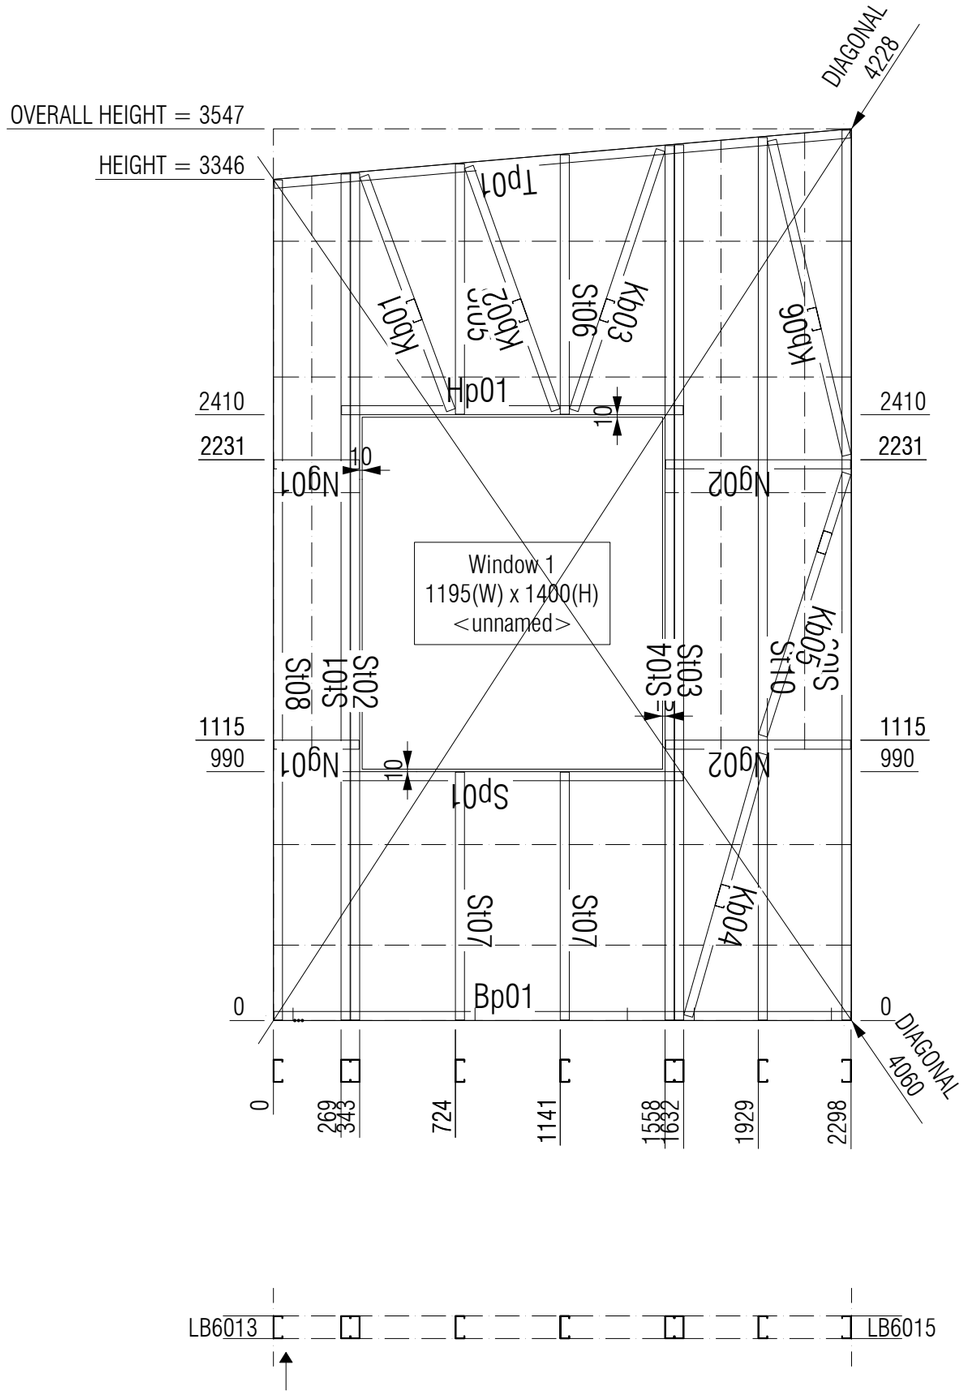

FRAME STICKS

NAME	LENGTH	WT	QTY	PROFILE
Tp01	2300	2.9	1	89S36-950-500
Bp01	2294	2.9	1	89S36-950-500
St01	3369	4.3	1	89S36-950-500
St02	3366	4.3	1	89S36-950-500
St03	3478	4.5	1	89S36-950-500
St04	3482	4.5	1	89S36-950-500
St05	995	1.3	1	89S36-950-500
St06	1032	1.3	1	89S36-950-500
St07	986	1.3	2	89S36-950-500
St08	3342	4.3	1	89S36-950-500
St09	3540	4.5	1	89S36-950-500
St10	3511	4.5	1	89S36-950-500
Ng01	339	0.4	2	89S36-950-500
Ng02	736	0.9	2	89S36-950-500
Kb01	993	1.3	1	89S36-950-500
Kb02	1028	1.3	1	89S36-950-500
Kb03	1091	1.4	1	89S36-950-500
Kb04	1085	1.4	1	89S36-950-500
Kb05	1095	1.4	1	89S36-950-500
Kb06	1288	1.6	1	89S36-950-500
Hp01	1359	1.7	1	89S36-950-500
Sp01	1359	1.7	1	89S36-950-500
TOTAL	44128	56.5	25	

LB6014

AUSTRUSS
www.austruss.com.au (02) 4860 1400


DWG FILE: ####

DRAWN Mitchell.H
Ph:02 4860 1426

ISSUE	DATE	DESCRIPTION OF REVISION
0	05/03/26	IFA
A	03/05/26	IFC
B	06/05/26	IFC
C	08/05/26	IFC
D	11/05/26	IFC

Client/Company Name: Taylor
Project Name: Blayney
Project Address: 3 Osman st, Blayney NSW 2799
NOTE: USE PROVIDED DIMENSIONS ONLY. IF NOT PROVIDED, ASK.
Scale: NTS
Building / Zone / Area: Zone 6
Job Number: 23314
Drawing Name: 90mm LB Wall production
Drawing Number: LGS-6-201
Revision: D

DOUBLE SCREW

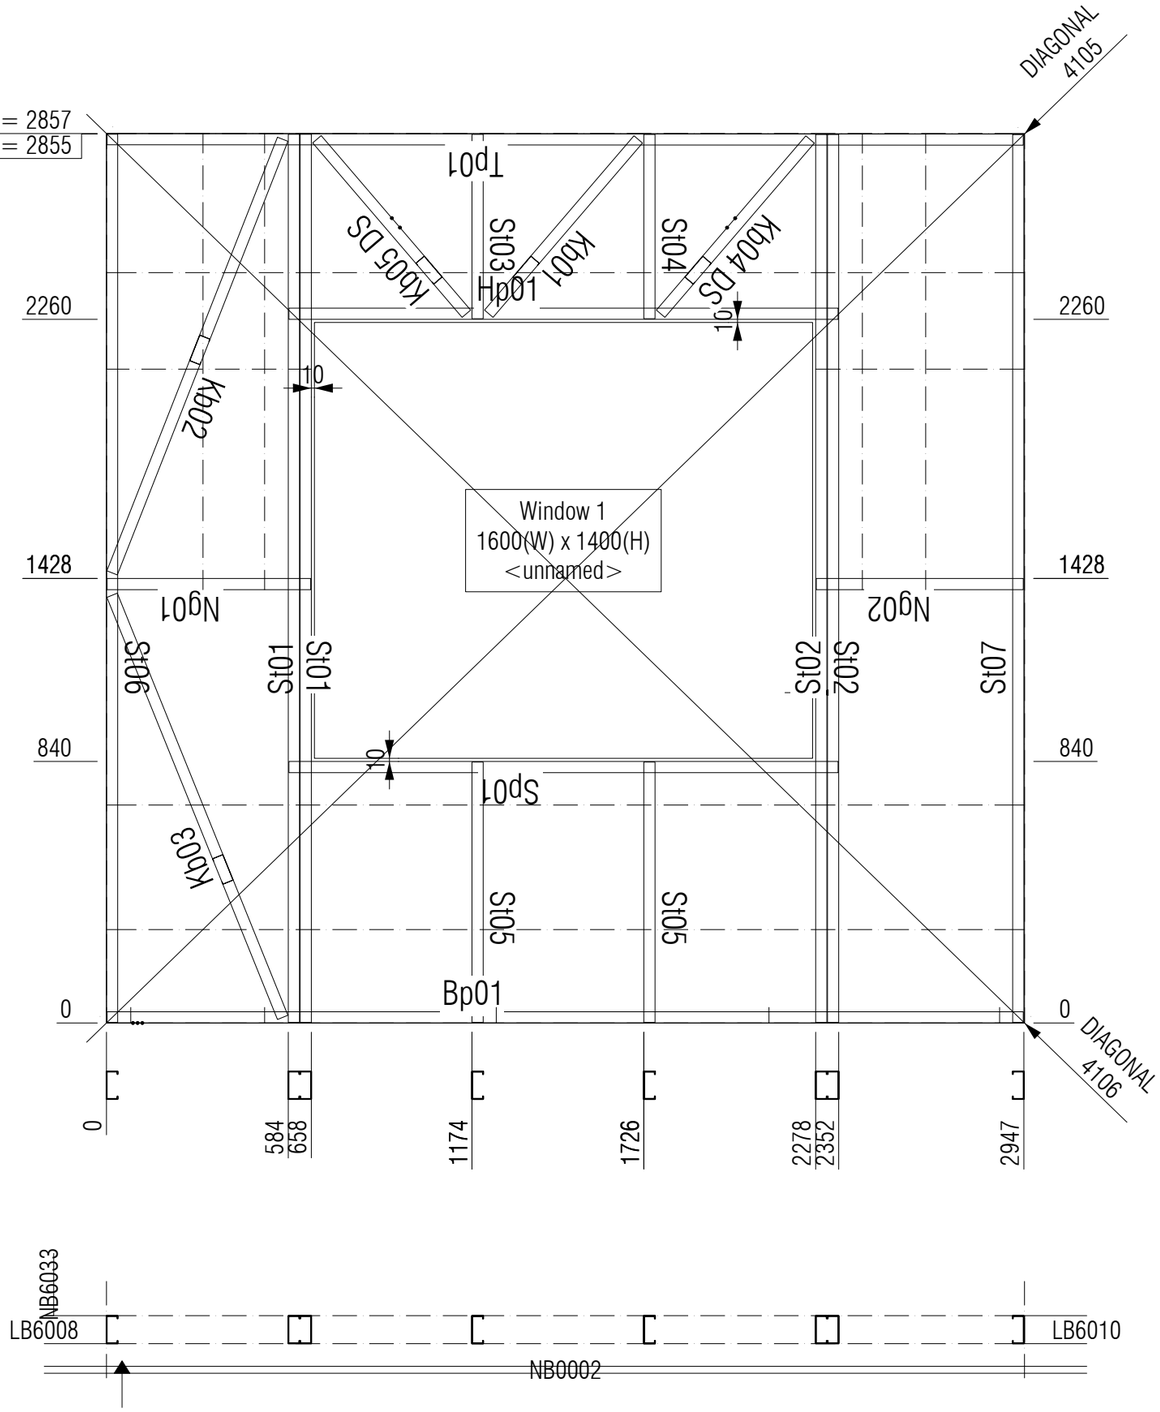

FRAME STICKS

NAME	LENGTH	WT	QTY	PROFILE
Tp01	2943	3.8	1	89S36-950-500
Bp01	2943	3.8	1	89S36-950-500
St01	2852	3.7	2	89S36-950-500
St02	2852	3.7	2	89S36-950-500
St03	592	0.8	1	89S36-950-500
St04	592	0.8	1	89S36-950-500
St05	836	1.1	2	89S36-950-500
St06	2853	3.7	1	89S36-950-500
St07	2851	3.6	1	89S36-950-500
Ng01	654	0.8	1	89S36-950-500
Ng02	665	0.9	1	89S36-950-500
Kb01	738	0.9	1	89S36-950-500
Kb02	1497	1.9	1	89S36-950-500
Kb03	1462	1.9	1	89S36-950-500
Kb04 DS	737	0.9	1	89S36-950-500
Kb05 DS	738	0.9	1	89S36-950-500
Hp01	1764	2.3	1	89S36-950-500
Sp01	1764	2.3	1	89S36-950-500
TOTAL	35872	45.9	21	

LB6009

AUSTRUSS
www.austruss.com.au (02) 4860 1400


DWG FILE: ####

DRAWN Mitchell.H
Ph:02 4860 1426

ISSUE	DATE	DESCRIPTION OF REVISION
0	05/03/26	IFA
A	03/05/26	IFC
B	06/05/26	IFC
C	08/05/26	IFC
D	11/05/26	IFC

Client/Company Name: Taylor
Project Name: Blayney
Building / Zone / Area: Zone 6
Job Number: 23314
Project Address: 3 Osman st, Blayney NSW 2799
Drawing Name: 90mm LB Wall production
Drawing Number: LGS-6-201
Revision: D
NOTE: USE PROVIDED DIMENSIONS ONLY. IF NOT PROVIDED, ASK.
Scale: NTS

DOUBLE SCREW

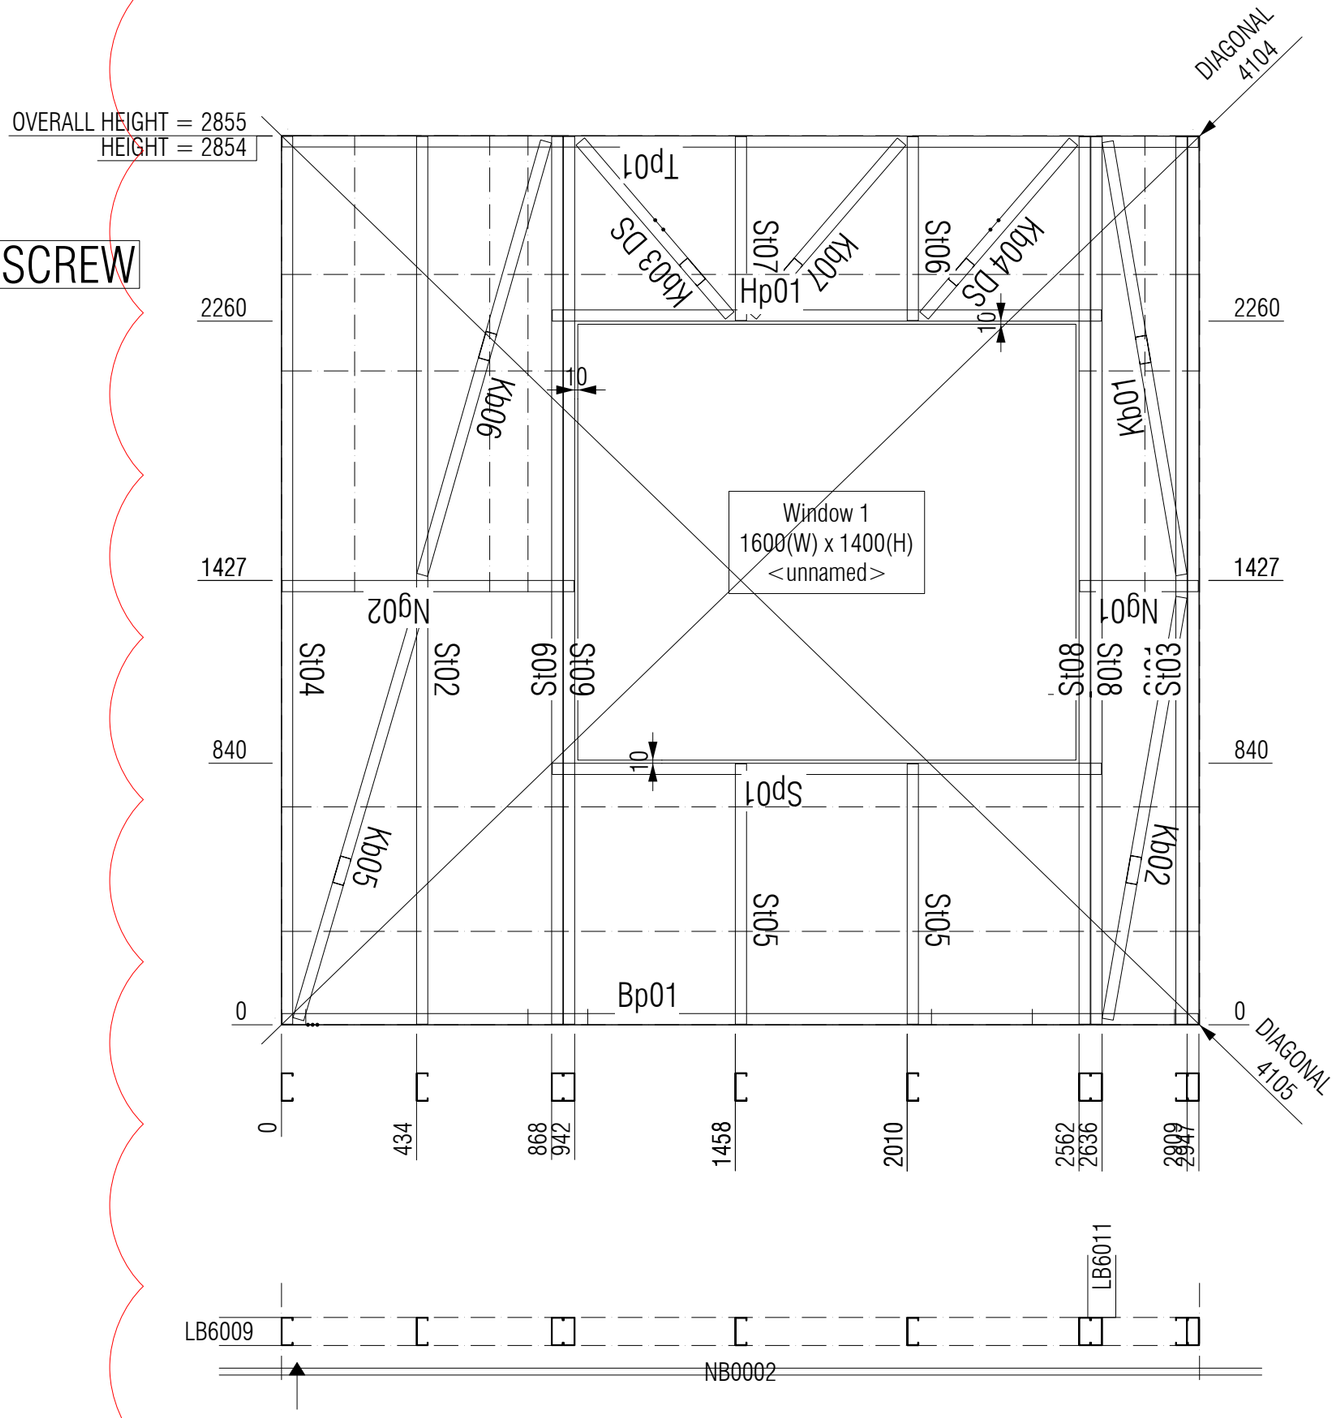

FRAME STICKS

NAME	LENGTH	WT	QTY	PROFILE
Tp01	2943	3.8	1	89S36-950-500
Bp01	2943	3.8	1	89S36-950-500
St01	2850	3.6	1	89S36-950-500
St02	2851	3.6	1	89S36-950-500
St03	2850	3.6	1	89S36-950-500
St04	2851	3.6	1	89S36-950-500
St05	836	1.1	2	89S36-950-500
St06	591	0.8	1	89S36-950-500
St07	591	0.8	1	89S36-950-500
St08	2850	3.6	2	89S36-950-500
St09	2851	3.6	2	89S36-950-500
Ng01	381	0.5	1	89S36-950-500
Ng02	938	1.2	1	89S36-950-500
Kb01	1411	1.8	1	89S36-950-500
Kb02	1376	1.8	1	89S36-950-500
Kb03 DS	737	0.9	1	89S36-950-500
Kb04 DS	736	0.9	1	89S36-950-500
Kb05	1412	1.8	1	89S36-950-500
Kb06	1448	1.9	1	89S36-950-500
Kb07	736	0.9	1	89S36-950-500
Hp01	1764	2.3	1	89S36-950-500
Sp01	1764	2.3	1	89S36-950-500
TOTAL	44247	56.6	25	

LB6010


AUSTRUSS
www.austruss.com.au (02) 4860 1400

DRAWN Mitchell.H
Ph:02 4860 1426

DWG FILE: ####

ISSUE	DATE	DESCRIPTION OF REVISION
0	05/03/26	IFA
A	03/05/26	IFC
B	06/05/26	IFC
C	08/05/26	IFC
D	11/05/26	IFC

Client/Company Name: Taylor
Project Name: Blayney
Building / Zone / Area: Zone 6
Job Number: 23314
Project Address: 3 Osman st, Blayney NSW 2799
Drawing Name: 90mm LB Wall production
Drawing Number: LGS-6-201
Revision: D
NOTE: USE PROVIDED DIMENSIONS ONLY. IF NOT PROVIDED, ASK.
Scale: NTS

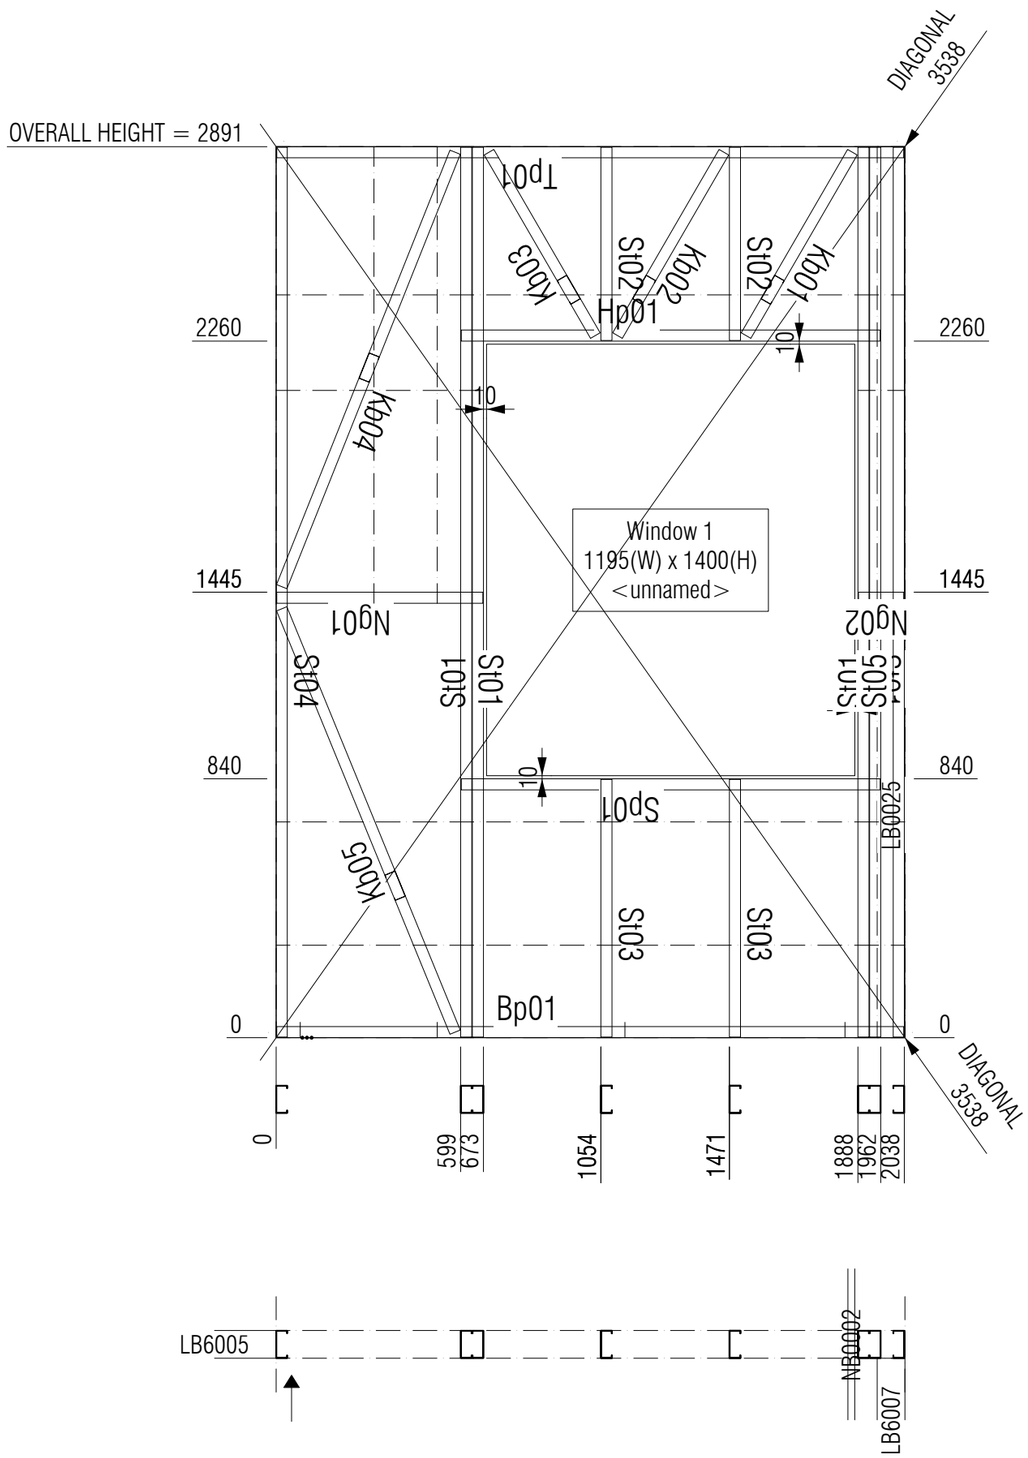

FRAME STICKS

NAME	LENGTH	WT	QTY	PROFILE
Tp01	2034	2.6	1	89S36-950-500
Bp01	2034	2.6	1	89S36-950-500
St01	2887	3.7	4	89S36-950-500
St02	627	0.8	2	89S36-950-500
St03	836	1.1	2	89S36-950-500
St04	2887	3.7	1	89S36-950-500
St05	2887	3.7	1	89S36-950-500
Ng01	669	0.9	1	89S36-950-500
Ng02	147	0.2	1	89S36-950-500
Kb01	688	0.9	1	89S36-950-500
Kb02	688	0.9	1	89S36-950-500
Kb03	688	0.9	1	89S36-950-500
Kb04	1518	1.9	1	89S36-950-500
Kb05	1484	1.9	1	89S36-950-500
Hp01	1359	1.7	1	89S36-950-500
Sp01	1359	1.7	1	89S36-950-500
TOTAL	32913	42.1	21	

LB6006


AUSTRUSS
www.austruss.com.au (02) 4860 1400

DRAWN Mitchell.H Ph:02 4860 1426

DWG FILE: ####

ISSUE	DATE	DESCRIPTION OF REVISION
0	05/03/26	IFA
A	03/05/26	IFC
B	06/05/26	IFC
C	08/05/26	IFC
D	11/05/26	IFC

Client/Company Name: Taylor
Project Name: Blayney
Building / Zone / Area: Zone 6
Job Number: 23314
Project Address: 3 Osman st, Blayney NSW 2799
Drawing Name: 90mm LB Wall production
Drawing Number: LGS-6-201
Revision: D
NOTE: USE PROVIDED DIMENSIONS ONLY. IF NOT PROVIDED, ASK.
Scale: NTS

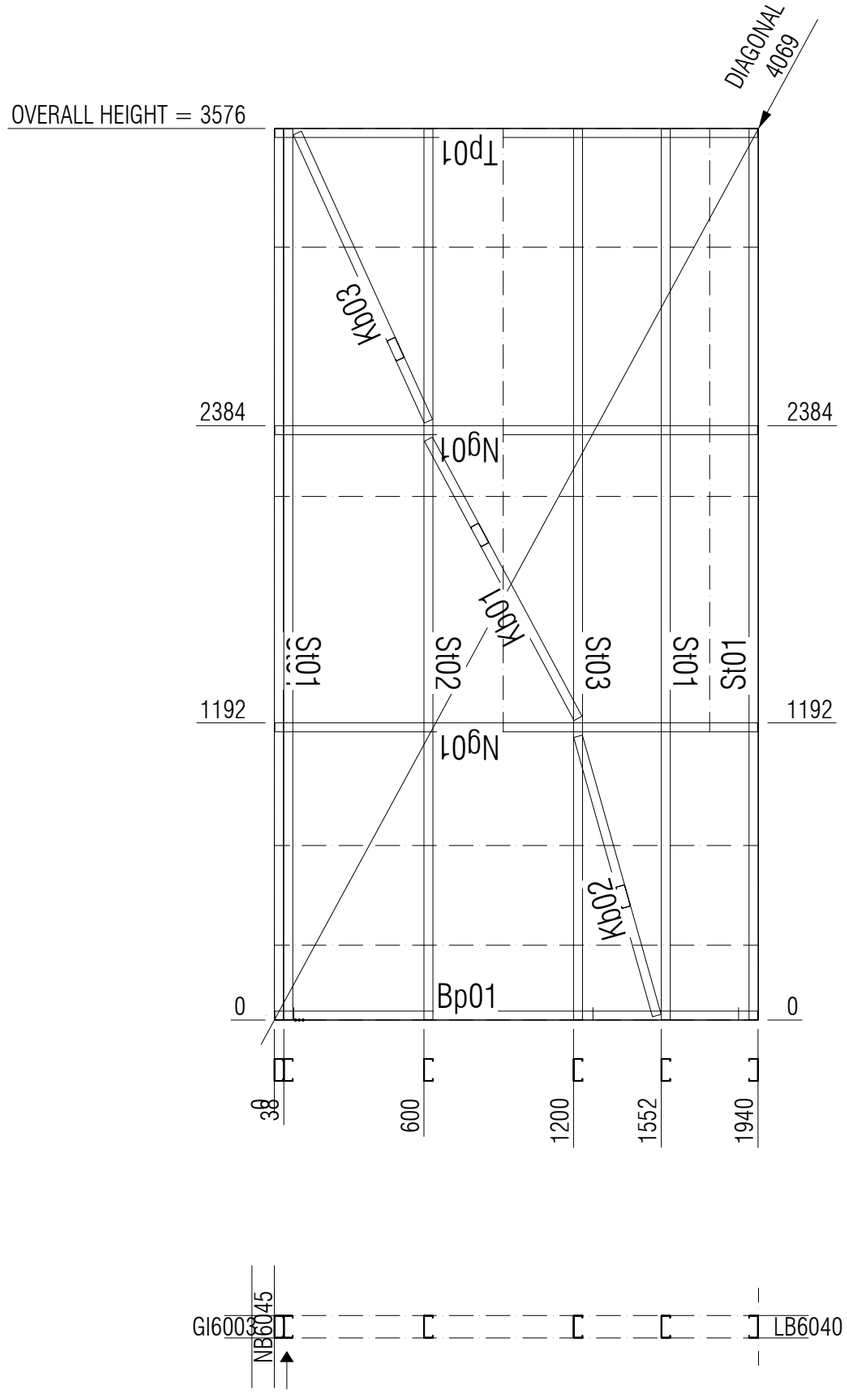

FRAME STICKS

NAME	LENGTH	WT	QTY	PROFILE
Tp01	1936	2.5	1	89S36-950-500
Bp01	1936	2.5	1	89S36-950-500
St01	3572	4.6	4	89S36-950-500
St02	3572	4.6	1	89S36-950-500
St03	3572	4.6	1	89S36-950-500
Ng01	1936	2.5	2	89S36-950-500
Kb01	1271	1.6	1	89S36-950-500
Kb02	1164	1.5	1	89S36-950-500
Kb03	1270	1.6	1	89S36-950-500
TOTAL	32879	42.1	13	

LB6039


AUSTRUSS
www.austruss.com.au (02) 4860 1400

DWG FILE: ####

DRAWN
Mitchell.H
Ph:02 4860 1426

ISSUE	DATE	DESCRIPTION OF REVISION
0	05/03/26	IFA
A	03/05/26	IFC
B	06/05/26	IFC
C	08/05/26	IFC
D	11/05/26	IFC

Client/Company Name: Taylor
Project Name: Blayney
Building / Zone / Area: Zone 6
Job Number: 23314
Project Address: 3 Osman st, Blayney NSW 2799
Drawing Name: 90mm LB Wall production
Drawing Number: LGS-6-201
Revision: D
NOTE: USE PROVIDED DIMENSIONS ONLY. IF NOT PROVIDED, ASK.
Scale: NTS

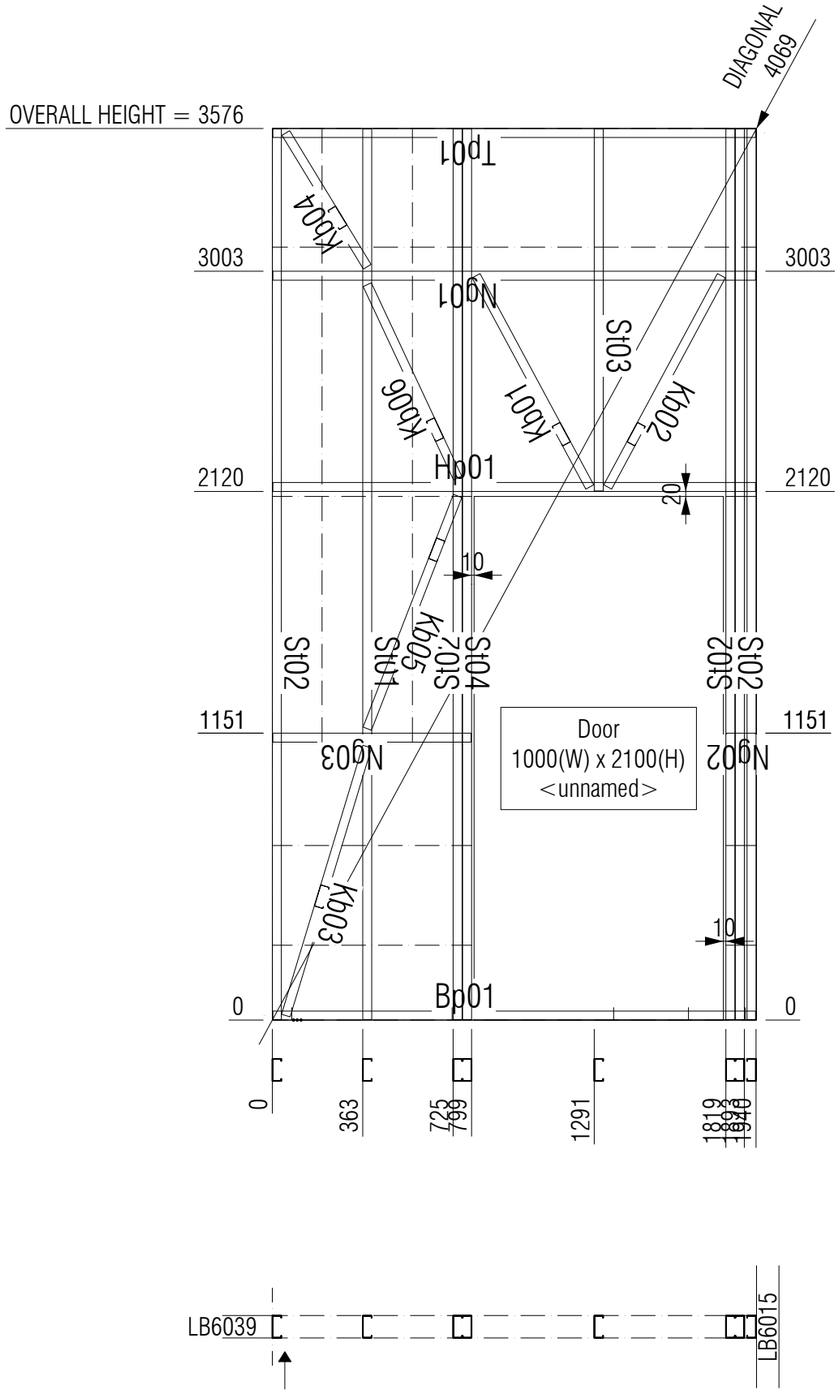

FRAME STICKS

NAME	LENGTH	WT	QTY	PROFILE
Tp01	1936	2.5	1	89S36-950-500
Bp01	1936	2.5	1	89S36-950-500
St01	3572	4.6	1	89S36-950-500
St02	3572	4.6	5	89S36-950-500
St03	1452	1.9	1	89S36-950-500
St04	3572	4.6	1	89S36-950-500
Ng01	1936	2.5	1	89S36-950-500
Ng02	117	0.1	1	89S36-950-500
Ng03	795	1.0	1	89S36-950-500
Kb01	962	1.2	1	89S36-950-500
Kb02	962	1.2	1	89S36-950-500
Kb03	1127	1.4	1	89S36-950-500
Kb04	628	0.8	1	89S36-950-500
Kb05	1001	1.3	1	89S36-950-500
Kb06	856	1.1	1	89S36-950-500
Hp01	1936	2.5	1	89S36-950-500
TOTAL	40647	52.0	20	

LB6040


AUSTRUSS
www.austruss.com.au (02) 4860 1400

DWG FILE: ####

DRAWN
Mitchell.H
Ph:02 4860 1426

ISSUE	DATE	DESCRIPTION OF REVISION
0	05/03/26	IFA
A	03/05/26	IFC
B	06/05/26	IFC
C	08/05/26	IFC
D	11/05/26	IFC

Client/Company Name: Taylor
Project Name: Blayney
Building / Zone / Area: Zone 6
Job Number: 23314
Project Address: 3 Osman st, Blayney NSW 2799
Drawing Name: 90mm LB Wall production
Drawing Number: LGS-6-201
Revision: D
NOTE: USE PROVIDED DIMENSIONS ONLY. IF NOT PROVIDED, ASK.
Scale: NTS

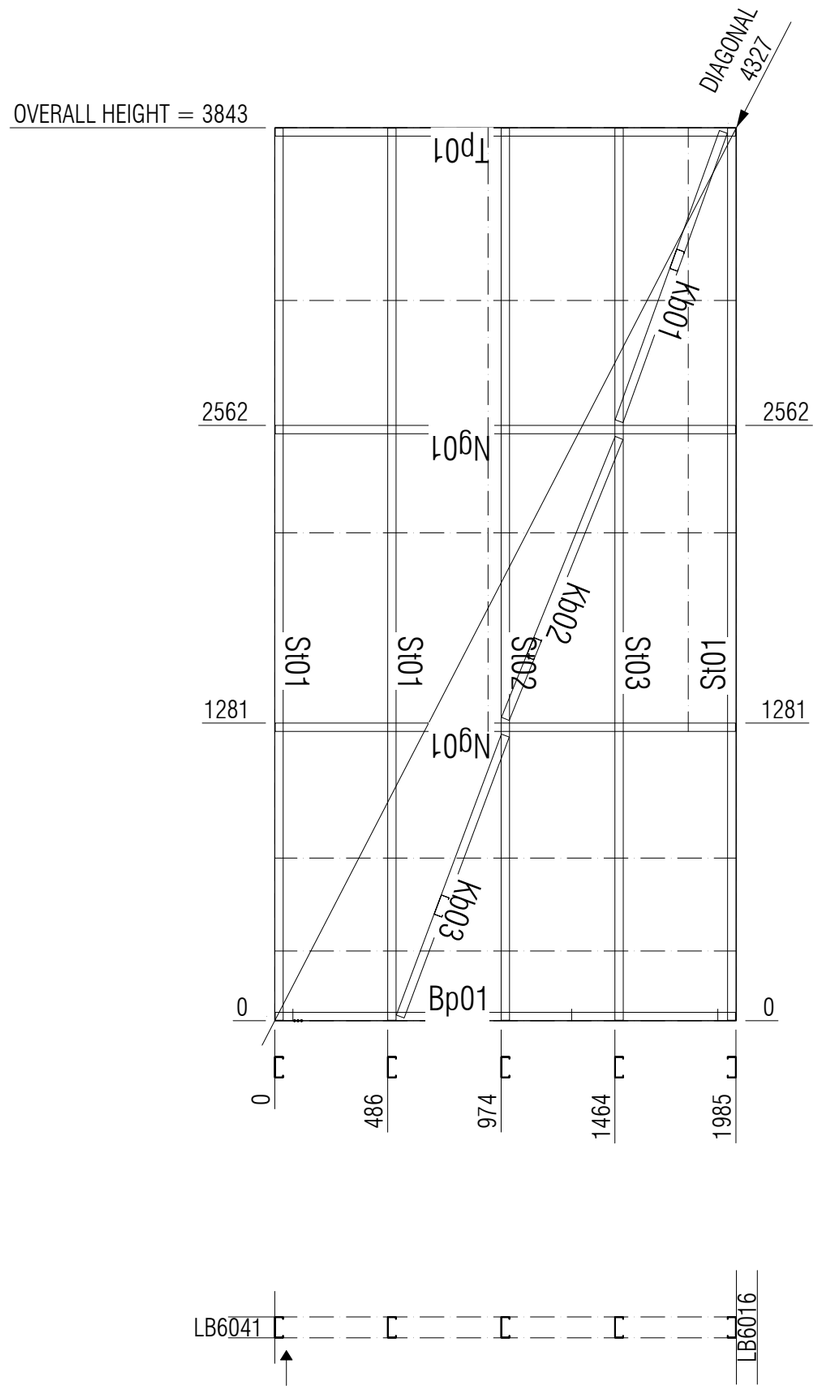

FRAME STICKS

NAME	LENGTH	WT	QTY	PROFILE
Tp01	1981	2.5	1	89S36-950-500
Bp01	1981	2.5	1	89S36-950-500
St01	3839	4.9	3	89S36-950-500
St02	3839	4.9	1	89S36-950-500
St03	3839	4.9	1	89S36-950-500
Ng01	1981	2.5	2	89S36-950-500
Kb01	1324	1.7	1	89S36-950-500
Kb02	1304	1.7	1	89S36-950-500
Kb03	1291	1.7	1	89S36-950-500
TOTAL	31040	39.7	12	

LB6042


AUSTRUSS
www.austruss.com.au (02) 4860 1400

DRAWN
Mitchell.H
Ph:02 4860 1426

ISSUE	DATE	DESCRIPTION OF REVISION
0	05/03/26	IFA
A	03/05/26	IFC
B	06/05/26	IFC
C	08/05/26	IFC
D	11/05/26	IFC

DWG FILE: ####

Client/Company Name: Taylor
Project Name: Blayney
Building / Zone / Area: Zone 6
Job Number: 23314
Project Address: 3 Osman st, Blayney NSW 2799
Drawing Name: 90mm LB Wall production
Drawing Number: LGS-6-201
Revision: D
NOTE: USE PROVIDED DIMENSIONS ONLY. IF NOT PROVIDED, ASK.
Scale: NTS

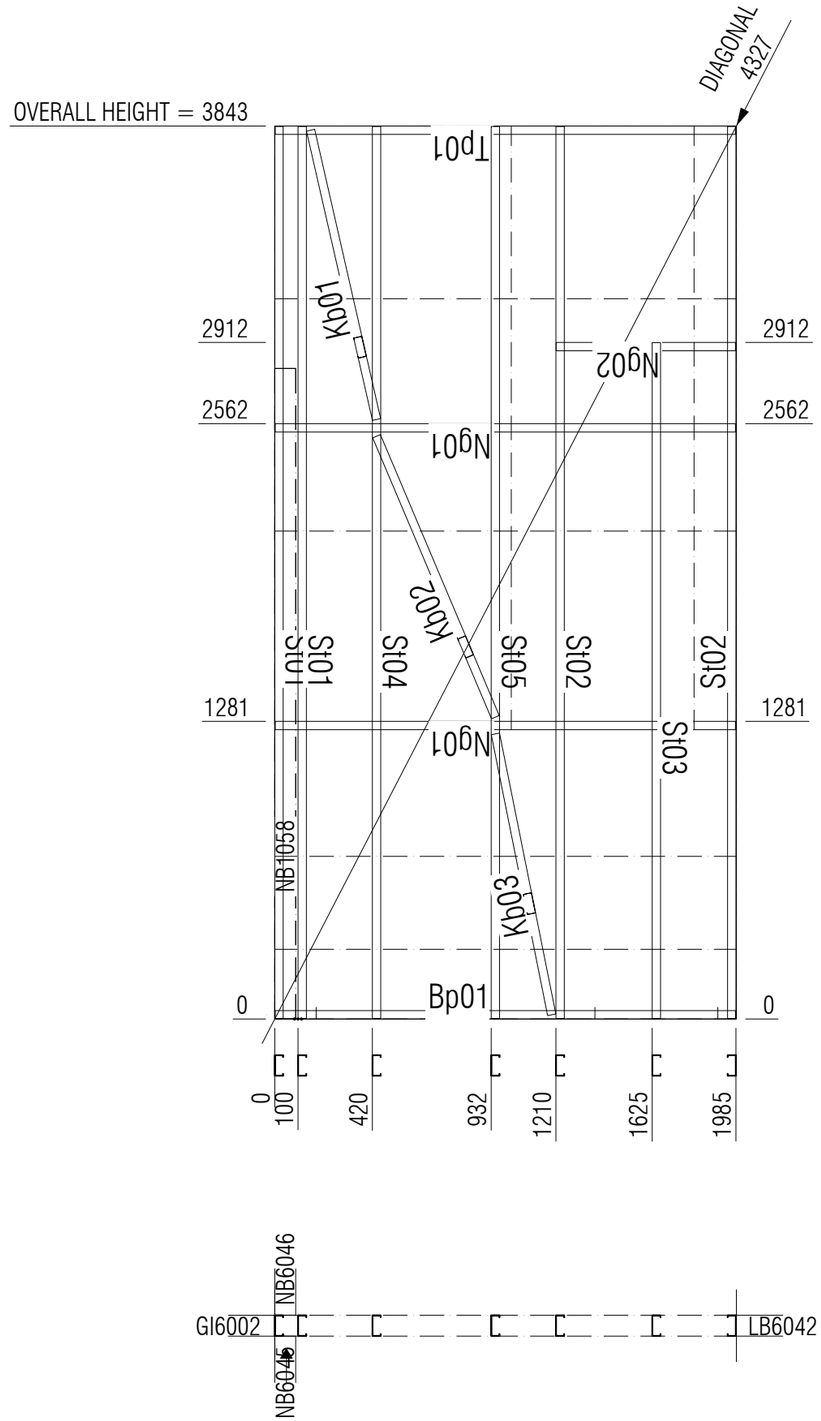

FRAME STICKS

NAME	LENGTH	WT	QTY	PROFILE
Tp01	1981	2.5	1	89S36-950-500
Bp01	1981	2.5	1	89S36-950-500
St01	3839	4.9	2	89S36-950-500
St02	3839	4.9	2	89S36-950-500
St03	2909	3.7	1	89S36-950-500
St04	3839	4.9	1	89S36-950-500
St05	3839	4.9	1	89S36-950-500
Ng01	1981	2.5	2	89S36-950-500
Ng02	772	1.0	1	89S36-950-500
Kb01	1277	1.6	1	89S36-950-500
Kb02	1313	1.7	1	89S36-950-500
Kb03	1233	1.6	1	89S36-950-500
TOTAL	38465	49.2	15	


LB6041

AUSTRUSS
www.austruss.com.au (02) 4860 1400

DRAWN Mitchell.H
Ph:02 4860 1426

ISSUE	DATE	DESCRIPTION OF REVISION
0	05/03/26	IFA
A	03/05/26	IFC
B	06/05/26	IFC
C	08/05/26	IFC
D	11/05/26	IFC

Client/Company Name: Taylor
Project Name: Blayney
Building / Zone / Area: Zone 6
Job Number: 23314
Project Address: 3 Osman st, Blayney NSW 2799
Drawing Name: 90mm LB Wall production
Drawing Number: LGS-6-201
Revision: D
NOTE: USE PROVIDED DIMENSIONS ONLY. IF NOT PROVIDED, ASK.
Scale: NTS
DWG FILE: ####

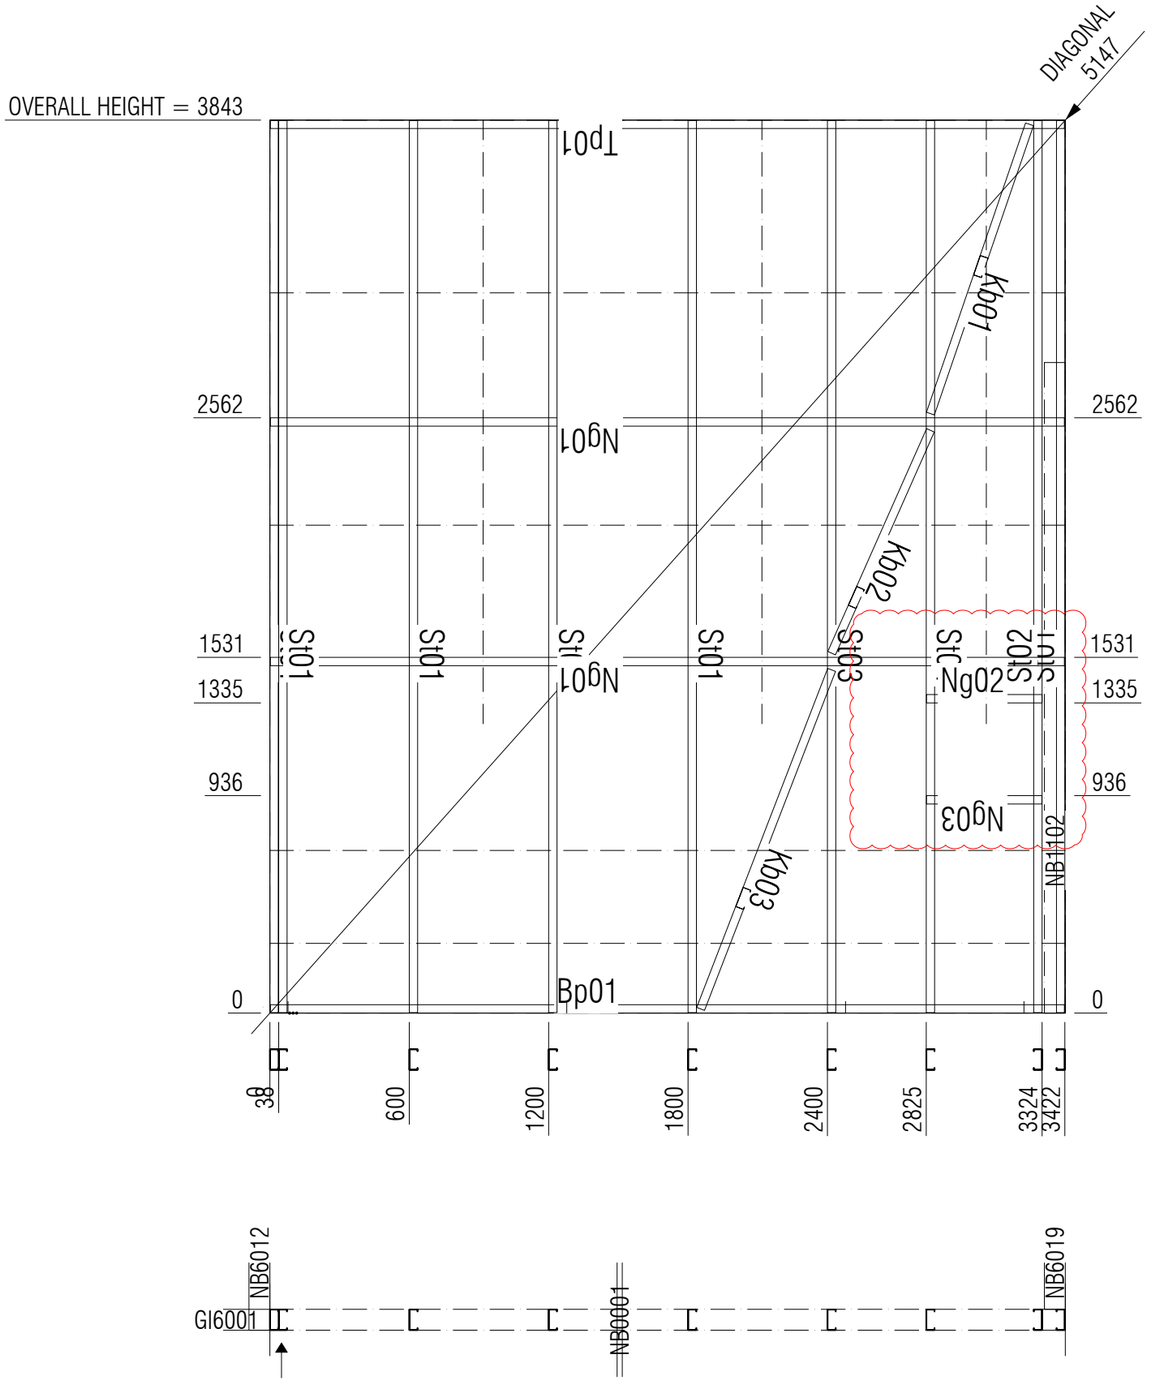

FRAME STICKS

NAME	LENGTH	WT	QTY	PROFILE
Tp01	3418	4.4	1	89S36-950-500
Bp01	3418	4.4	1	89S36-950-500
St01	3839	4.9	6	89S36-950-500
St02	3839	4.9	1	89S36-950-500
St03	3839	4.9	1	89S36-950-500
St04	3839	4.9	1	89S36-950-500
Ng01	3418	4.4	2	89S36-950-500
Ng02	498	0.6	1	89S36-950-500
Ng03	497	0.6	1	89S36-950-500
Kb01	1316	1.7	1	89S36-950-500
Kb02	1049	1.3	1	89S36-950-500
Kb03	1564	2.0	1	89S36-950-500
TOTAL	53150	68.0	18	


LB6034

AUSTRUSS
www.austruss.com.au (02) 4860 1400
DWG FILE: ####

DRAWN Mitchell.H
Ph:02 4860 1426

ISSUE	DATE	DESCRIPTION OF REVISION
0	05/03/26	IFA
A	03/05/26	IFC
B	06/05/26	IFC
C	08/05/26	IFC
D	11/05/26	IFC

Client/Company Name: Taylor
Project Name: Blayney
Project Address: 3 Osman st, Blayney NSW 2799
NOTE: USE PROVIDED DIMENSIONS ONLY. IF NOT PROVIDED, ASK.
Scale: NTS
Building / Zone / Area: Zone 6
Job Number: 23314
Drawing Name: 90mm LB Wall production
Drawing Number: LGS-6-201
Revision: D

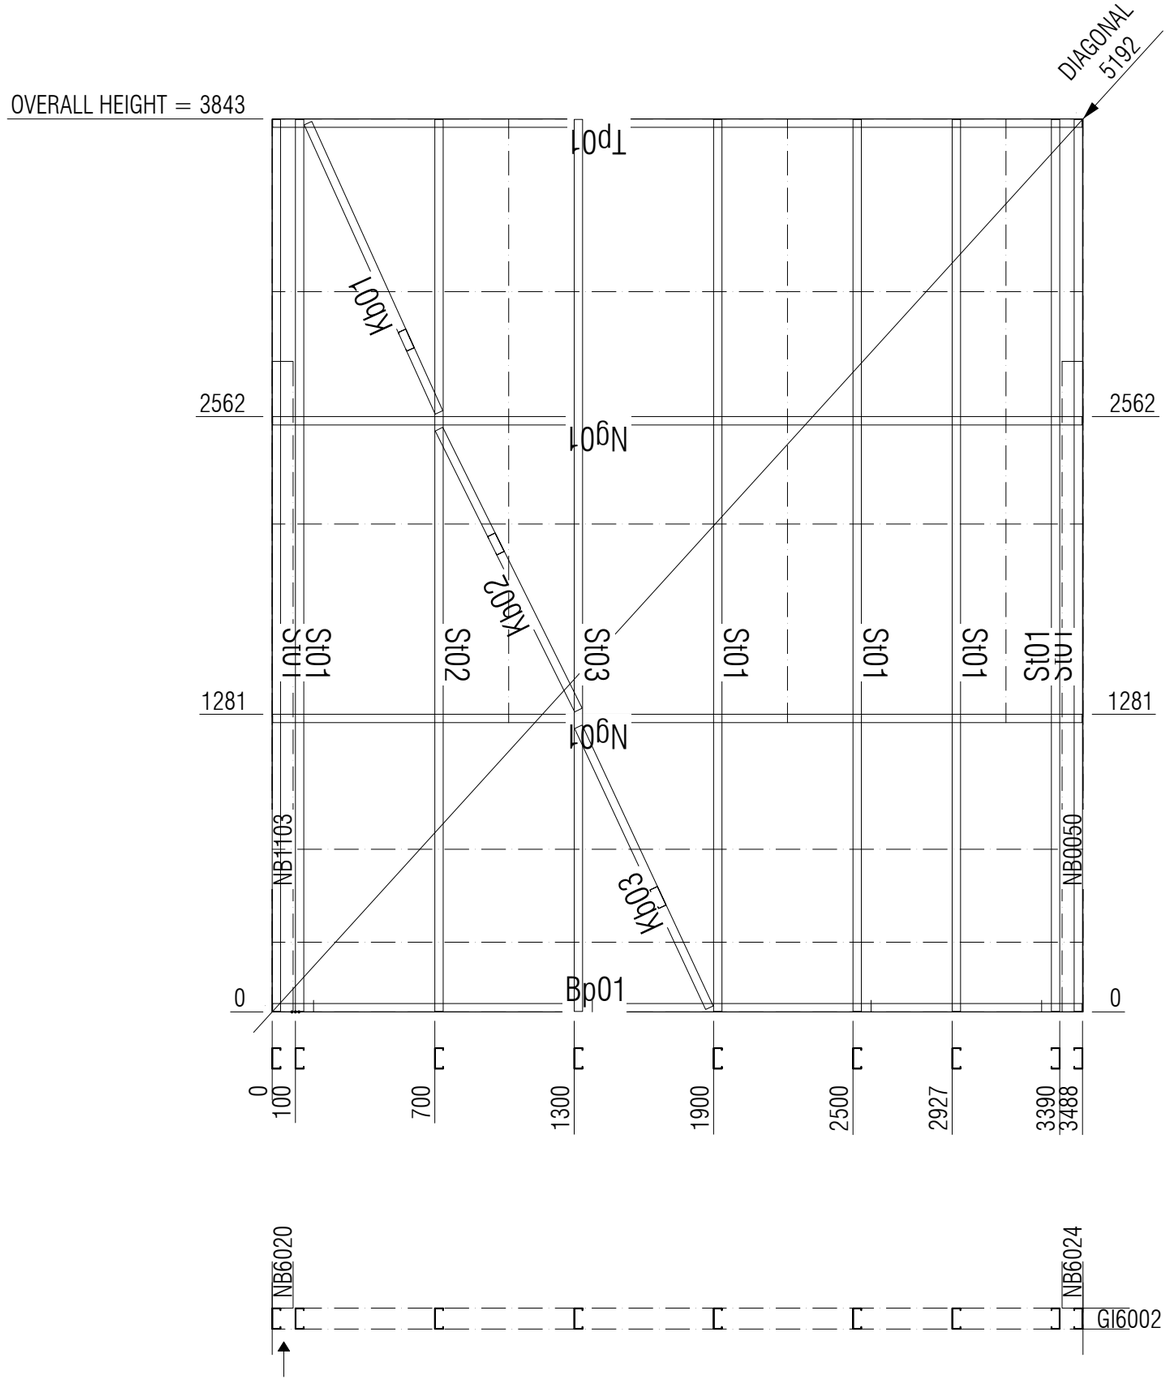

FRAME STICKS

NAME	LENGTH	WT	QTY	PROFILE
Tp01	3484	4.5	1	89S36-950-500
Bp01	3484	4.5	1	89S36-950-500
St01	3839	4.9	7	89S36-950-500
St02	3839	4.9	1	89S36-950-500
St03	3839	4.9	1	89S36-950-500
Ng01	3484	4.5	2	89S36-950-500
Kb01	1367	1.7	1	89S36-950-500
Kb02	1350	1.7	1	89S36-950-500
Kb03	1334	1.7	1	89S36-950-500
TOTAL	52542	67.3	16	

LB6038


AUSTRUSS
www.austruss.com.au (02) 4860 1400

DWG FILE: ####

DRAWN
Mitchell.H
Ph:02 4860 1426

ISSUE	DATE	DESCRIPTION OF REVISION
0	05/03/26	IFA
A	03/05/26	IFC
B	06/05/26	IFC
C	08/05/26	IFC
D	11/05/26	IFC

Client/Company Name: Taylor
Project Name: Blayney
Building / Zone / Area: Zone 6
Job Number: 23314
Project Address: 3 Osman st, Blayney NSW 2799
Drawing Name: 90mm LB Wall production
Drawing Number: LGS-6-201
Revision: D
NOTE: USE PROVIDED DIMENSIONS ONLY. IF NOT PROVIDED, ASK.
Scale: NTS

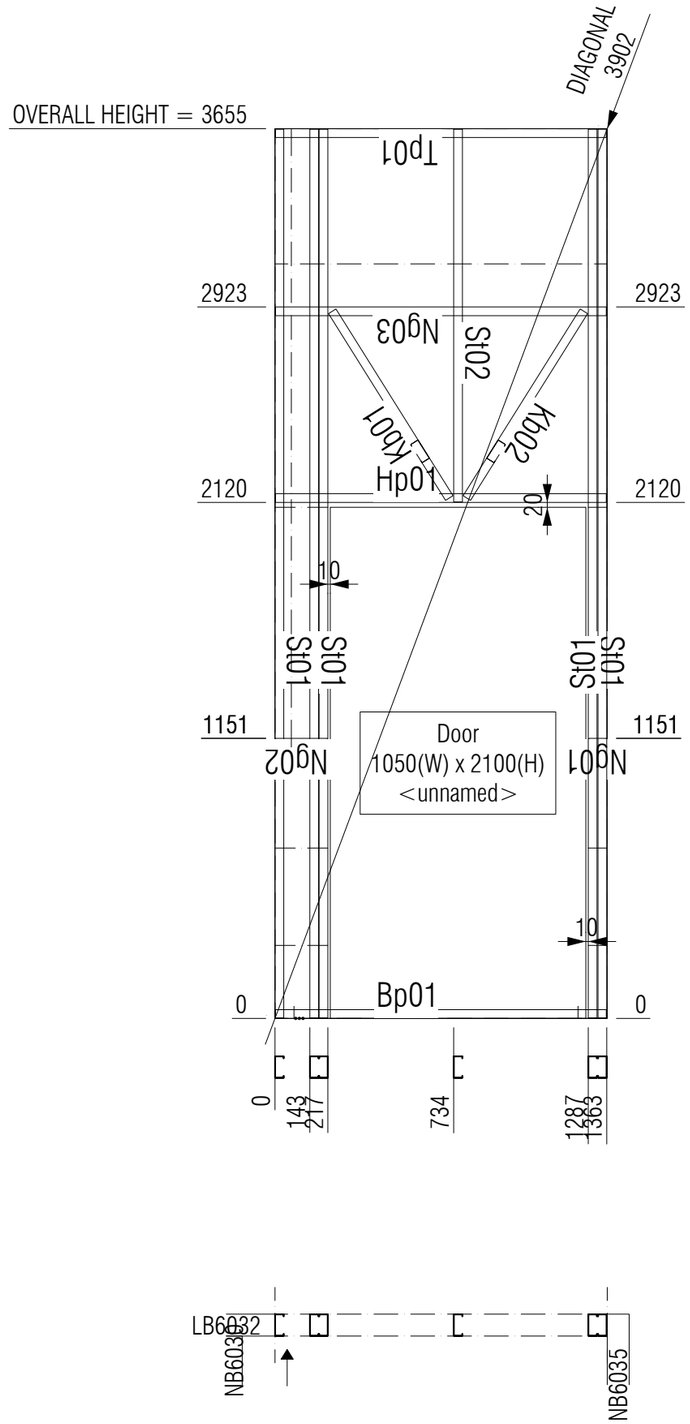

FRAME STICKS

NAME	LENGTH	WT	QTY	PROFILE
Tp01	1359	1.7	1	89S36-950-500
Bp01	1359	1.7	1	89S36-950-500
St01	3651	4.7	5	89S36-950-500
St02	1531	2.0	1	89S36-950-500
Ng01	72	0.1	1	89S36-950-500
Ng02	213	0.3	1	89S36-950-500
Ng03	1359	1.7	1	89S36-950-500
Kb01	906	1.2	1	89S36-950-500
Kb02	906	1.2	1	89S36-950-500
Hp01	1359	1.7	1	89S36-950-500
TOTAL	27321	35.0	14	

LB6033


AUSTRUSS
www.austruss.com.au (02) 4860 1400

DWG FILE: ####

DRAWN
Mitchell.H
Ph:02 4860 1426

ISSUE	DATE	DESCRIPTION OF REVISION
0	05/03/26	IFA
A	03/05/26	IFC
B	06/05/26	IFC
C	08/05/26	IFC
D	11/05/26	IFC

Client/Company Name: Taylor
Project Name: Blayney
Building / Zone / Area: Zone 6
Job Number: 23314
Project Address: 3 Osman st, Blayney NSW 2799
Drawing Name: 90mm LB Wall production
Drawing Number: LGS-6-201
Revision: D
NOTE: USE PROVIDED DIMENSIONS ONLY. IF NOT PROVIDED, ASK.
Scale: NTS

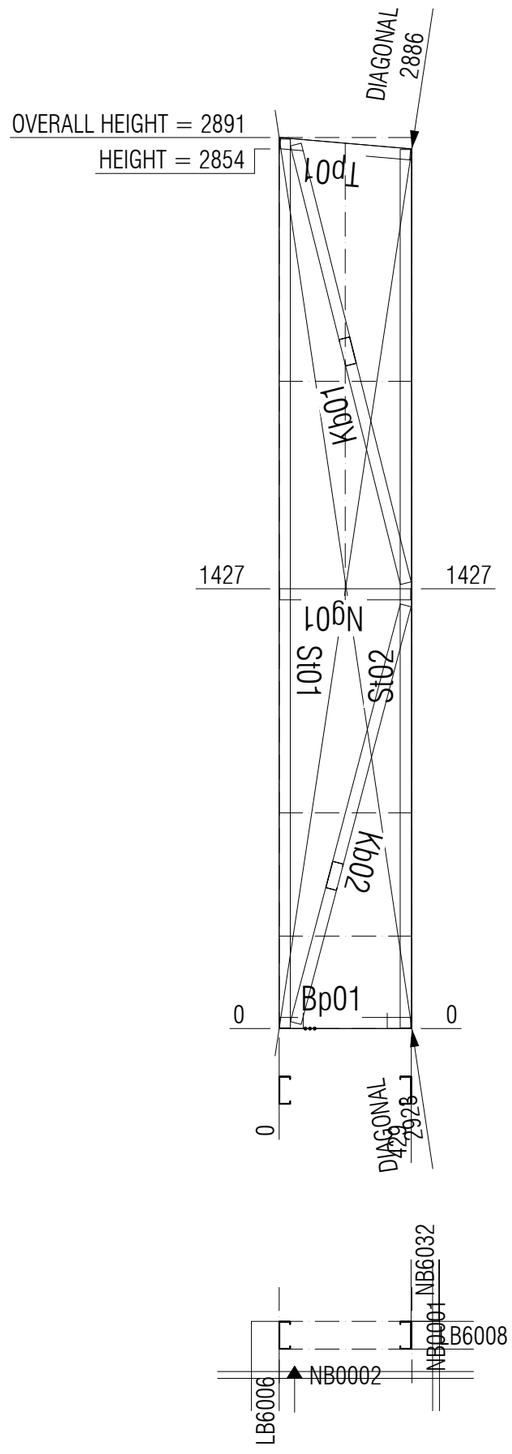

FRAME STICKS

NAME	LENGTH	WT	QTY	PROFILE
Tp01	423	0.5	1	89S36-950-500
Bp01	425	0.5	1	89S36-950-500
St01	2884	3.7	1	89S36-950-500
St02	2850	3.6	1	89S36-950-500
Ng01	425	0.5	1	89S36-950-500
Kb01	1467	1.9	1	89S36-950-500
Kb02	1401	1.8	1	89S36-950-500
TOTAL	9874	12.6	7	

LB6007


AUSTRUSS
www.austruss.com.au (02) 4860 1400
DWG FILE: ####

DRAWN
Mitchell.H
Ph:02 4860 1426

ISSUE	DATE	DESCRIPTION OF REVISION
0	05/03/26	IFA
A	03/05/26	IFC
B	06/05/26	IFC
C	08/05/26	IFC
D	11/05/26	IFC

Client/Company Name: Taylor
Project Name: Blayney
Building / Zone / Area: Zone 6
Job Number: 23314
Project Address: 3 Osman st, Blayney NSW 2799
Drawing Name: 90mm LB Wall production
Drawing Number: LGS-6-201
Revision: D
NOTE: USE PROVIDED DIMENSIONS ONLY. IF NOT PROVIDED, ASK.
Scale: NTS

DOUBLE SCREW

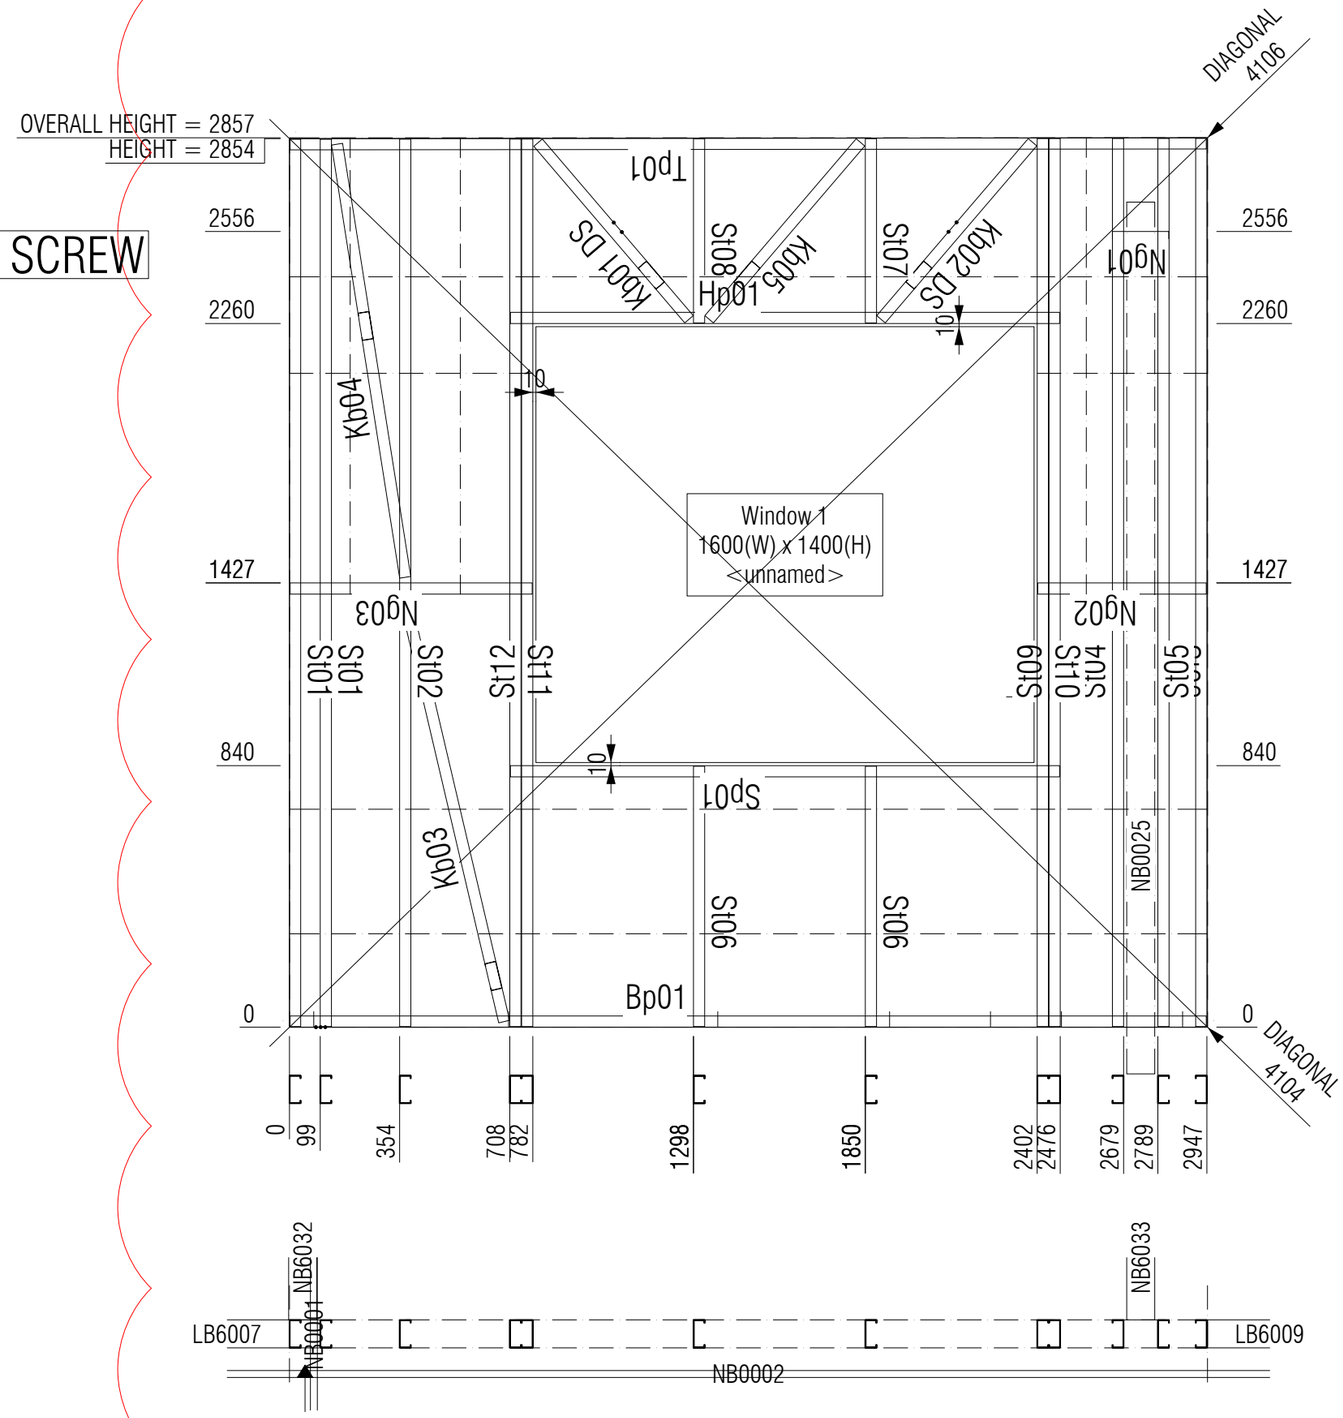

FRAME STICKS

NAME	LENGTH	WT	QTY	PROFILE
Tp01	2943	3.8	1	89S36-950-500
Bp01	2943	3.8	1	89S36-950-500
St01	2850	3.6	2	89S36-950-500
St02	2850	3.6	1	89S36-950-500
St03	2852	3.7	1	89S36-950-500
St04	2852	3.7	1	89S36-950-500
St05	2853	3.7	1	89S36-950-500
St06	836	1.1	2	89S36-950-500
St07	592	0.8	1	89S36-950-500
St08	591	0.8	1	89S36-950-500
St09	2852	3.7	1	89S36-950-500
St10	2852	3.7	1	89S36-950-500
St11	2851	3.6	1	89S36-950-500
St12	2851	3.6	1	89S36-950-500
Ng01	181	0.2	1	89S36-950-500
Ng02	541	0.7	1	89S36-950-500
Ng03	778	1.0	1	89S36-950-500
Kb01 DS	746	1.0	1	89S36-950-500
Kb02 DS	749	1.0	1	89S36-950-500
Kb03	1392	1.8	1	89S36-950-500
Kb04	1408	1.8	1	89S36-950-500
Kb05	748	1.0	1	89S36-950-500
Hp01	1764	2.3	1	89S36-950-500
Sp01	1764	2.3	1	89S36-950-500
TOTAL	47323	60.6	26	

LB6008


AUSTRUSS
www.austruss.com.au (02) 4860 1400

DWG FILE: ####

DRAWN Mitchell.H
Ph:02 4860 1426

ISSUE	DATE	DESCRIPTION OF REVISION
0	05/03/26	IFA
A	03/05/26	IFC
B	06/05/26	IFC
C	08/05/26	IFC
D	11/05/26	IFC

Client/Company Name: Taylor
Project Name: Blayney
Building / Zone / Area: Zone 6
Job Number: 23314
Project Address: 3 Osman st, Blayney NSW 2799
Drawing Name: 90mm LB Wall production
Drawing Number: LGS-6-201
Revision: D
NOTE: USE PROVIDED DIMENSIONS ONLY. IF NOT PROVIDED, ASK.
Scale: NTS

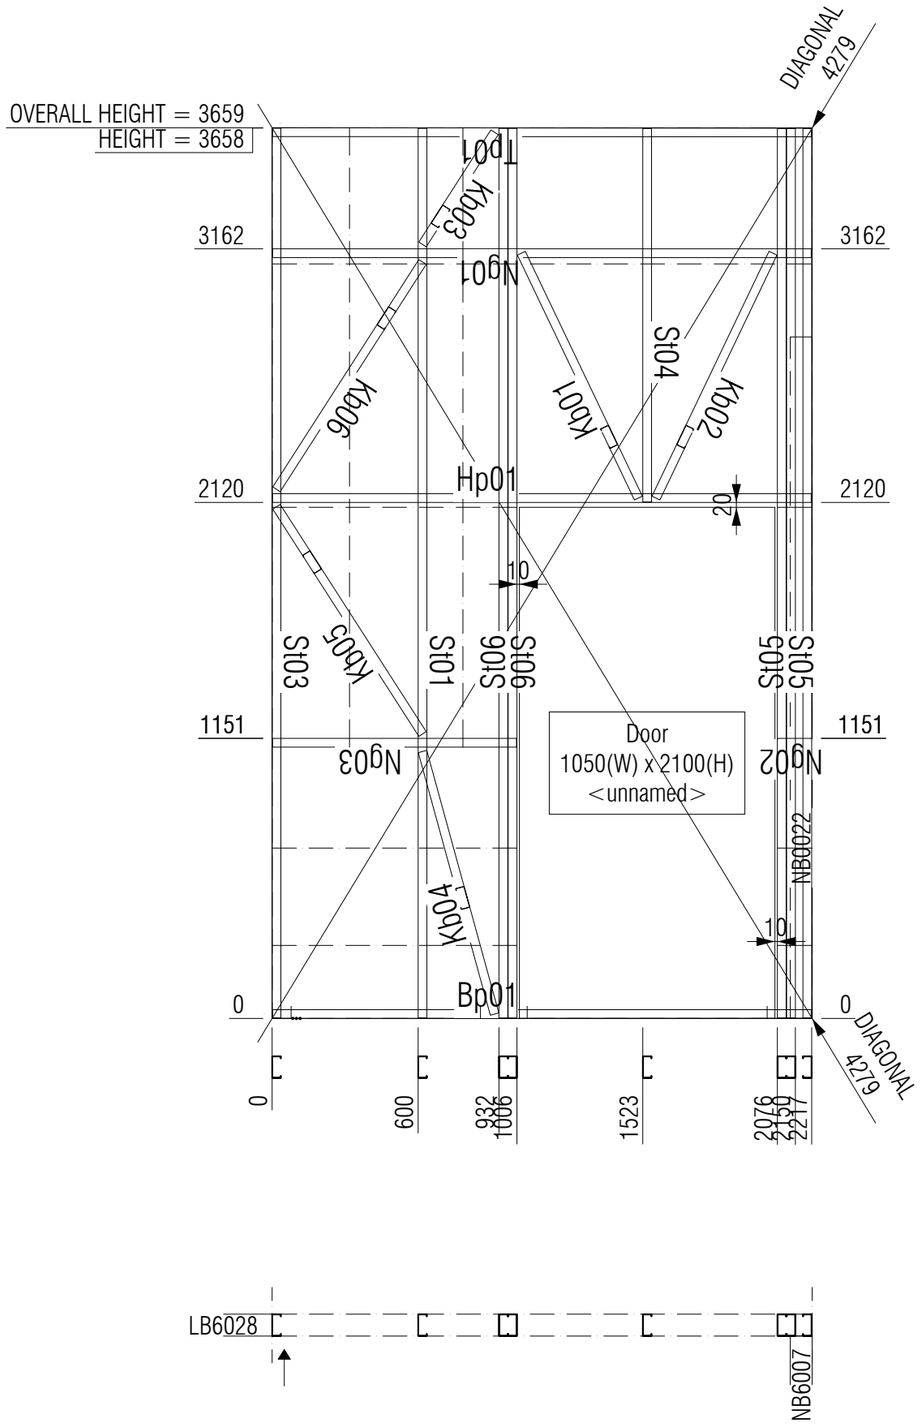

FRAME STICKS

NAME	LENGTH	WT	QTY	PROFILE
Tp01	2213	2.8	1	89S36-950-500
Bp01	2213	2.8	1	89S36-950-500
St01	3655	4.7	1	89S36-950-500
St02	3654	4.7	1	89S36-950-500
St03	3655	4.7	1	89S36-950-500
St04	1534	2.0	1	89S36-950-500
St05	3654	4.7	2	89S36-950-500
St06	3655	4.7	2	89S36-950-500
Ng01	2213	2.8	1	89S36-950-500
Ng02	137	0.2	1	89S36-950-500
Ng03	1002	1.3	1	89S36-950-500
Kb01	1115	1.4	1	89S36-950-500
Kb02	1115	1.4	1	89S36-950-500
Kb03	548	0.7	1	89S36-950-500
Kb04	1119	1.4	1	89S36-950-500
Kb05	1110	1.4	1	89S36-950-500
Kb06	1110	1.4	1	89S36-950-500
Hp01	2213	2.8	1	89S36-950-500
TOTAL	43223	55.3	20	

LB6029


AUSTRUSS
www.austruss.com.au (02) 4860 1400

DWG FILE: ####

DRAWN Mitchell.H
Ph:02 4860 1426

ISSUE	DATE	DESCRIPTION OF REVISION
0	05/03/26	IFA
A	03/05/26	IFC
B	06/05/26	IFC
C	08/05/26	IFC
D	11/05/26	IFC

Client/Company Name: Taylor
Project Name: Blayney
Project Address: 3 Osman st, Blayney NSW 2799
NOTE: USE PROVIDED DIMENSIONS ONLY. IF NOT PROVIDED, ASK.
Scale: NTS
Building / Zone / Area: Zone 6
Job Number: 23314
Drawing Name: 90mm LB Wall production
Drawing Number: LGS-6-201
Revision: D

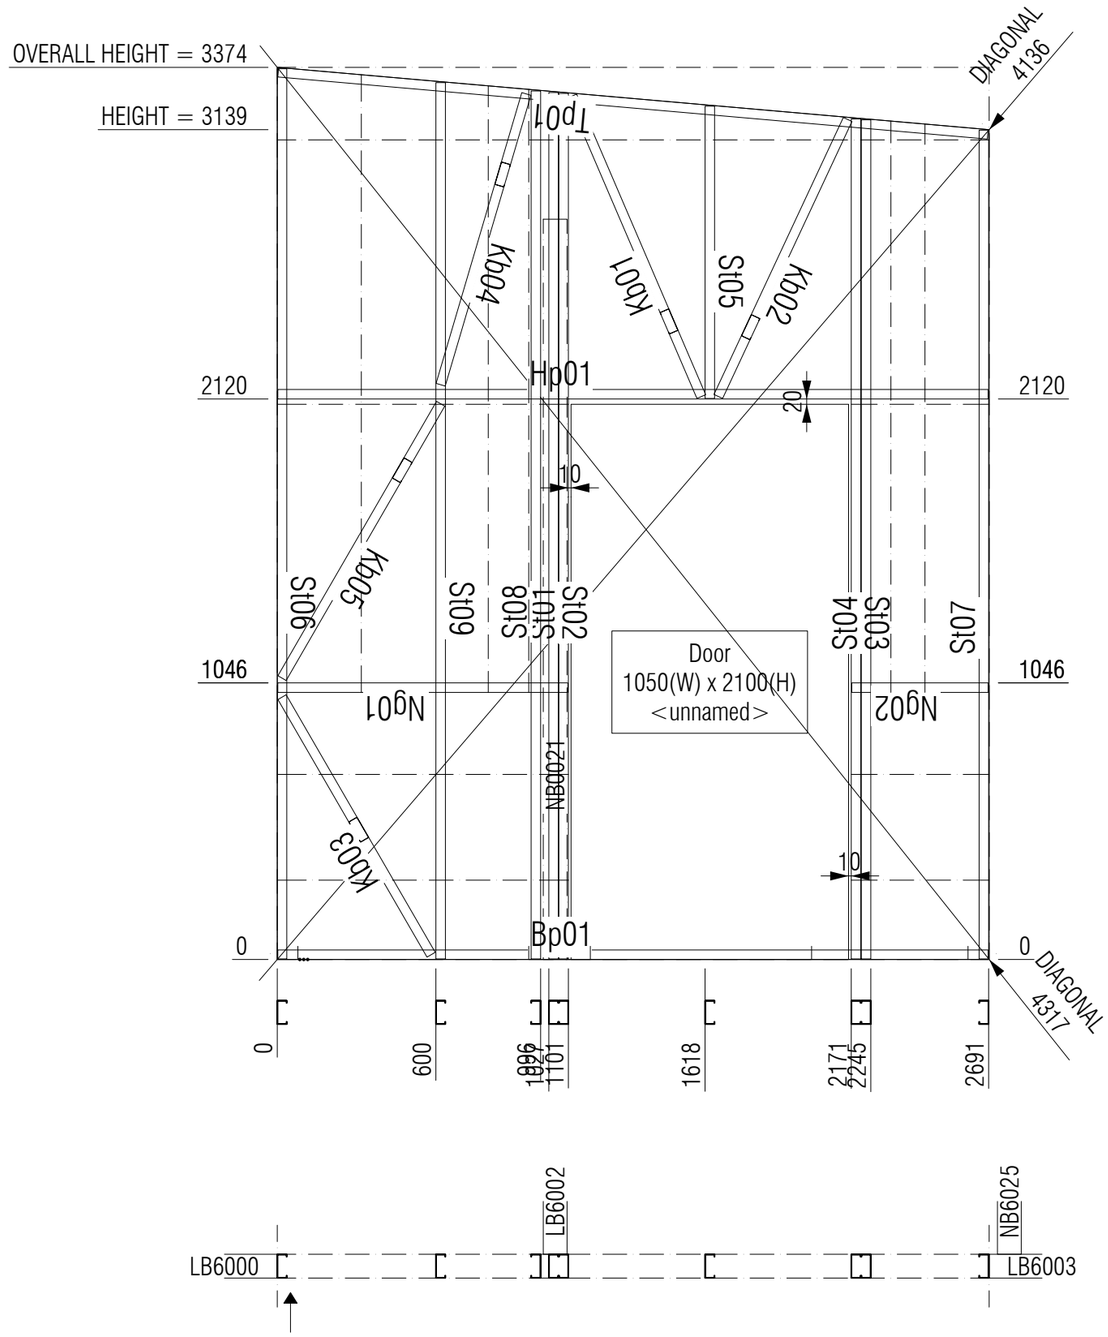

FRAME STICKS

NAME	LENGTH	WT	QTY	PROFILE
Tp01	2694	3.4	1	89S36-950-500
Bp01	2687	3.4	1	89S36-950-500
St01	3274	4.2	1	89S36-950-500
St02	3277	4.2	1	89S36-950-500
St03	3177	4.1	1	89S36-950-500
St04	3174	4.1	1	89S36-950-500
St05	1106	1.4	1	89S36-950-500
St06	3367	4.3	1	89S36-950-500
St07	3135	4.0	1	89S36-950-500
St08	3283	4.2	1	89S36-950-500
St09	3315	4.2	1	89S36-950-500
Ng01	1097	1.4	1	89S36-950-500
Ng02	516	0.7	1	89S36-950-500
Kb01	1237	1.6	1	89S36-950-500
Kb02	1156	1.5	1	89S36-950-500
Kb03	1126	1.4	1	89S36-950-500
Kb04	1147	1.5	1	89S36-950-500
Kb05	1199	1.5	1	89S36-950-500
Hp01	2687	3.4	1	89S36-950-500
TOTAL	42653	54.6	19	

LB6001

AUSTRUSS
www.austruss.com.au (02) 4860 1400


DWG FILE: ####

DRAWN Mitchell.H Ph:02 4860 1426

ISSUE	DATE	DESCRIPTION OF REVISION
0	05/03/26	IFA
A	03/05/26	IFC
B	06/05/26	IFC
C	08/05/26	IFC
D	11/05/26	IFC

Client/Company Name: Taylor
Project Name: Blayney
Building / Zone / Area: Zone 6
Job Number: 23314
Project Address: 3 Osman st, Blayney NSW 2799
Drawing Name: 90mm LB Wall production
Drawing Number: LGS-6-201
Revision: D
NOTE: USE PROVIDED DIMENSIONS ONLY. IF NOT PROVIDED, ASK.
Scale: NTS

DOUBLE SCREW

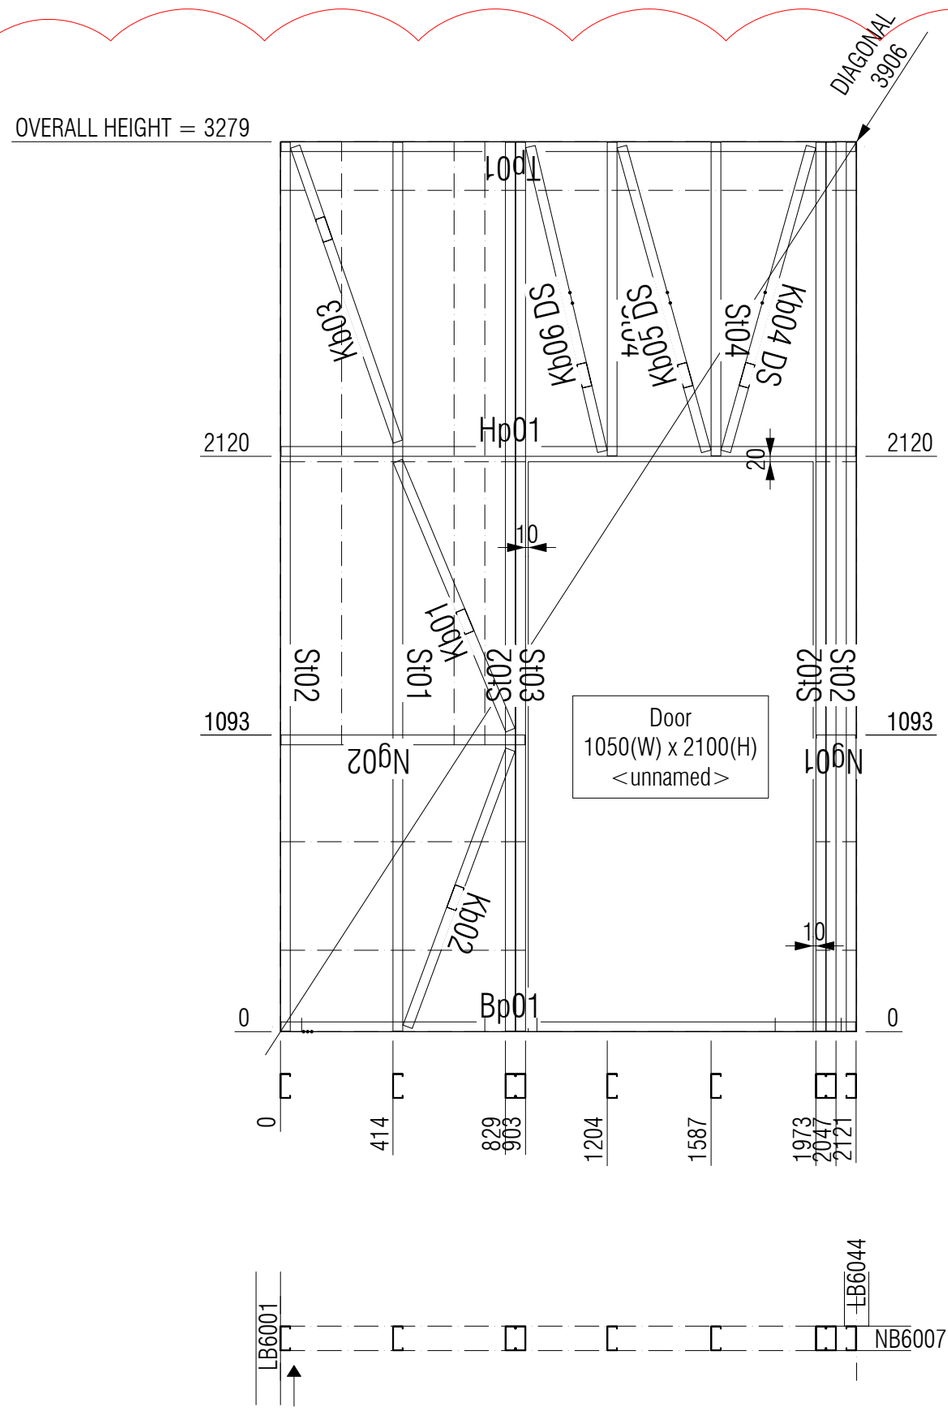

FRAME STICKS

NAME	LENGTH	WT	QTY	PROFILE
Tp01	2117	2.7	1	89S36-950-500
Bp01	2117	2.7	1	89S36-950-500
St01	3275	4.2	1	89S36-950-500
St02	3275	4.2	5	89S36-950-500
St03	3275	4.2	1	89S36-950-500
St04	1155	1.5	2	89S36-950-500
Ng01	144	0.2	1	89S36-950-500
Ng02	899	1.2	1	89S36-950-500
Kb01	1074	1.4	1	89S36-950-500
Kb02	1089	1.4	1	89S36-950-500
Kb03	1151	1.5	1	89S36-950-500
Kb04 DS	1166	1.5	1	89S36-950-500
Kb05 DS	1165	1.5	1	89S36-950-500
Kb06 DS	1154	1.5	1	89S36-950-500
Hp01	2117	2.7	1	89S36-950-500
TOTAL	39429	50.5	20	

LB6002

AUSTRUSS
www.austruss.com.au (02) 4860 1400


DWG FILE: ####

DRAWN
Mitchell.H
Ph:02 4860 1426

ISSUE	DATE	DESCRIPTION OF REVISION
0	05/03/26	IFA
A	03/05/26	IFC
B	06/05/26	IFC
C	08/05/26	IFC
D	11/05/26	IFC

Client/Company Name: Taylor
Project Name: Blayney
Building / Zone / Area: Zone 6
Job Number: 23314
Project Address: 3 Osman st, Blayney NSW 2799
Drawing Name: 90mm LB Wall production
Drawing Number: LGS-6-201
Revision: D
NOTE: USE PROVIDED DIMENSIONS ONLY. IF NOT PROVIDED, ASK.
Scale: NTS

THIS WALL WILL HAVE LEAD PANELS AT 10kg/m²

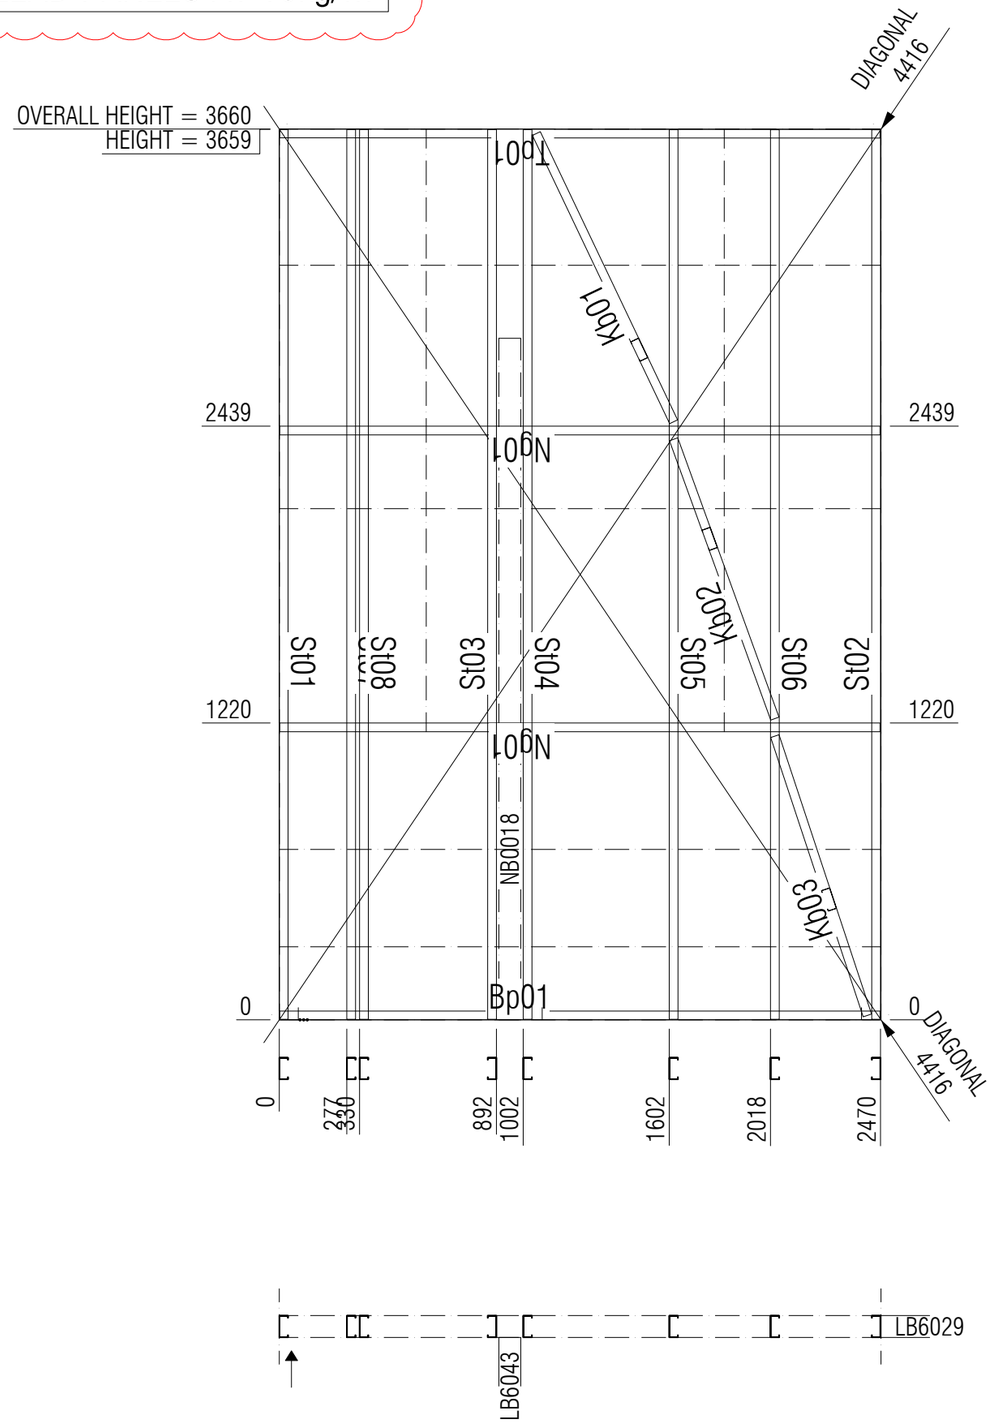

FRAME STICKS

NAME	LENGTH	WT	QTY	PROFILE
Tp01	2466	3.2	1	89S36-950-500
Bp01	2466	3.2	1	89S36-950-500
St01	3656	4.7	1	89S36-950-500
St02	3655	4.7	1	89S36-950-500
St03	3655	4.7	1	89S36-950-500
St04	3655	4.7	1	89S36-950-500
St05	3655	4.7	1	89S36-950-500
St06	3655	4.7	1	89S36-950-500
St07	3656	4.7	1	89S36-950-500
St08	3656	4.7	1	89S36-950-500
Ng01	2466	3.2	2	89S36-950-500
Kb01	1312	1.7	1	89S36-950-500
Kb02	1221	1.6	1	89S36-950-500
Kb03	1209	1.5	1	89S36-950-500
TOTAL	42848	54.8	15	

LB6028


AUSTRUSS
www.austruss.com.au (02) 4860 1400

DWG FILE: ####

DRAWN
Mitchell.H
Ph:02 4860 1426

ISSUE	DATE	DESCRIPTION OF REVISION
0	05/03/26	IFA
A	03/05/26	IFC
B	06/05/26	IFC
C	08/05/26	IFC
D	11/05/26	IFC

Client/Company Name: Taylor
Project Name: Blayney
Building / Zone / Area: Zone 6
Job Number: 23314
Project Address: 3 Osman st, Blayney NSW 2799
Drawing Name: 90mm LB Wall production
Drawing Number: LGS-6-201
Revision: D
NOTE: USE PROVIDED DIMENSIONS ONLY. IF NOT PROVIDED, ASK.
Scale: NTS

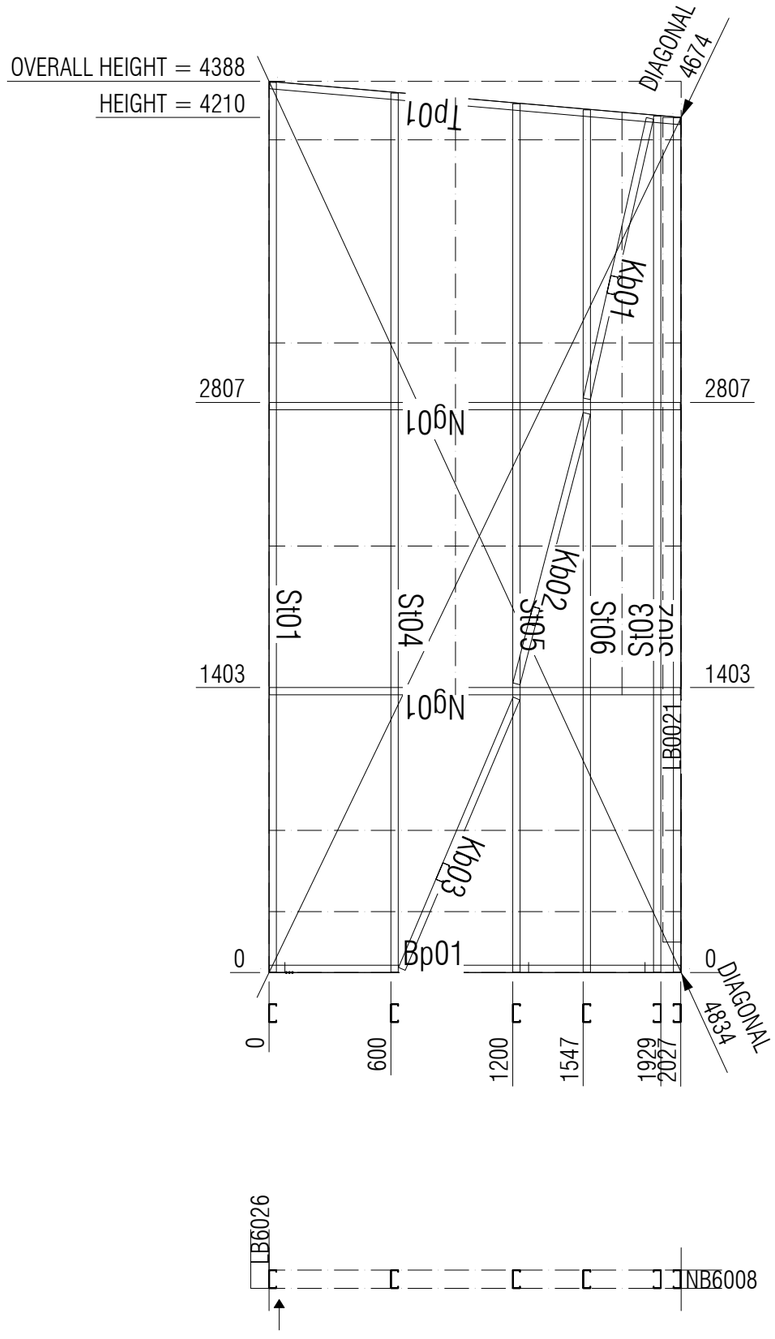

FRAME STICKS

NAME	LENGTH	WT	QTY	PROFILE
Tp01	2028	2.6	1	89S36-950-500
Bp01	2023	2.6	1	89S36-950-500
St01	4381	5.6	1	89S36-950-500
St02	4207	5.4	1	89S36-950-500
St03	4215	5.4	1	89S36-950-500
St04	4328	5.5	1	89S36-950-500
St05	4276	5.5	1	89S36-950-500
St06	4245	5.4	1	89S36-950-500
Ng01	2023	2.6	2	89S36-950-500
Kb01	1415	1.8	1	89S36-950-500
Kb02	1376	1.8	1	89S36-950-500
Kb03	1446	1.9	1	89S36-950-500
TOTAL	37987	48.6	13	

LB6027


AUSTRUSS
www.austruss.com.au (02) 4860 1400
DWG FILE: ####

DRAWN Mitchell.H
Ph:02 4860 1426

ISSUE	DATE	DESCRIPTION OF REVISION
0	05/03/26	IFA
A	03/05/26	IFC
B	06/05/26	IFC
C	08/05/26	IFC
D	11/05/26	IFC

Client/Company Name: Taylor
Project Name: Blayney
Project Address: 3 Osman st, Blayney NSW 2799
NOTE: USE PROVIDED DIMENSIONS ONLY. IF NOT PROVIDED, ASK.
Scale: NTS
Building / Zone / Area: Zone 6
Job Number: 23314
Drawing Name: 90mm LB Wall production
Drawing Number: LGS-6-201
Revision: D

WELD PART

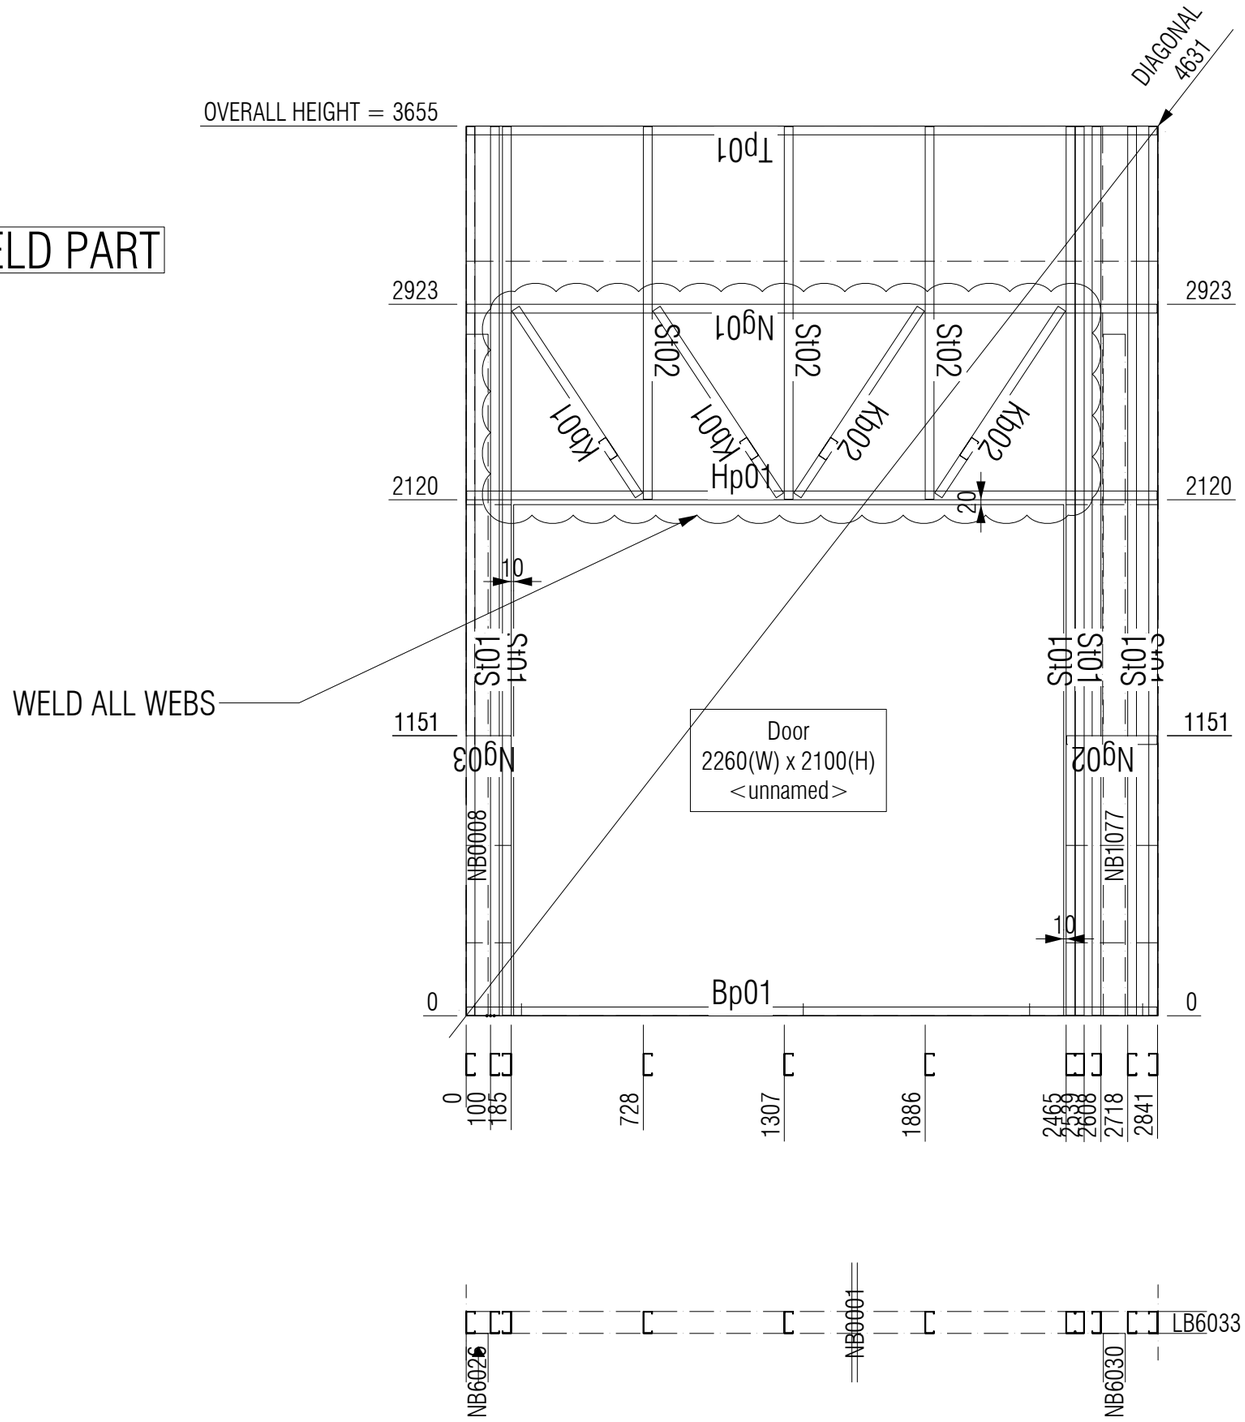

FRAME STICKS

NAME	LENGTH	WT	QTY	PROFILE
Tp01	2837	3.6	1	89S36-950-500
Bp01	2837	3.6	1	89S36-950-500
St01	3651	4.7	8	89S36-950-500
St02	1531	2.0	3	89S36-950-500
Ng01	2837	3.6	1	89S36-950-500
Ng02	372	0.5	1	89S36-950-500
Ng03	181	0.2	1	89S36-950-500
Kb01	920	1.2	2	89S36-950-500
Kb02	920	1.2	2	89S36-950-500
Hp01	2837	3.6	1	89S36-950-500
TOTAL	49382	63.2	21	


LB6032

AUSTRUSS
www.austruss.com.au (02) 4860 1400
DWG FILE: ####

DRAWN Mitchell.H
Ph:02 4860 1426

ISSUE	DATE	DESCRIPTION OF REVISION
0	05/03/26	IFA
A	03/05/26	IFC
B	06/05/26	IFC
C	08/05/26	IFC
D	11/05/26	IFC

Client/Company Name: Taylor
Project Name: Blayney
Building / Zone / Area: Zone 6
Job Number: 23314
Project Address: 3 Osman st, Blayney NSW 2799
NOTE: USE PROVIDED DIMENSIONS ONLY. IF NOT PROVIDED, ASK.
Scale: NTS
Drawing Name: 90mm LB Wall production
Drawing Number: LGS-6-201
Revision: D

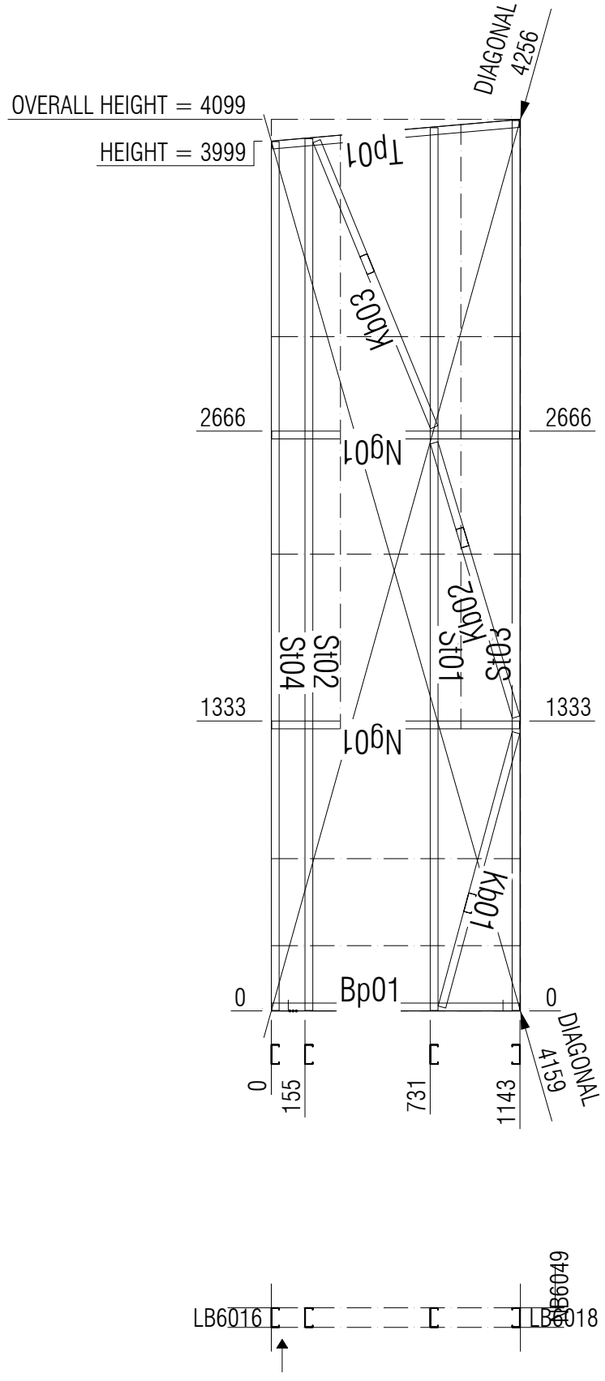

FRAME STICKS

NAME	LENGTH	WT	QTY	PROFILE
Tp01	1140	1.5	1	89S36-950-500
Bp01	1139	1.5	1	89S36-950-500
St01	4059	5.2	1	89S36-950-500
St02	4008	5.1	1	89S36-950-500
St03	4092	5.2	1	89S36-950-500
St04	3995	5.1	1	89S36-950-500
Ng01	1139	1.5	2	89S36-950-500
Kb01	1306	1.7	1	89S36-950-500
Kb02	1316	1.7	1	89S36-950-500
Kb03	1422	1.8	1	89S36-950-500
TOTAL	24755	31.7	11	


LB6017

AUSTRUSS
www.austruss.com.au (02) 4860 1400

DRAWN Mitchell.H
Ph:02 4860 1426

ISSUE	DATE	DESCRIPTION OF REVISION
0	05/03/26	IFA
A	03/05/26	IFC
B	06/05/26	IFC
C	08/05/26	IFC
D	11/05/26	IFC

Client/Company Name: Taylor
Project Name: Blayney
Building / Zone / Area: Zone 6
Job Number: 23314
Project Address: 3 Osman st, Blayney NSW 2799
Drawing Name: 90mm LB Wall production
Drawing Number: LGS-6-201
Revision: D
NOTE: USE PROVIDED DIMENSIONS ONLY. IF NOT PROVIDED, ASK.
Scale: NTS
DWG FILE: ####

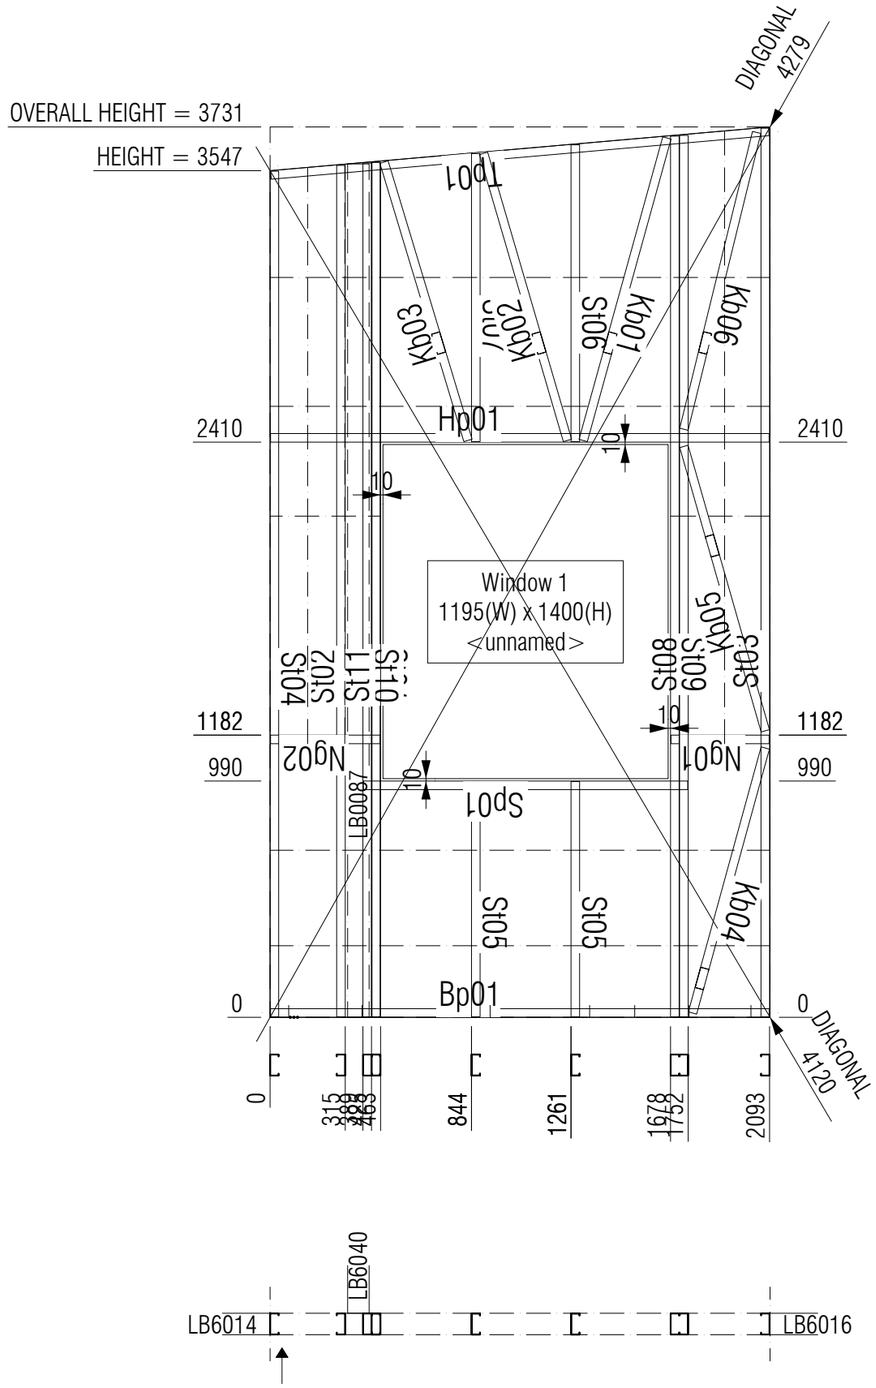

FRAME STICKS

NAME	LENGTH	WT	QTY	PROFILE
Tp01	2094	2.7	1	89S36-950-500
Bp01	2089	2.7	1	89S36-950-500
St01	3580	4.6	1	89S36-950-500
St02	3568	4.6	1	89S36-950-500
St03	3723	4.8	1	89S36-950-500
St04	3543	4.5	1	89S36-950-500
St05	986	1.3	2	89S36-950-500
St06	1244	1.6	1	89S36-950-500
St07	1207	1.5	1	89S36-950-500
St08	3693	4.7	1	89S36-950-500
St09	3690	4.7	1	89S36-950-500
St10	3577	4.6	1	89S36-950-500
St11	3581	4.6	1	89S36-950-500
Ng01	411	0.5	1	89S36-950-500
Ng02	459	0.6	1	89S36-950-500
Kb01	1315	1.7	1	89S36-950-500
Kb02	1253	1.6	1	89S36-950-500
Kb03	1218	1.6	1	89S36-950-500
Kb04	1152	1.5	1	89S36-950-500
Kb05	1239	1.6	1	89S36-950-500
Kb06	1281	1.6	1	89S36-950-500
Hp01	2089	2.7	1	89S36-950-500
Sp01	1359	1.7	1	89S36-950-500
TOTAL	49339	63.2	24	

LB6015


AUSTRUSS
www.austruss.com.au (02) 4860 1400


DWG FILE: ####

DRAWN Mitchell.H
Ph:02 4860 1426

ISSUE	DATE	DESCRIPTION OF REVISION
0	05/03/26	IFA
A	03/05/26	IFC
B	06/05/26	IFC
C	08/05/26	IFC
D	11/05/26	IFC

Client/Company Name: Taylor
Project Name: Blayney
Building / Zone / Area: Zone 6
Job Number: 23314
Project Address: 3 Osman st, Blayney NSW 2799
Drawing Name: 90mm LB Wall production
Drawing Number: LGS-6-201
Revision: D
NOTE: USE PROVIDED DIMENSIONS ONLY. IF NOT PROVIDED, ASK.
Scale: NTS

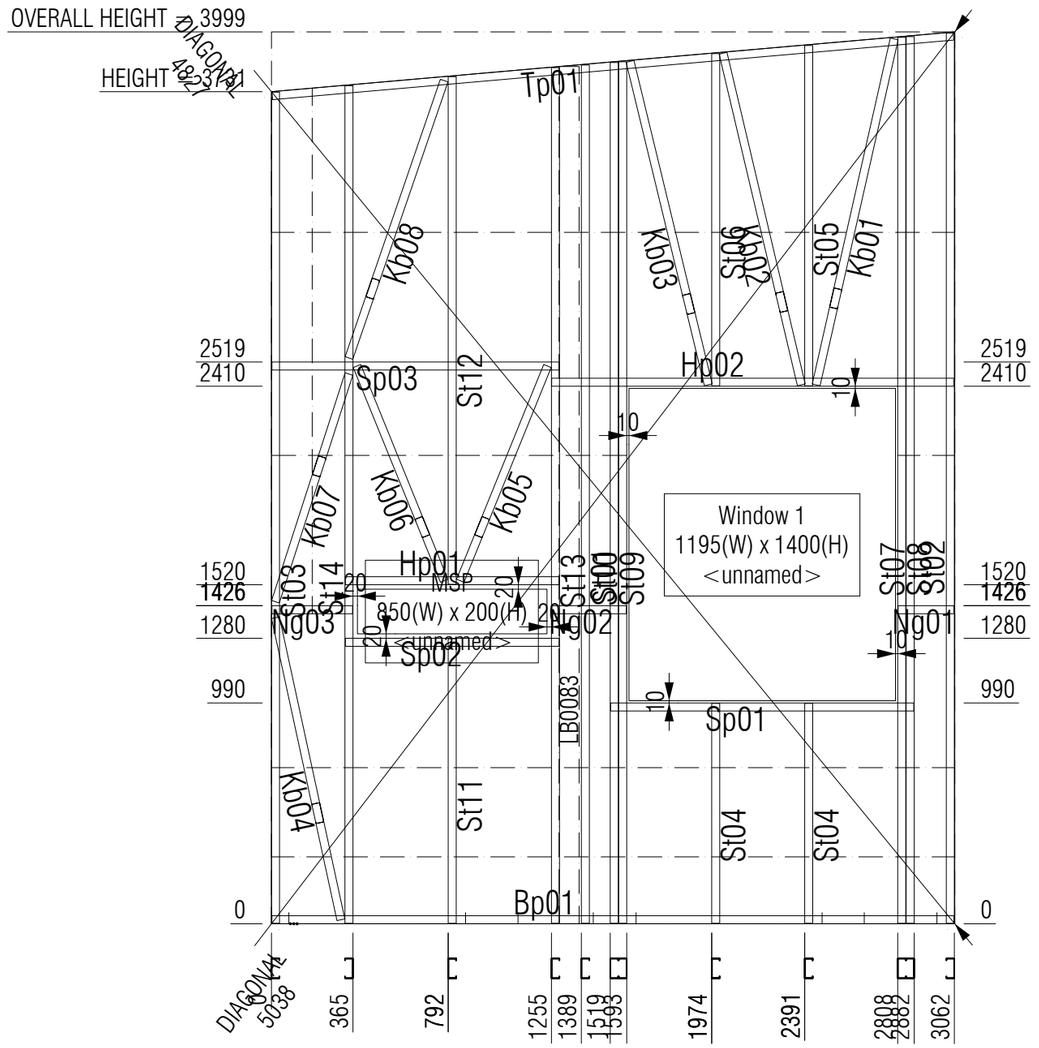

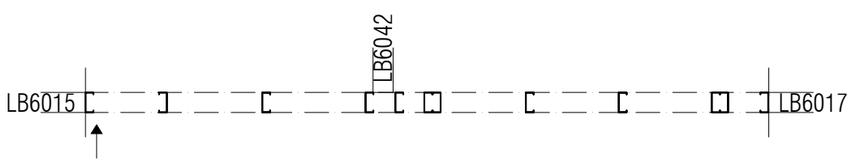

FRAME STICKS

NAME	LENGTH	WT	QTY	PROFILE
Tp01	3066	3.9	1	89S36-950-500
Bp01	3058	3.9	1	89S36-950-500
St01	3848	4.9	1	89S36-950-500
St02	3991	5.1	1	89S36-950-500
St03	3727	4.8	1	89S36-950-500
St04	986	1.3	2	89S36-950-500
St05	1526	2.0	1	89S36-950-500
St06	1489	1.9	1	89S36-950-500
St07	3976	5.1	1	89S36-950-500
St08	3972	5.1	1	89S36-950-500
St09	3859	4.9	1	89S36-950-500
St10	3863	4.9	1	89S36-950-500
St11	1276	1.6	1	89S36-950-500
St12	2276	2.9	1	89S36-950-500
St13	3836	4.9	1	89S36-950-500
St14	3755	4.8	1	89S36-950-500
Ng01	250	0.3	1	89S36-950-500
Ng02	333	0.4	1	89S36-950-500
Ng03	361	0.5	1	89S36-950-500
Kb01	1590	2.0	1	89S36-950-500
Kb02	1528	2.0	1	89S36-950-500
Kb03	1492	1.9	1	89S36-950-500
Kb04	1385	1.8	1	89S36-950-500
Kb05	1039	1.3	1	89S36-950-500
Kb06	1039	1.3	1	89S36-950-500
Kb07	1073	1.4	1	89S36-950-500
Kb08	1315	1.7	1	89S36-950-500
Hp01	958	1.2	1	89S36-950-500
Hp02	1803	2.3	1	89S36-950-500
Sp01	1359	1.7	1	89S36-950-500
Sp02	958	1.2	1	89S36-950-500
Sp03	1287	1.6	1	89S36-950-500
TOTAL	67264	86.1	33	


LB6016

AUSTRUSS
www.austruss.com.au (02) 4860 1400
DWG FILE: ####

DRAWN Mitchell.H Ph:02 4860 1426

ISSUE	DATE	DESCRIPTION OF REVISION
0	05/03/26	IFA
A	03/05/26	IFC
B	06/05/26	IFC
C	08/05/26	IFC
D	11/05/26	IFC

Client/Company Name: Taylor
Project Name: Blayney
Building / Zone / Area: Zone 6
Job Number: 23314
Project Address: 3 Osman st, Blayney NSW 2799
Drawing Name: 90mm LB Wall production
Drawing Number: LGS-6-201
Revision: D
NOTE: USE PROVIDED DIMENSIONS ONLY. IF NOT PROVIDED, ASK.
Scale: NTS

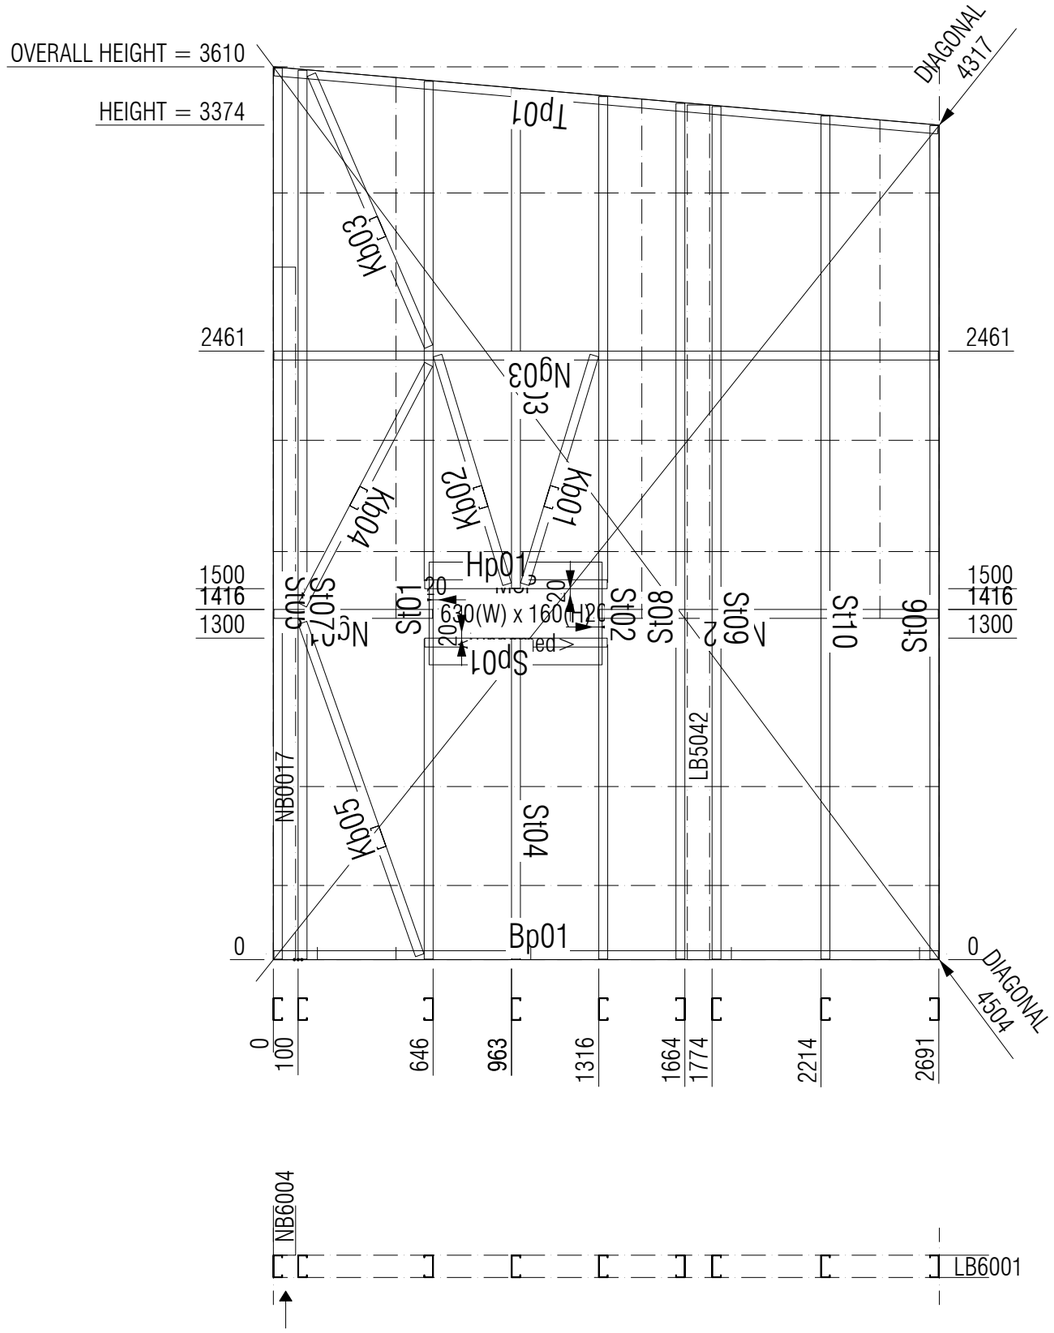

FRAME STICKS

NAME	LENGTH	WT	QTY	PROFILE
Tp01	2694	3.4	1	89S36-950-500
Bp01	2687	3.4	1	89S36-950-500
St01	3549	4.5	1	89S36-950-500
St02	3488	4.5	1	89S36-950-500
St03	2018	2.6	1	89S36-950-500
St04	1296	1.7	1	89S36-950-500
St05	3603	4.6	1	89S36-950-500
St06	3370	4.3	1	89S36-950-500
St07	3594	4.6	1	89S36-950-500
St08	3460	4.4	1	89S36-950-500
St09	3448	4.4	1	89S36-950-500
St10	3409	4.4	1	89S36-950-500
Ng01	642	0.8	1	89S36-950-500
Ng02	1371	1.8	1	89S36-950-500
Ng03	2687	3.4	1	89S36-950-500
Kb01	966	1.2	1	89S36-950-500
Kb02	966	1.2	1	89S36-950-500
Kb03	1198	1.5	1	89S36-950-500
Kb04	1098	1.4	1	89S36-950-500
Kb05	1425	1.8	1	89S36-950-500
Hp01	738	0.9	1	89S36-950-500
Sp01	738	0.9	1	89S36-950-500
TOTAL	48446	62.0	22	


LB6000

AUSTRUSS
www.austruss.com.au (02) 4860 1400
DWG FILE: ####

DRAWN Mitchell.H Ph:02 4860 1426

ISSUE	DATE	DESCRIPTION OF REVISION
0	05/03/26	IFA
A	03/05/26	IFC
B	06/05/26	IFC
C	08/05/26	IFC
D	11/05/26	IFC

Client/Company Name: Taylor
Project Name: Blayney
Building / Zone / Area: Zone 6
Job Number: 23314
Project Address: 3 Osman st, Blayney NSW 2799
Drawing Name: 90mm LB Wall production
Drawing Number: LGS-6-201
Revision: D
NOTE: USE PROVIDED DIMENSIONS ONLY. IF NOT PROVIDED, ASK.
Scale: NTS

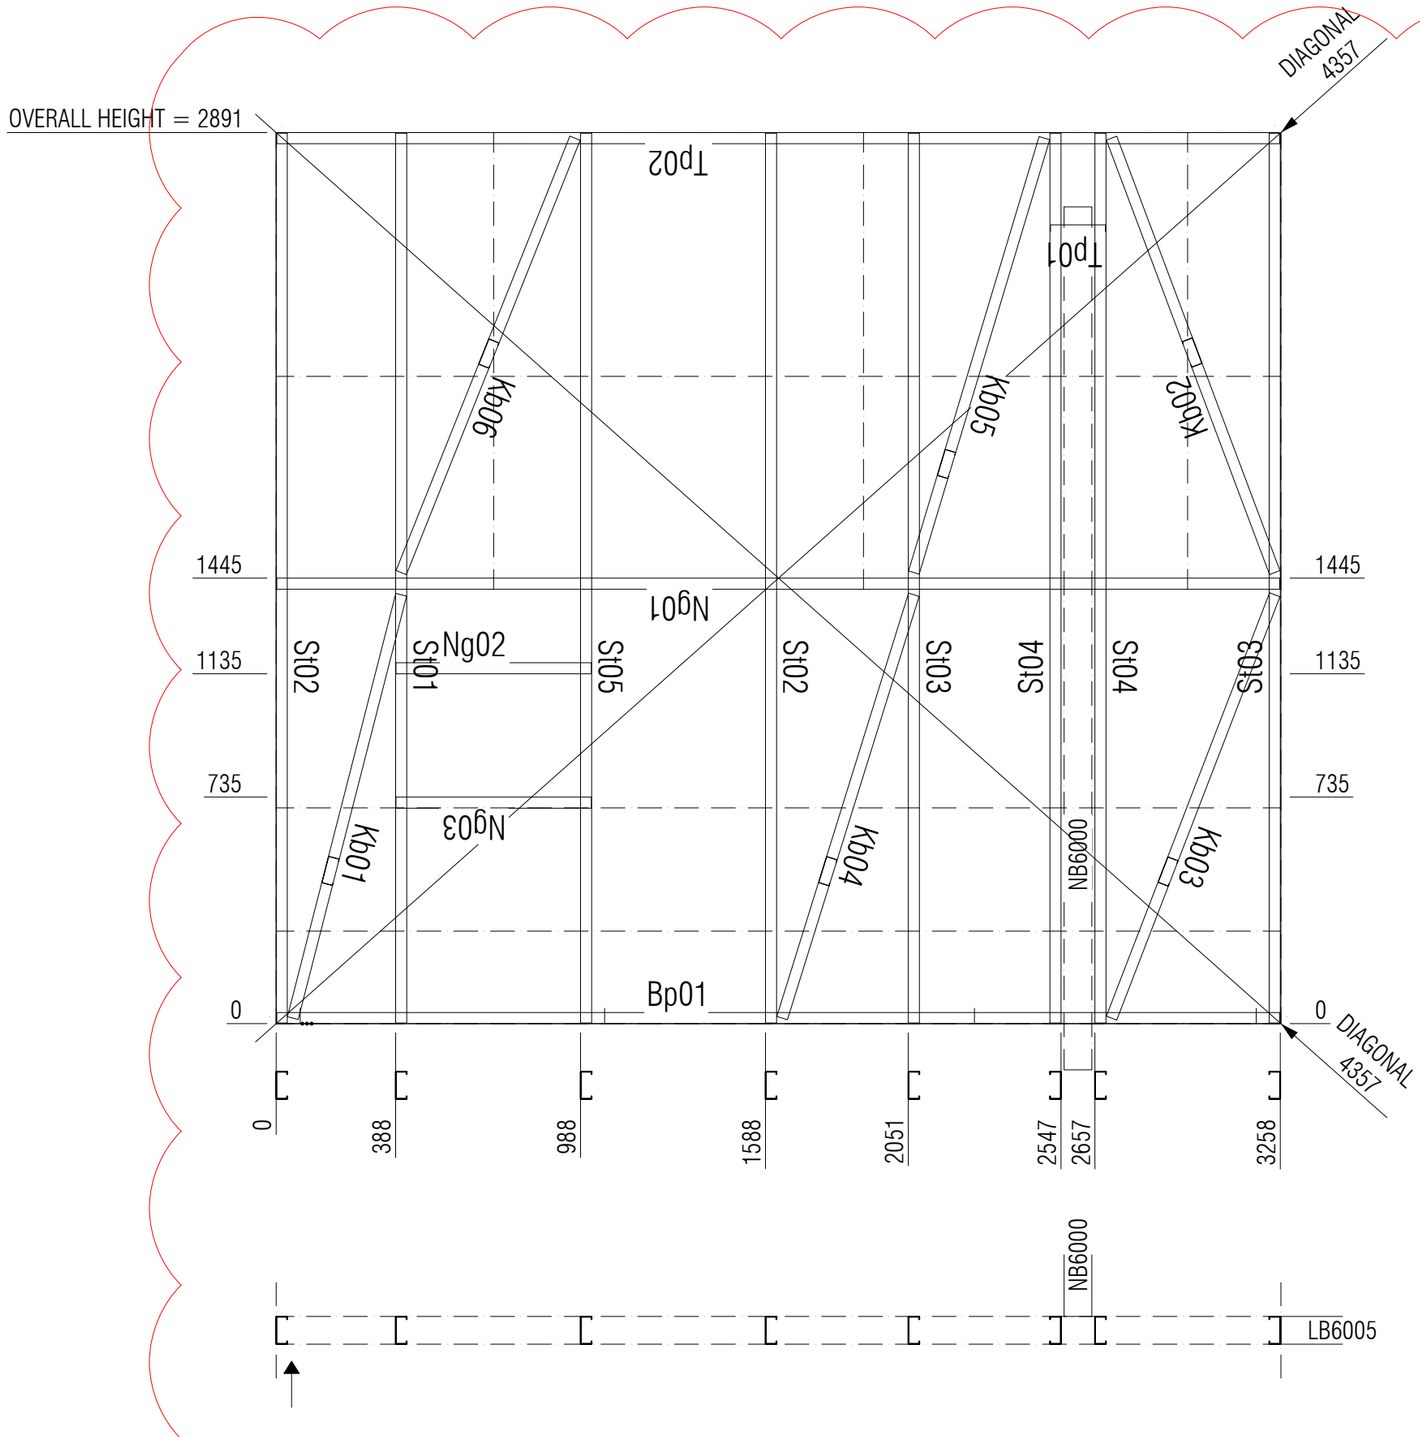

FRAME STICKS

NAME	LENGTH	WT	QTY	PROFILE
Tp01	178	0.2	1	89S36-950-500
Tp02	3254	4.2	1	89S36-950-500
Bp01	3254	4.2	1	89S36-950-500
St01	2887	3.7	1	89S36-950-500
St02	2887	3.7	2	89S36-950-500
St03	2887	3.7	2	89S36-950-500
St04	2887	3.7	2	89S36-950-500
St05	2887	3.7	1	89S36-950-500
Ng01	3254	4.2	1	89S36-950-500
Ng02	634	0.8	1	89S36-950-500
Ng03	634	0.8	1	89S36-950-500
Kb01	1418	1.8	1	89S36-950-500
Kb02	1506	1.9	1	89S36-950-500
Kb03	1472	1.9	1	89S36-950-500
Kb04	1438	1.8	1	89S36-950-500
Kb05	1472	1.9	1	89S36-950-500
Kb06	1518	1.9	1	89S36-950-500
TOTAL	43127	55.2	20	


LB6004

AUSTRUSS
www.austruss.com.au (02) 4860 1400
DWG FILE: ####

DRAWN Mitchell.H
Ph:02 4860 1426

ISSUE	DATE	DESCRIPTION OF REVISION
0	05/03/26	IFA
A	03/05/26	IFC
B	06/05/26	IFC
C	08/05/26	IFC
D	11/05/26	IFC

Client/Company Name: Taylor
Project Name: Blayney
Building / Zone / Area: Zone 6
Job Number: 23314
Project Address: 3 Osman st, Blayney NSW 2799
Drawing Name: 90mm LB Wall production
Drawing Number: LGS-6-201
Revision: D
NOTE: USE PROVIDED DIMENSIONS ONLY. IF NOT PROVIDED, ASK.
Scale: NTS

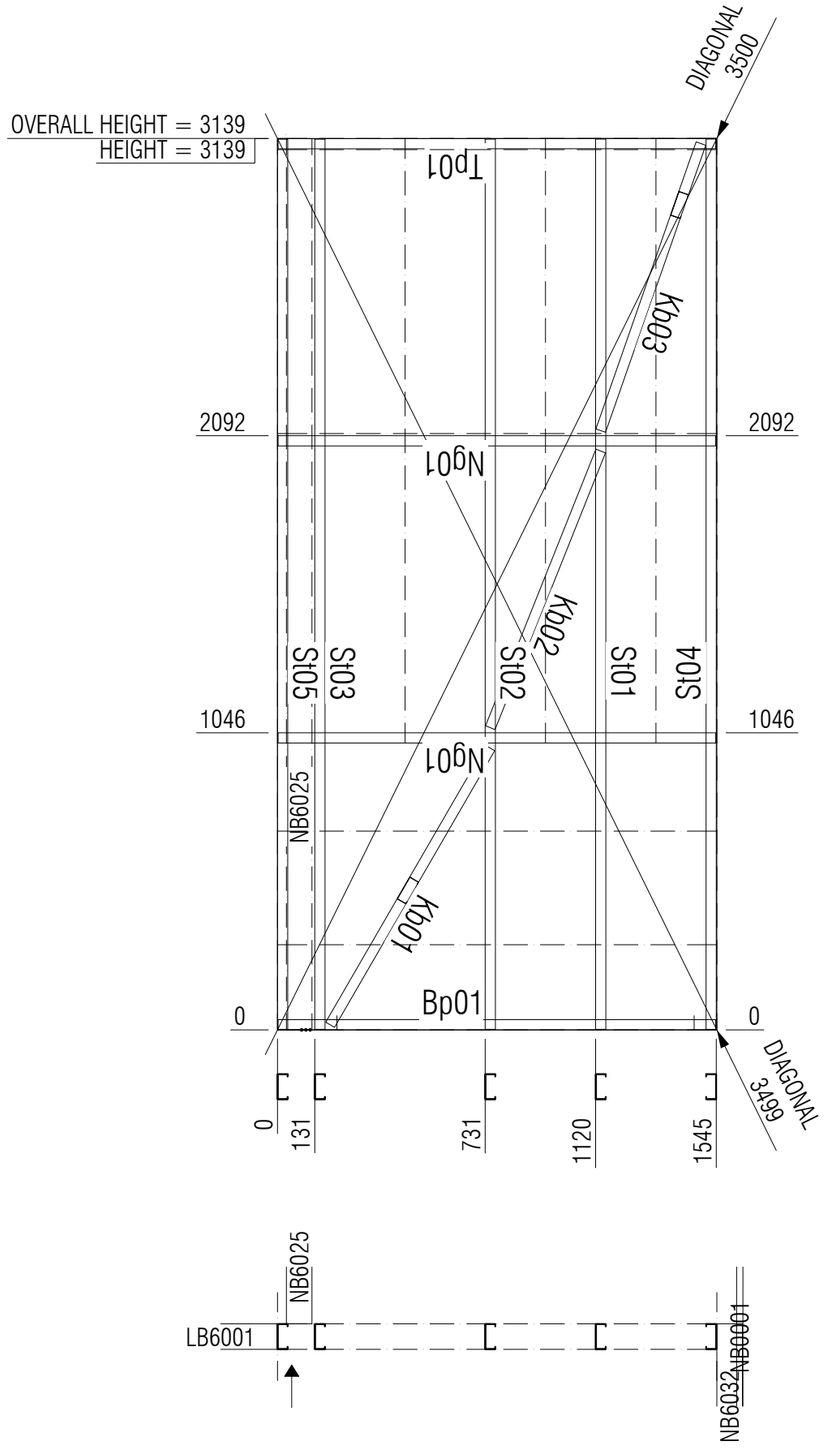

FRAME STICKS

NAME	LENGTH	WT	QTY	PROFILE
Tp01	1541	2.0	1	89S36-950-500
Bp01	1541	2.0	1	89S36-950-500
St01	3135	4.0	1	89S36-950-500
St02	3135	4.0	1	89S36-950-500
St03	3135	4.0	1	89S36-950-500
St04	3135	4.0	1	89S36-950-500
St05	3135	4.0	1	89S36-950-500
Ng01	1541	2.0	2	89S36-950-500
Kb01	1126	1.4	1	89S36-950-500
Kb02	1049	1.3	1	89S36-950-500
Kb03	1071	1.4	1	89S36-950-500
TOTAL	25085	32.1	12	

LB6003


AUSTRUSS
www.austruss.com.au (02) 4860 1400
DWG FILE: ####

DRAWN Mitchell.H Ph:02 4860 1426

ISSUE	DATE	DESCRIPTION OF REVISION
0	05/03/26	IFA
A	03/05/26	IFC
B	06/05/26	IFC
C	08/05/26	IFC
D	11/05/26	IFC

Client/Company Name: Taylor
Project Name: Blayney
Building / Zone / Area: Zone 6
Job Number: 23314
Project Address: 3 Osman st, Blayney NSW 2799
Drawing Name: 90mm LB Wall production
Drawing Number: LGS-6-201
Revision: D
NOTE: USE PROVIDED DIMENSIONS ONLY. IF NOT PROVIDED, ASK.
Scale: NTS

DOUBLE SCREW

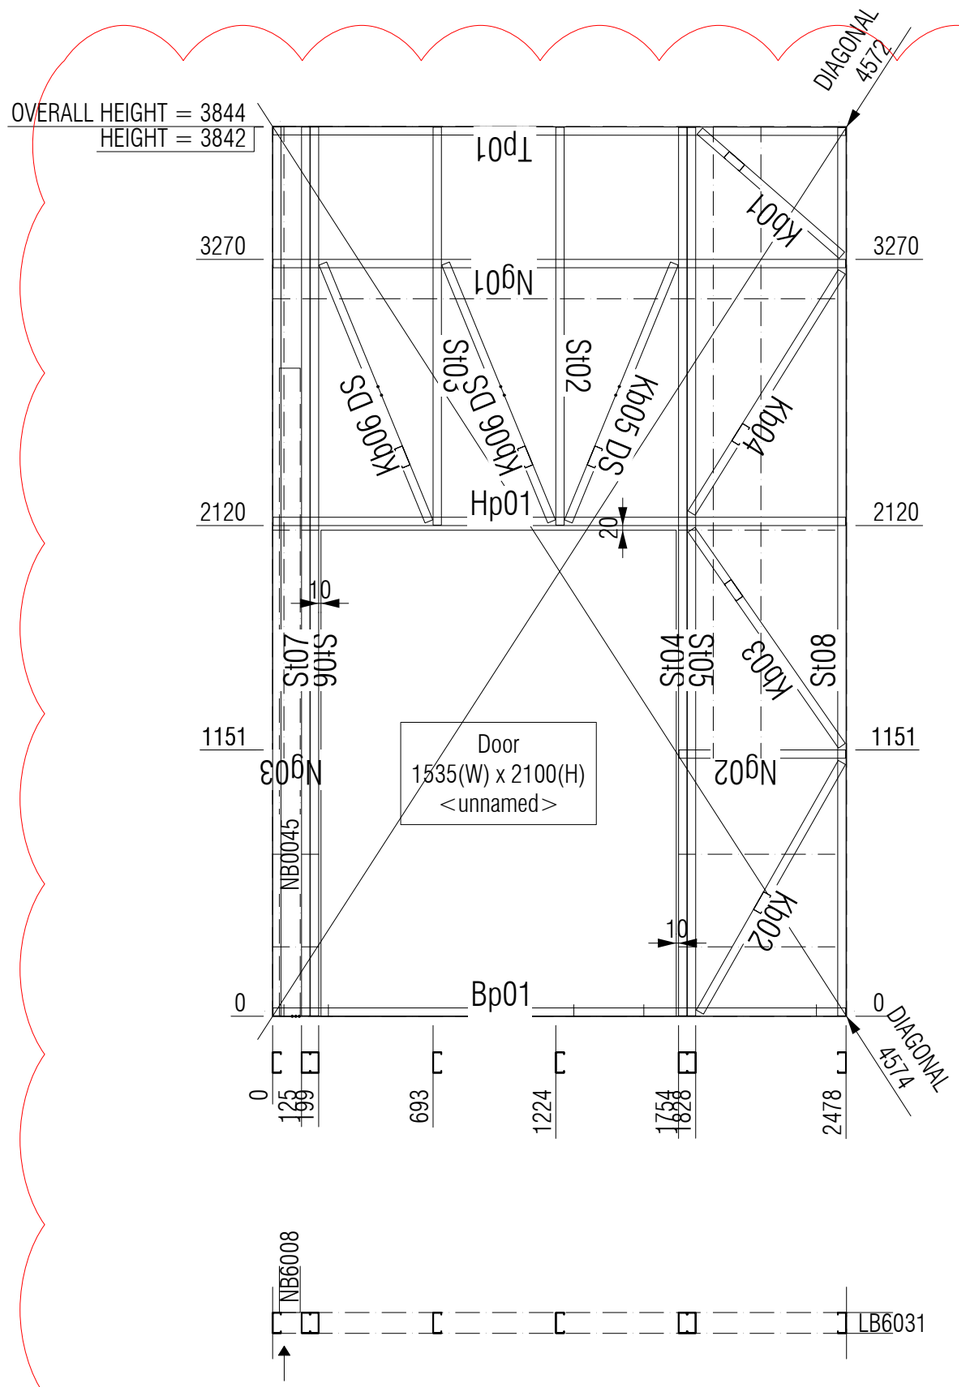

FRAME STICKS

NAME	LENGTH	WT	QTY	PROFILE
Tp01	2474	3.2	1	89S36-950-500
Bp01	2474	3.2	1	89S36-950-500
St01	3840	4.9	1	89S36-950-500
St02	1719	2.2	1	89S36-950-500
St03	1719	2.2	1	89S36-950-500
St04	3838	4.9	1	89S36-950-500
St05	3838	4.9	1	89S36-950-500
St06	3840	4.9	1	89S36-950-500
St07	3840	4.9	1	89S36-950-500
St08	3838	4.9	1	89S36-950-500
Ng01	2474	3.2	1	89S36-950-500
Ng02	720	0.9	1	89S36-950-500
Ng03	195	0.2	1	89S36-950-500
Kb01	815	1.0	1	89S36-950-500
Kb02	1241	1.6	1	89S36-950-500
Kb03	1137	1.5	1	89S36-950-500
Kb04	1228	1.6	1	89S36-950-500
Kb05 DS	1205	1.5	1	89S36-950-500
Kb06 DS	1205	1.5	2	89S36-950-500
Hp01	2474	3.2	1	89S36-950-500
TOTAL	45315	58.0	21	

LB6030


AUSTRUSS
www.austruss.com.au (02) 4860 1400

DWG FILE: ####

DRAWN Mitchell.H Ph:02 4860 1426

ISSUE	DATE	DESCRIPTION OF REVISION
0	05/03/26	IFA
A	03/05/26	IFC
B	06/05/26	IFC
C	08/05/26	IFC
D	11/05/26	IFC

Client/Company Name: Taylor
Project Name: Blayney
Building / Zone / Area: Zone 6
Job Number: 23314
Project Address: 3 Osman st, Blayney NSW 2799
Drawing Name: 90mm LB Wall production
Drawing Number: LGS-6-201
Revision: D
NOTE: USE PROVIDED DIMENSIONS ONLY. IF NOT PROVIDED, ASK.
Scale: NTS

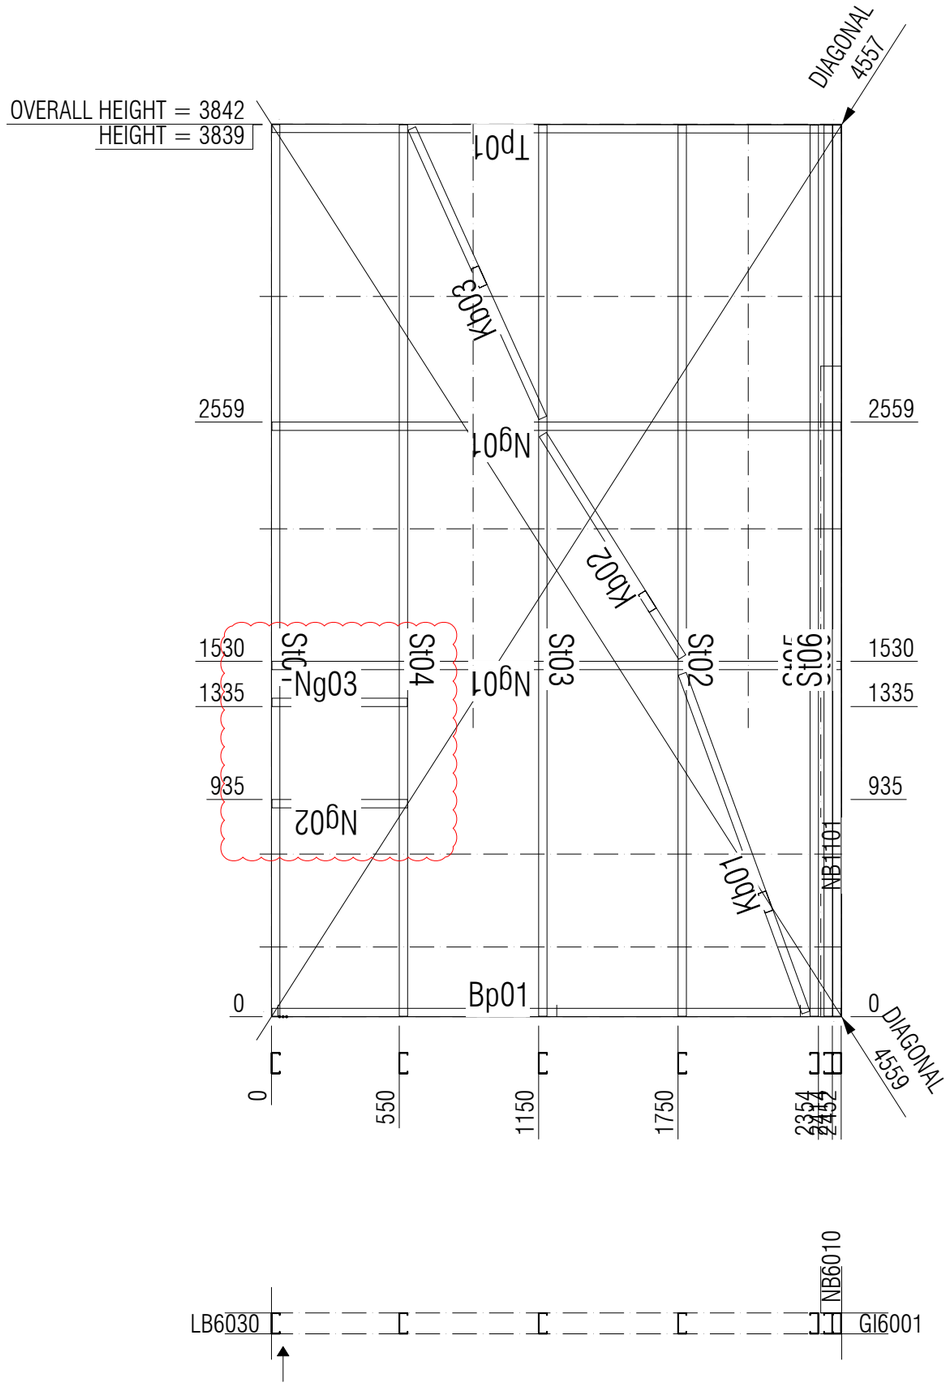

FRAME STICKS

NAME	LENGTH	WT	QTY	PROFILE
Tp01	2448	3.1	1	89S36-950-500
Bp01	2448	3.1	1	89S36-950-500
St01	3838	4.9	1	89S36-950-500
St02	3836	4.9	1	89S36-950-500
St03	3836	4.9	1	89S36-950-500
St04	3837	4.9	1	89S36-950-500
St05	3835	4.9	1	89S36-950-500
St06	3835	4.9	2	89S36-950-500
Ng01	2448	3.1	2	89S36-950-500
Ng02	584	0.7	1	89S36-950-500
Ng03	583	0.7	1	89S36-950-500
Kb01	1552	2.0	1	89S36-950-500
Kb02	1130	1.4	1	89S36-950-500
Kb03	1367	1.8	1	89S36-950-500
TOTAL	41862	53.6	16	


LB6031

AUSTRUSS
www.austruss.com.au (02) 4860 1400
DWG FILE: ####

DRAWN Mitchell.H
Ph:02 4860 1426

ISSUE	DATE	DESCRIPTION OF REVISION
0	05/03/26	IFA
A	03/05/26	IFC
B	06/05/26	IFC
C	08/05/26	IFC
D	11/05/26	IFC

Client/Company Name: Taylor
Project Name: Blayney
Building / Zone / Area: Zone 6
Job Number: 23314
Project Address: 3 Osman st, Blayney NSW 2799
NOTE: USE PROVIDED DIMENSIONS ONLY. IF NOT PROVIDED, ASK.
Scale: NTS
Drawing Name: 90mm LB Wall production
Drawing Number: LGS-6-201
Revision: D

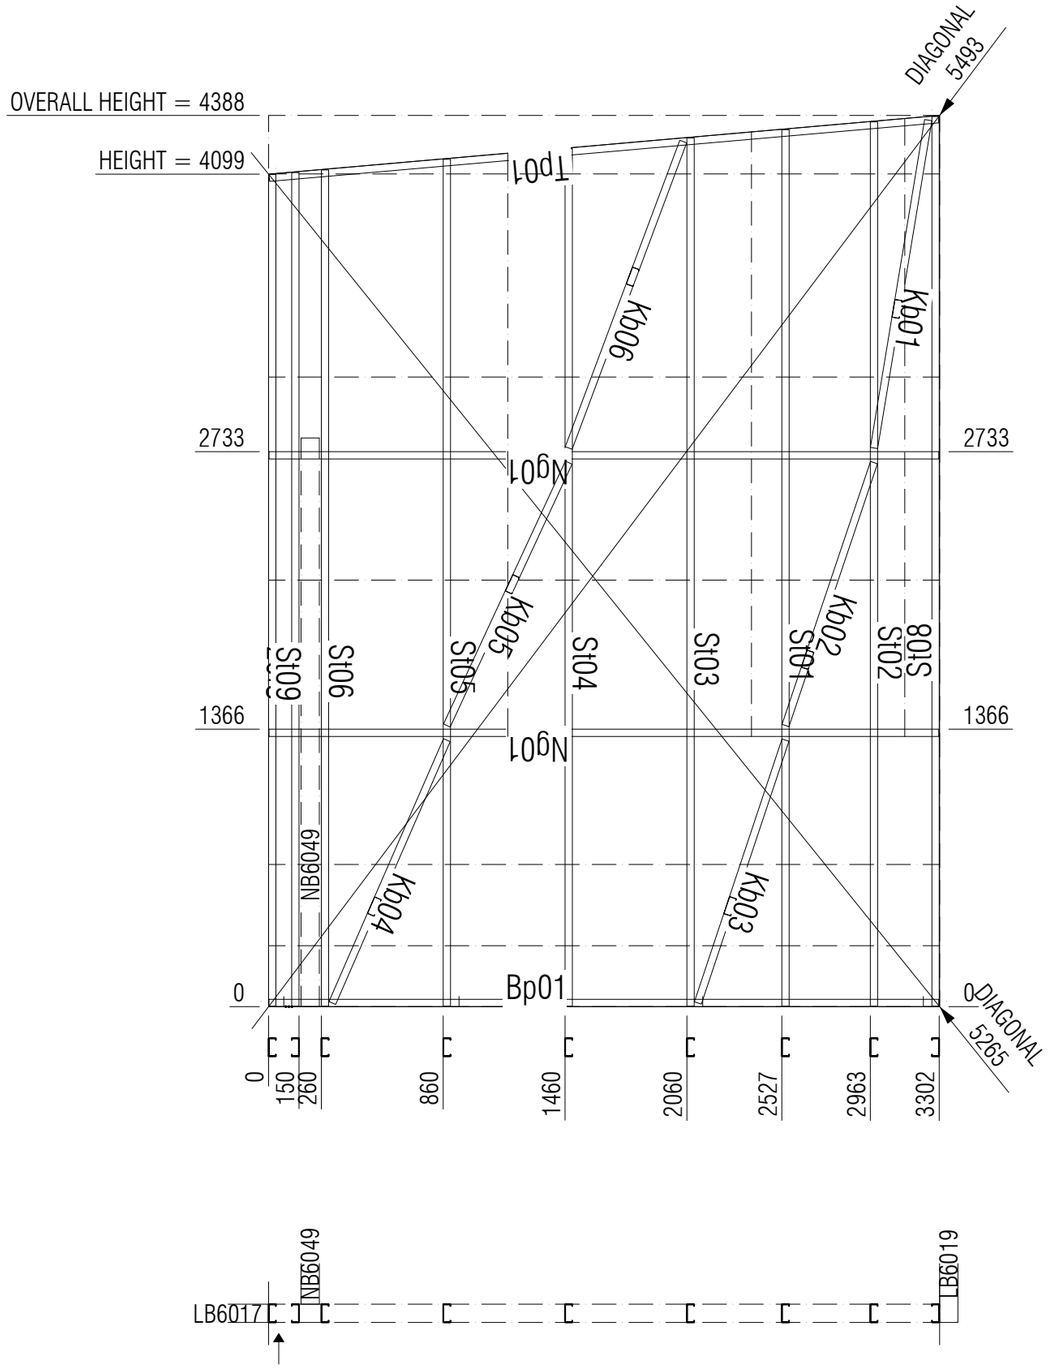

FRAME STICKS

NAME	LENGTH	WT	QTY	PROFILE
Tp01	3308	4.2	1	89S36-950-500
Bp01	3298	4.2	1	89S36-950-500
St01	4316	5.5	1	89S36-950-500
St02	4354	5.6	1	89S36-950-500
St03	4275	5.5	1	89S36-950-500
St04	4223	5.4	1	89S36-950-500
St05	4170	5.3	1	89S36-950-500
St06	4118	5.3	1	89S36-950-500
St07	4105	5.3	1	89S36-950-500
St08	4381	5.6	1	89S36-950-500
St09	4095	5.2	1	89S36-950-500
Ng01	3298	4.2	2	89S36-950-500
Kb01	1636	2.1	1	89S36-950-500
Kb02	1366	1.7	1	89S36-950-500
Kb03	1364	1.7	1	89S36-950-500
Kb04	1412	1.8	1	89S36-950-500
Kb05	1427	1.8	1	89S36-950-500
Kb06	1611	2.1	1	89S36-950-500
TOTAL	60053	76.9	19	

LB6018


AUSTRUSS
www.austruss.com.au (02) 4860 1400

DWG FILE: ####

DRAWN
Mitchell.H
Ph:02 4860 1426

ISSUE	DATE	DESCRIPTION OF REVISION
0	05/03/26	IFA
A	03/05/26	IFC
B	06/05/26	IFC
C	08/05/26	IFC
D	11/05/26	IFC

Client/Company Name: Taylor
Project Name: Blayney
Building / Zone / Area: Zone 6
Job Number: 23314
Project Address: 3 Osman st, Blayney NSW 2799
Drawing Name: 90mm LB Wall production
Drawing Number: LGS-6-201
Revision: D
NOTE: USE PROVIDED DIMENSIONS ONLY. IF NOT PROVIDED, ASK.
Scale: NTS

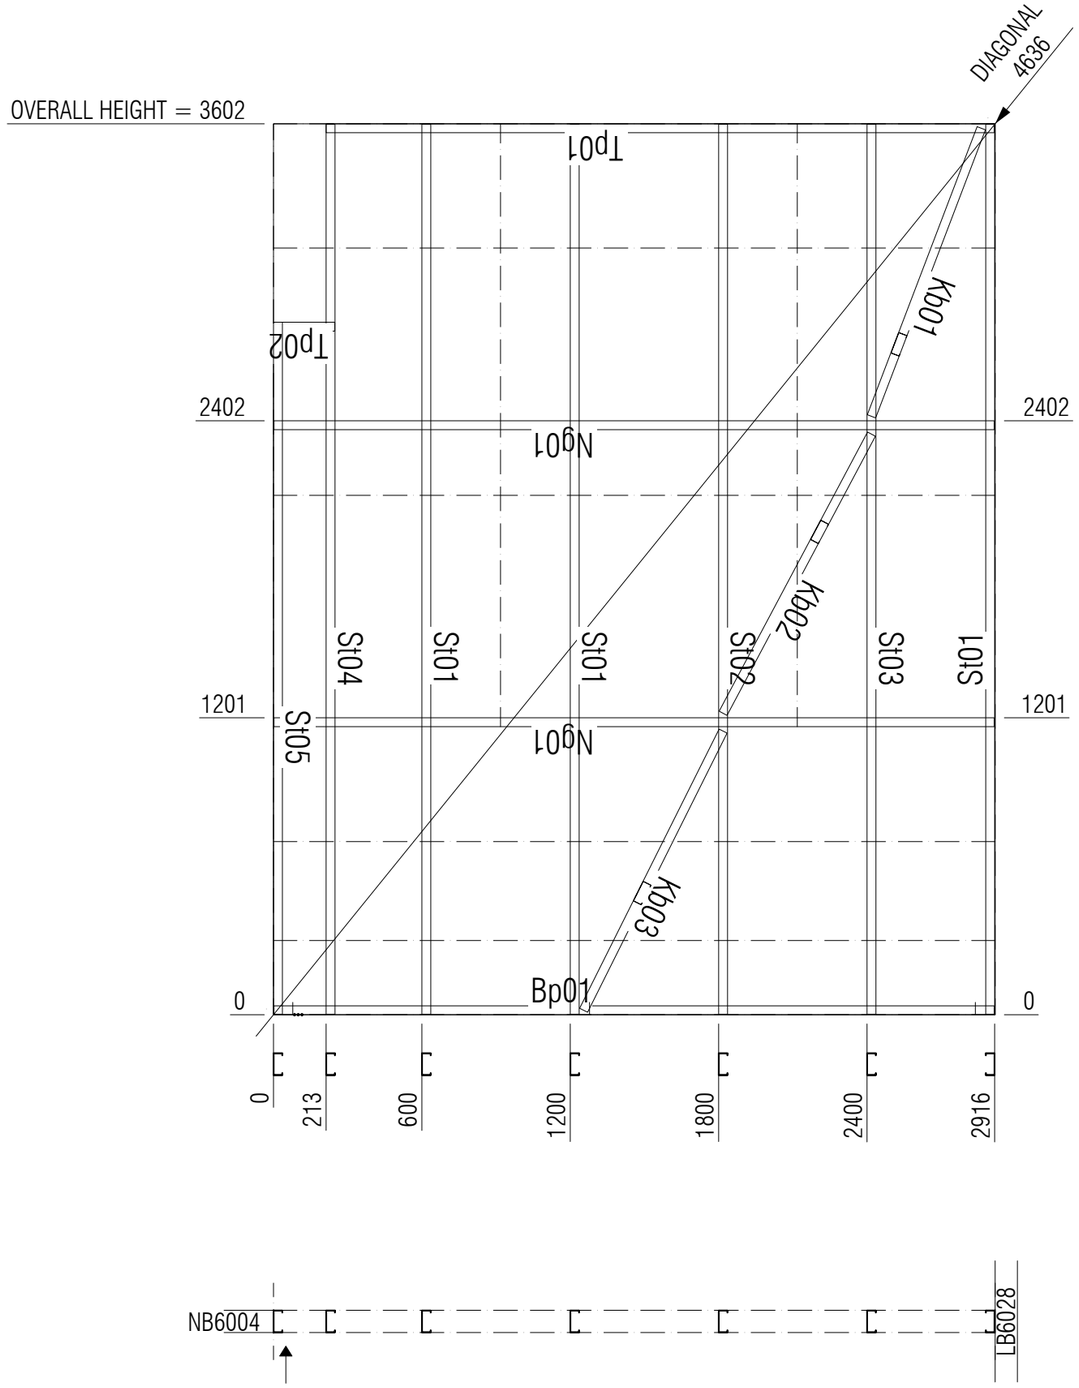

FRAME STICKS

NAME	LENGTH	WT	QTY	PROFILE
Tp01	2701	3.5	1	89S36-950-500
Tp02	246	0.3	1	89S36-950-500
Bp01	2912	3.7	1	89S36-950-500
St01	3598	4.6	3	89S36-950-500
St02	3598	4.6	1	89S36-950-500
St03	3598	4.6	1	89S36-950-500
St04	3598	4.6	1	89S36-950-500
St05	2798	3.6	1	89S36-950-500
Ng01	2912	3.7	2	89S36-950-500
Kb01	1247	1.6	1	89S36-950-500
Kb02	1278	1.6	1	89S36-950-500
Kb03	1262	1.6	1	89S36-950-500
TOTAL	39857	51.0	15	

LB6043


AUSTRUSS
www.austruss.com.au (02) 4860 1400

DWG FILE: ####

DRAWN Mitchell.H Ph:02 4860 1426

ISSUE	DATE	DESCRIPTION OF REVISION
0	05/03/26	IFA
A	03/05/26	IFC
B	06/05/26	IFC
C	08/05/26	IFC
D	11/05/26	IFC

Client/Company Name: Taylor
Project Name: Blayney
Building / Zone / Area: Zone 6
Job Number: 23314
Project Address: 3 Osman st, Blayney NSW 2799
Drawing Name: 90mm LB Wall production
Drawing Number: LGS-6-201
Revision: D
NOTE: USE PROVIDED DIMENSIONS ONLY. IF NOT PROVIDED, ASK.
Scale: NTS

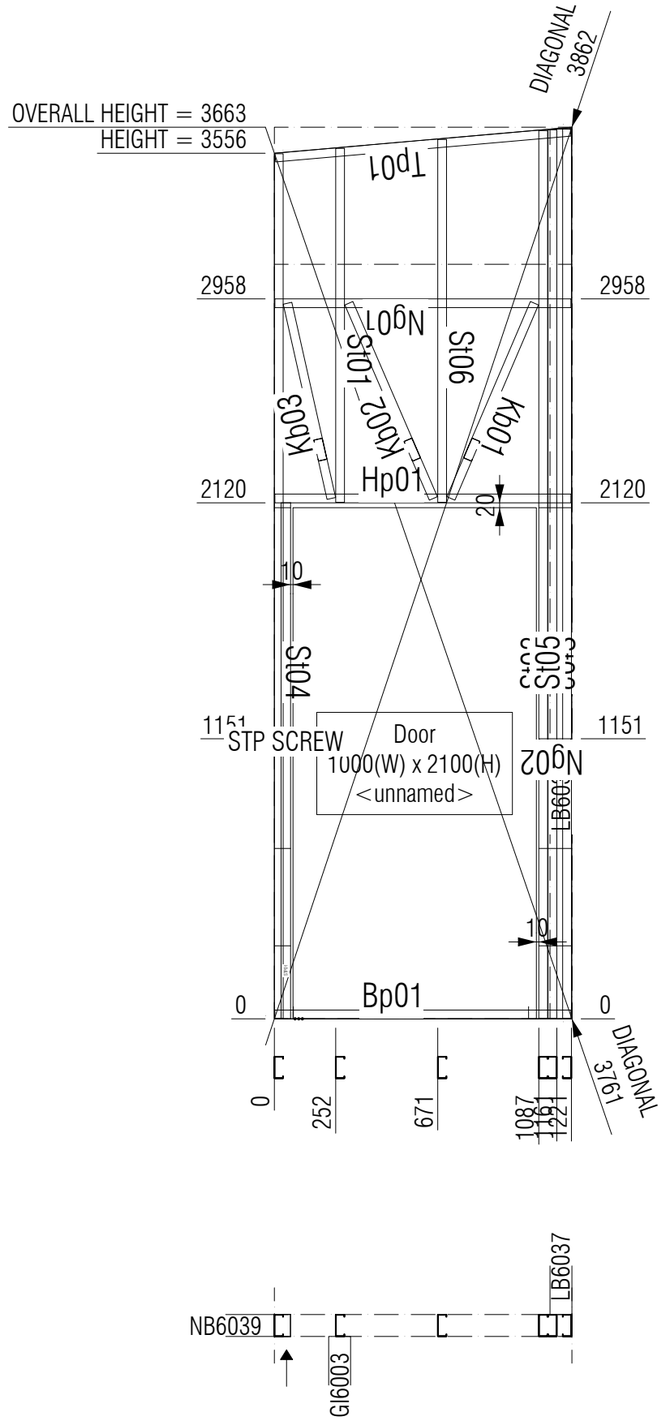

FRAME STICKS

NAME	LENGTH	WT	QTY	PROFILE
Tp01	1218	1.6	1	89S36-950-500
Bp01	1217	1.6	1	89S36-950-500
St01	1454	1.9	1	89S36-950-500
St02	3647	4.7	1	89S36-950-500
St03	3651	4.7	1	89S36-950-500
St04	3552	4.5	1	89S36-950-500
St05	3656	4.7	1	89S36-950-500
St06	1491	1.9	1	89S36-950-500
Ng01	1217	1.6	1	89S36-950-500
Ng02	130	0.2	1	89S36-950-500
Kb01	872	1.1	1	89S36-950-500
Kb02	874	1.1	1	89S36-950-500
Kb03	822	1.1	1	89S36-950-500
Hp01	1217	1.6	1	89S36-950-500
TOTAL	25017	32.0	14	

STEEL SUPPORT MEMBERS

NAME	PROFILE	LENGTH	WT	QTY
STP01	92U39_095_550	2120	2.7	1
TOTAL			2.7	1

LB6045


AUSTRUSS
www.austruss.com.au (02) 4860 1400

DRAWN Mitchell.H
Ph:02 4860 1426

DWG FILE: ####

ISSUE	DATE	DESCRIPTION OF REVISION
0	05/03/26	IFA
A	03/05/26	IFC
B	06/05/26	IFC
C	08/05/26	IFC
D	11/05/26	IFC

Client/Company Name: Taylor
Project Name: Blayney
Project Address: 3 Osman st, Blayney NSW 2799
NOTE: USE PROVIDED DIMENSIONS ONLY. IF NOT PROVIDED, ASK.
Scale: NTS
Building / Zone / Area: Zone 6
Job Number: 23314
Drawing Name: 90mm LB Wall production
Drawing Number: LGS-6-201
Revision: D

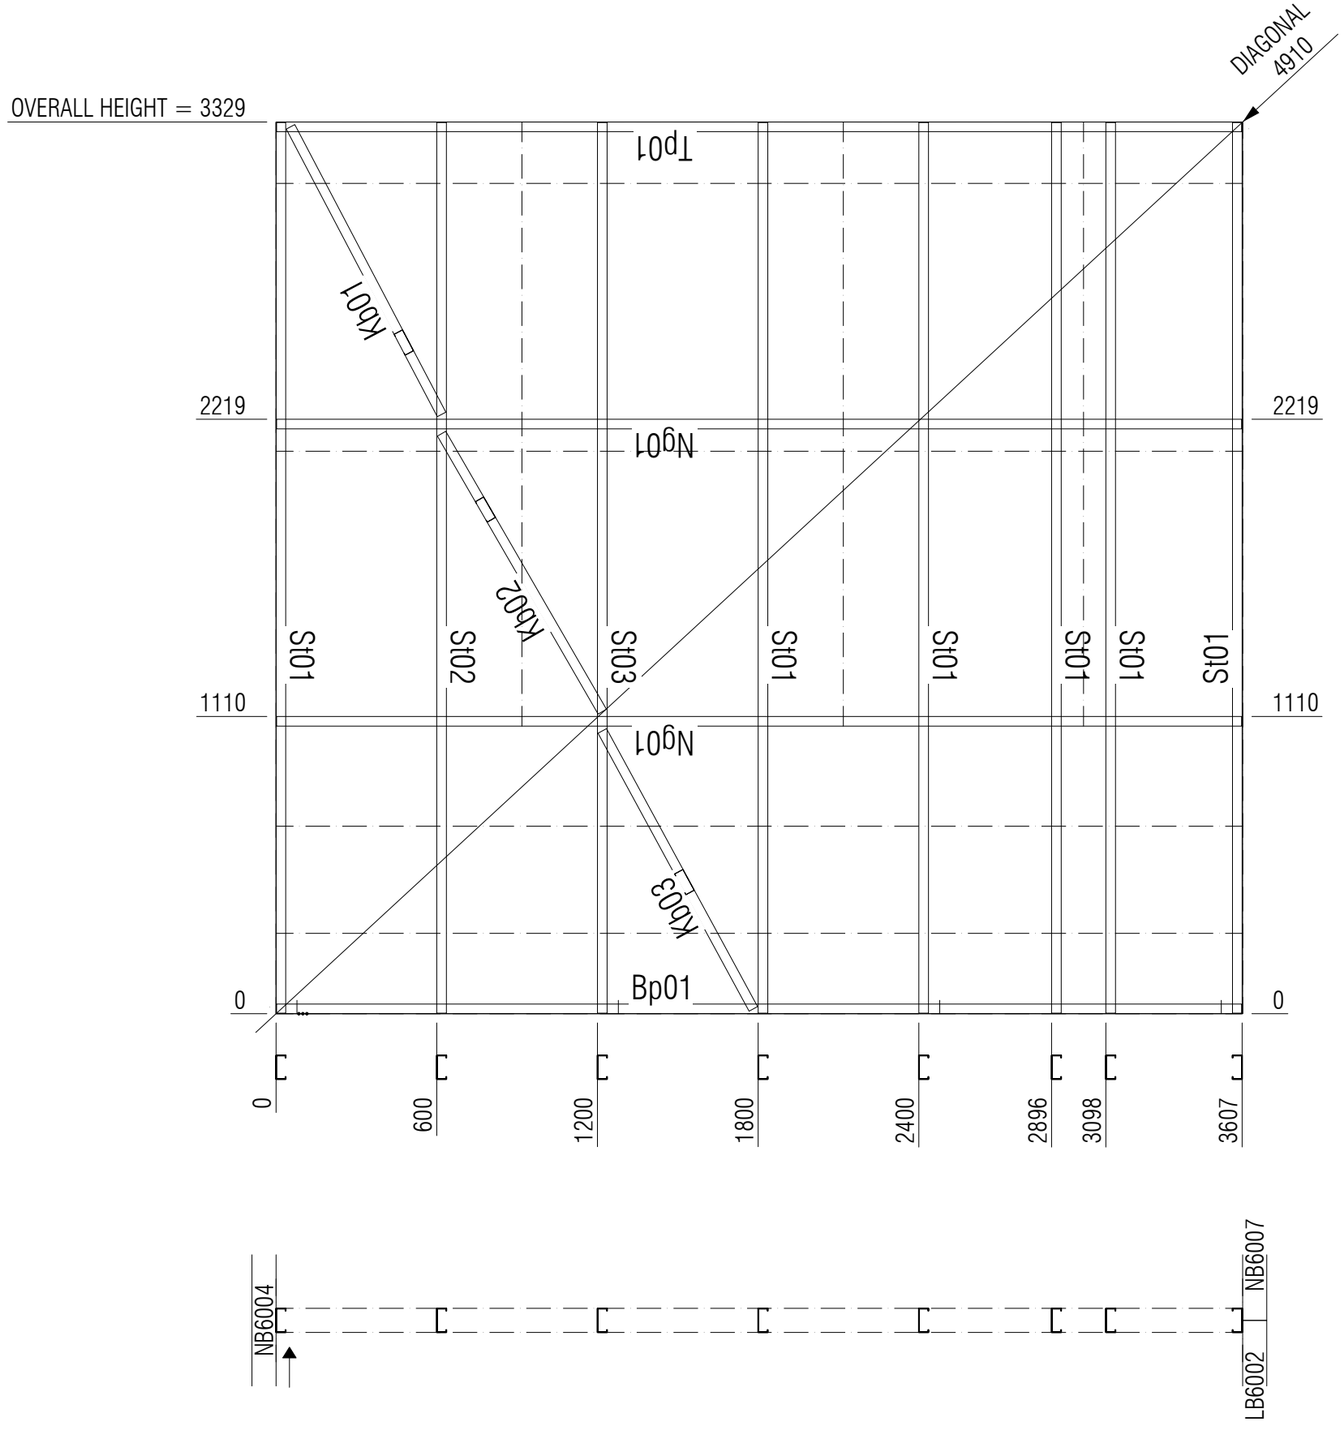

FRAME STICKS

NAME	LENGTH	WT	QTY	PROFILE
Tp01	3603	4.6	1	89S36-950-500
Bp01	3603	4.6	1	89S36-950-500
St01	3325	4.3	6	89S36-950-500
St02	3325	4.3	1	89S36-950-500
St03	3325	4.3	1	89S36-950-500
Ng01	3603	4.6	2	89S36-950-500
Kb01	1213	1.6	1	89S36-950-500
Kb02	1199	1.5	1	89S36-950-500
Kb03	1181	1.5	1	89S36-950-500
TOTAL	44606	57.1	15	

LB6044

AUSTRUSS
www.austruss.com.au (02) 4860 1400
DWG FILE: ####


DRAWN Mitchell.H
Ph:02 4860 1426

ISSUE	DATE	DESCRIPTION OF REVISION
0	05/03/26	IFA
A	03/05/26	IFC
B	06/05/26	IFC
C	08/05/26	IFC
D	11/05/26	IFC

Client/Company Name: Taylor
Project Name: Blayney
Project Address: 3 Osman st, Blayney NSW 2799
NOTE: USE PROVIDED DIMENSIONS ONLY. IF NOT PROVIDED, ASK.
Scale: NTS
Building / Zone / Area: Zone 6
Job Number: 23314
Drawing Name: 90mm LB Wall production
Drawing Number: LGS-6-201
Revision: D

DOUBLE SCREW

STP

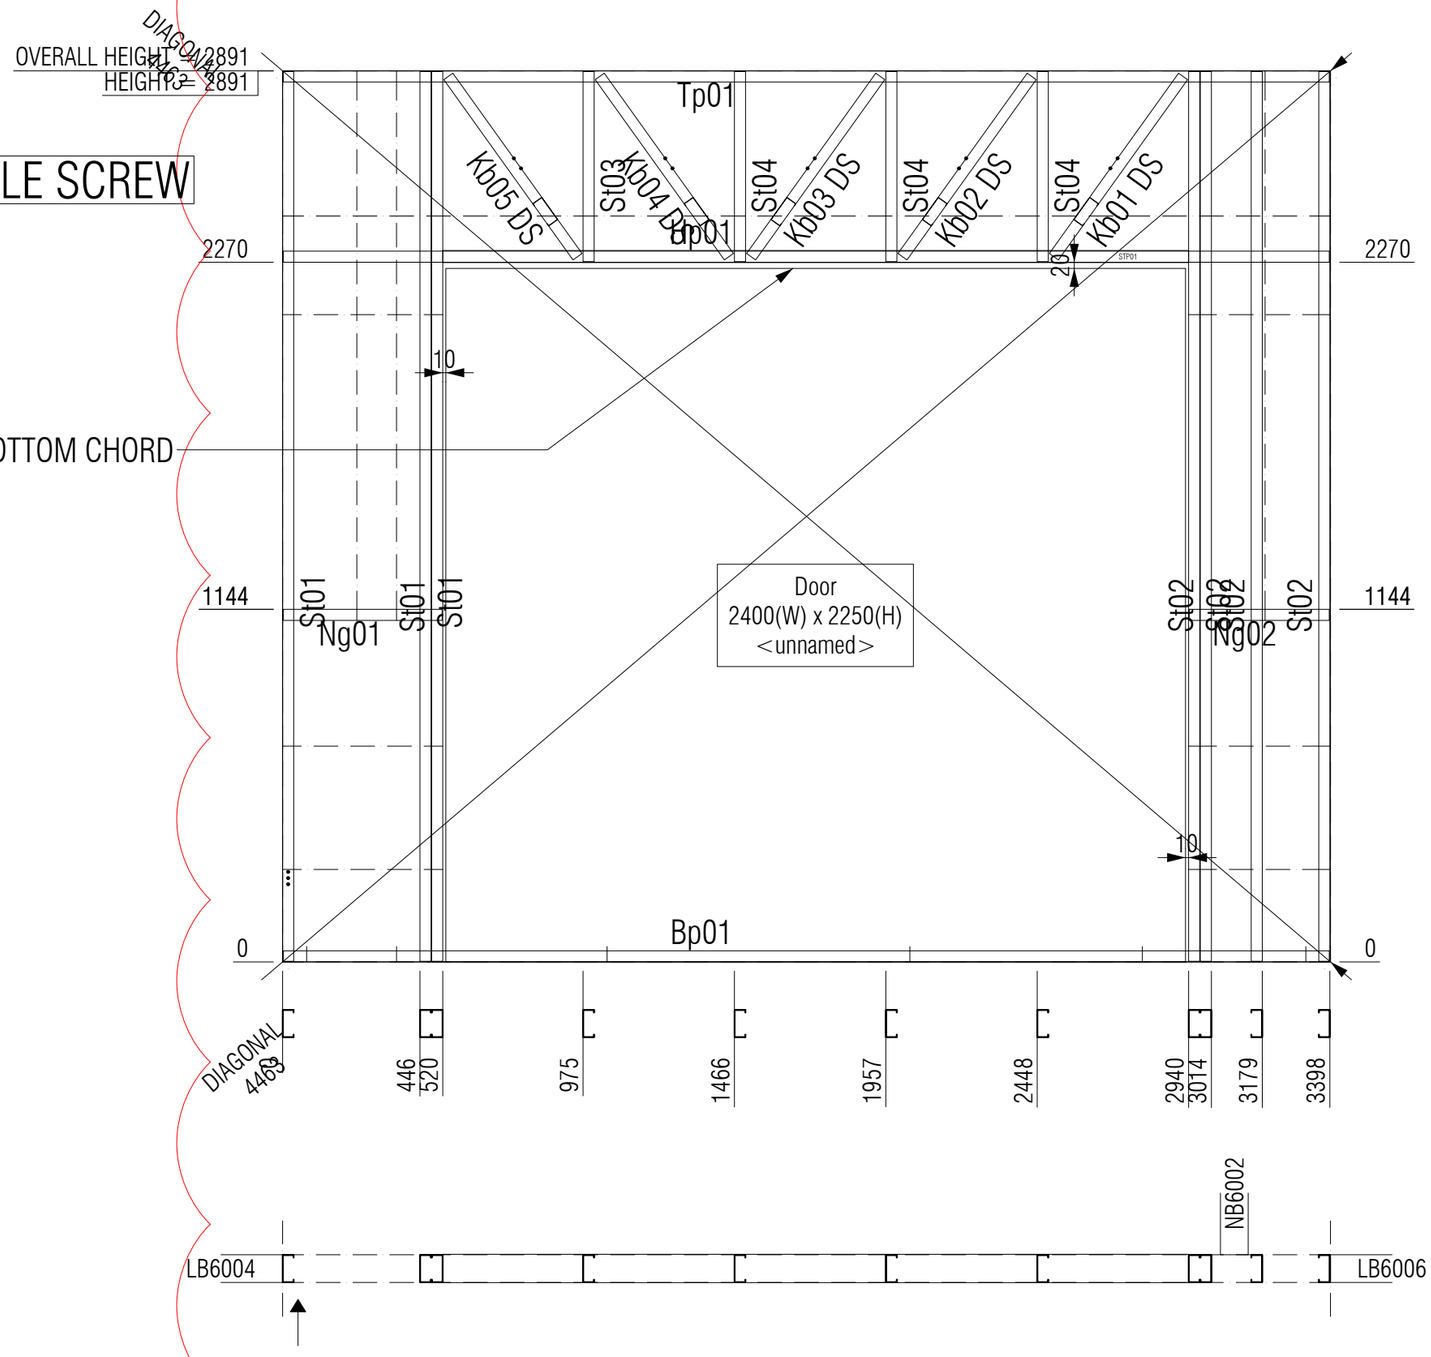

FRAME STICKS

NAME	LENGTH	WT	QTY	PROFILE
Tp01	3394	4.3	1	89S36-950-500
Bp01	3394	4.3	1	89S36-950-500
St01	2887	3.7	3	89S36-950-500
St02	2887	3.7	4	89S36-950-500
St03	617	0.8	1	89S36-950-500
St04	617	0.8	3	89S36-950-500
Ng01	516	0.7	1	89S36-950-500
Ng02	454	0.6	1	89S36-950-500
Kb01 DS	720	0.9	1	89S36-950-500
Kb02 DS	720	0.9	1	89S36-950-500
Kb03 DS	720	0.9	1	89S36-950-500
Kb04 DS	720	0.9	1	89S36-950-500
Kb05 DS	720	0.9	1	89S36-950-500
Hp01	3394	4.3	1	89S36-950-500
TOTAL	37425	47.9	21	

STEEL SUPPORT MEMBERS

NAME	PROFILE	LENGTH	WT	QTY
STP01	92U39_095_550	2420	3.1	1
TOTAL			3.1	1

LB6005


AUSTRUSS
www.austruss.com.au (02) 4860 1400

DRAWN Mitchell.H Ph:02 4860 1426

ISSUE	DATE	DESCRIPTION OF REVISION
0	05/03/26	IFA
A	03/05/26	IFC
B	06/05/26	IFC
C	08/05/26	IFC
D	11/05/26	IFC

DWG FILE: ####

Client/Company Name: Taylor
Project Name: Blayney
Building / Zone / Area: Zone 6
Job Number: 23314
Project Address: 3 Osman st, Blayney NSW 2799
Drawing Name: 90mm LB Wall production
Drawing Number: LGS-6-201
Revision: D
NOTE: USE PROVIDED DIMENSIONS ONLY. IF NOT PROVIDED, ASK.
Scale: NTS

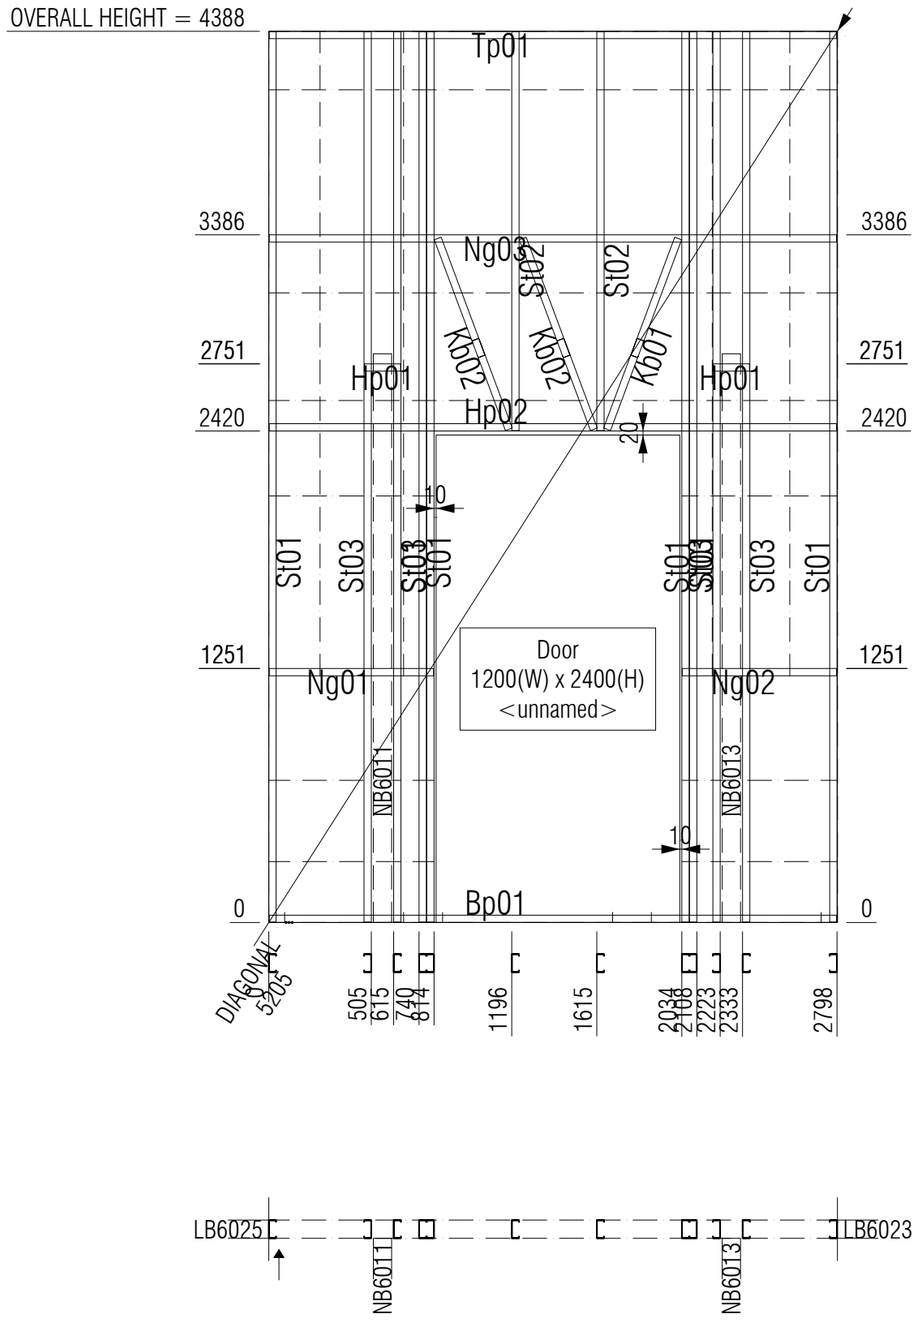

FRAME STICKS

NAME	LENGTH	WT	QTY	PROFILE
Tp01	2794	3.6	1	89S36-950-500
Bp01	2794	3.6	1	89S36-950-500
St01	4384	5.6	6	89S36-950-500
St02	1964	2.5	2	89S36-950-500
St03	4384	5.6	4	89S36-950-500
Ng01	810	1.0	1	89S36-950-500
Ng02	760	1.0	1	89S36-950-500
Ng03	2794	3.6	1	89S36-950-500
Kb01	1003	1.3	1	89S36-950-500
Kb02	1003	1.3	2	89S36-950-500
Hp01	178	0.2	2	89S36-950-500
Hp02	2794	3.6	1	89S36-950-500
TOTAL	63878	81.8	23	

LB6024


AUSTRUSS
www.austruss.com.au (02) 4860 1400

DRAWN Mitchell.H Ph:02 4860 1426

DWG FILE: ####

ISSUE	DATE	DESCRIPTION OF REVISION
0	05/03/26	IFA
A	03/05/26	IFC
B	06/05/26	IFC
C	08/05/26	IFC
D	11/05/26	IFC

Client/Company Name: Taylor
Project Name: Blayney
Building / Zone / Area: Zone 6
Job Number: 23314
Project Address: 3 Osman st, Blayney NSW 2799
Drawing Name: 90mm LB Wall production
Drawing Number: LGS-6-201
Revision: D
NOTE: USE PROVIDED DIMENSIONS ONLY. IF NOT PROVIDED, ASK.
Scale: NTS

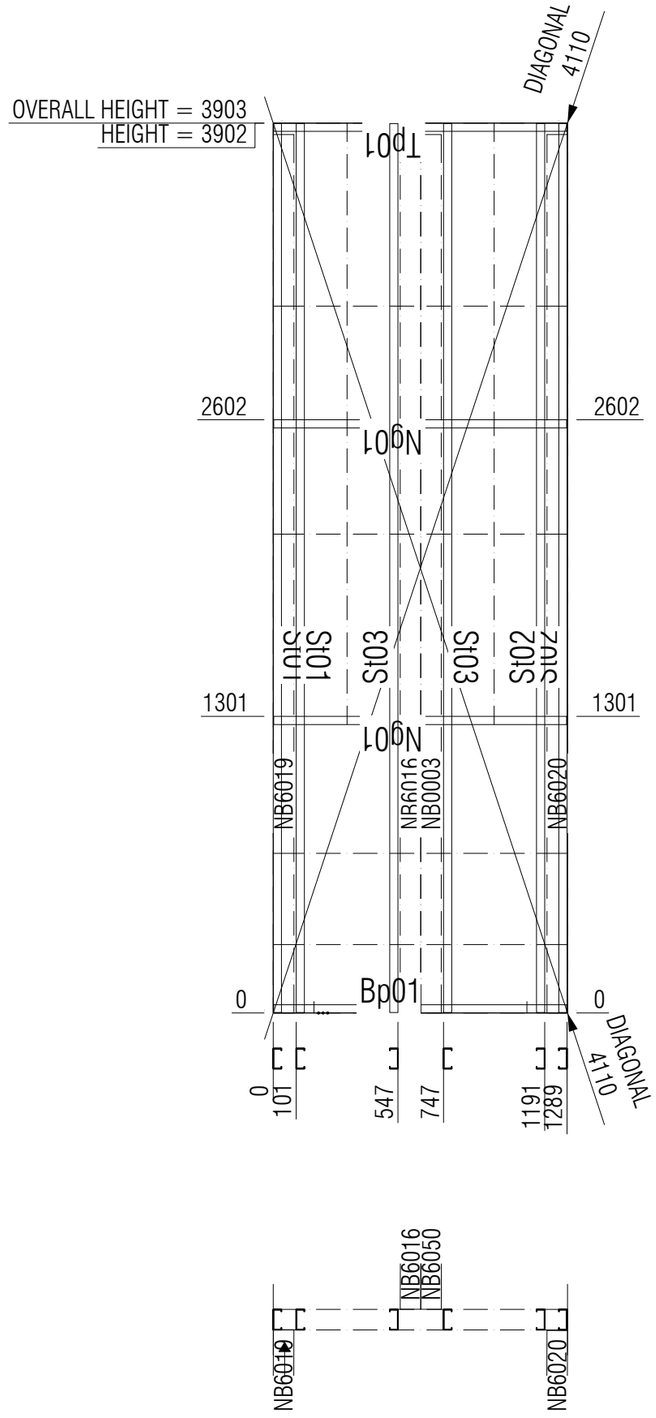

FRAME STICKS

NAME	LENGTH	WT	QTY	PROFILE
Tp01	1285	1.6	1	89S36-950-500
Bp01	1285	1.6	1	89S36-950-500
St01	3898	5.0	2	89S36-950-500
St02	3899	5.0	2	89S36-950-500
St03	3898	5.0	2	89S36-950-500
Ng01	1285	1.6	2	89S36-950-500
TOTAL	28530	36.5	10	

LB6036

AUSTRUSS
www.austruss.com.au (02) 4860 1400


DRAWN Mitchell.H
Ph:02 4860 1426

ISSUE	DATE	DESCRIPTION OF REVISION
0	05/03/26	IFA
A	03/05/26	IFC
B	06/05/26	IFC
C	08/05/26	IFC
D	11/05/26	IFC

DWG FILE: ####

Client/Company Name: Taylor
Project Name: Blayney
Building / Zone / Area: Zone 6
Job Number: 23314
Project Address: 3 Osman st, Blayney NSW 2799
Drawing Name: 90mm LB Wall production
Drawing Number: LGS-6-201
Revision: D
NOTE: USE PROVIDED DIMENSIONS ONLY. IF NOT PROVIDED, ASK.
Scale: NTS

STP

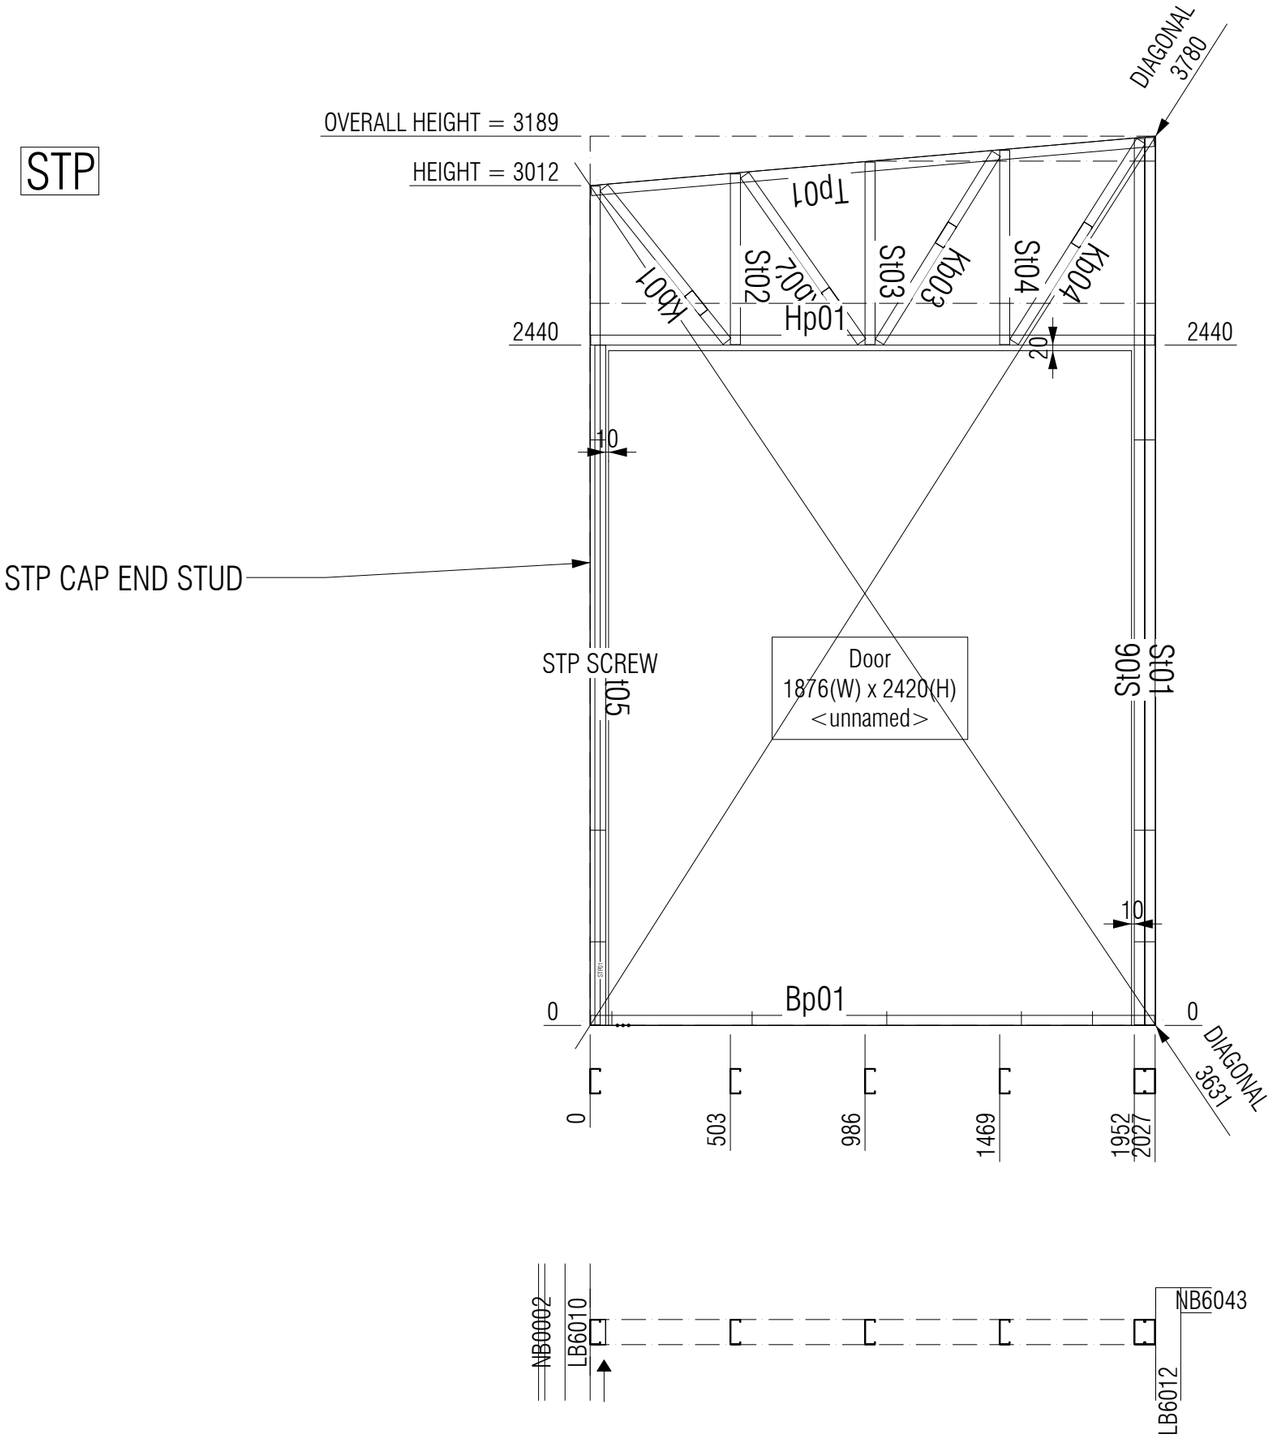

FRAME STICKS

NAME	LENGTH	WT	QTY	PROFILE
Tp01	2027	2.6	1	89S36-950-500
Bp01	2023	2.6	1	89S36-950-500
St01	3179	4.1	1	89S36-950-500
St02	612	0.8	1	89S36-950-500
St03	654	0.8	1	89S36-950-500
St04	697	0.9	1	89S36-950-500
St05	3008	3.9	1	89S36-950-500
St06	3182	4.1	1	89S36-950-500
Kb01	706	0.9	1	89S36-950-500
Kb02	730	0.9	1	89S36-950-500
Kb03	794	1.0	1	89S36-950-500
Kb04	852	1.1	1	89S36-950-500
Hp01	2023	2.6	1	89S36-950-500
TOTAL	20486	26.2	13	

STEEL SUPPORT MEMBERS

NAME	PROFILE	LENGTH	WT	QTY
STP01	92U39_095_550	2440	3.1	1
TOTAL			3.1	1

LB6011


AUSTRUSS
www.austruss.com.au (02) 4860 1400

DRAWN Mitchell.H
Ph:02 4860 1426

DWG FILE: ####

ISSUE	DATE	DESCRIPTION OF REVISION
0	05/03/26	IFA
A	03/05/26	IFC
B	06/05/26	IFC
C	08/05/26	IFC
D	11/05/26	IFC

Client/Company Name: Taylor
Project Name: Blayney
Project Address: 3 Osman st, Blayney NSW 2799
NOTE: USE PROVIDED DIMENSIONS ONLY. IF NOT PROVIDED, ASK.
Scale: NTS
Building / Zone / Area: Zone 6
Job Number: 23314
Drawing Name: 90mm LB Wall production
Drawing Number: LGS-6-201
Revision: D

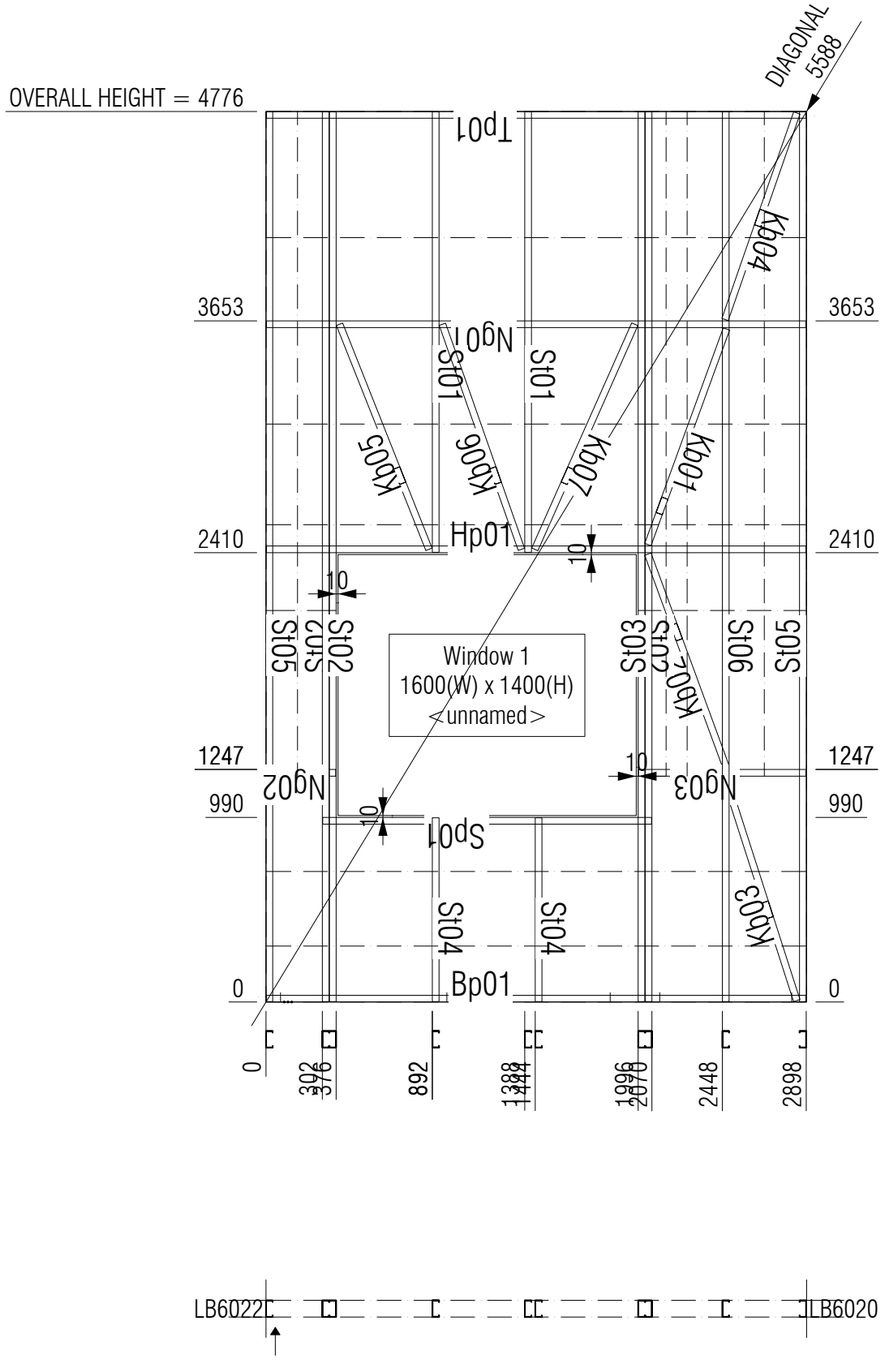

FRAME STICKS

NAME	LENGTH	WT	QTY	PROFILE
Tp01	2894	3.7	1	89S36-950-500
Bp01	2894	3.7	1	89S36-950-500
St01	2362	3.0	2	89S36-950-500
St02	4772	6.1	3	89S36-950-500
St03	4772	6.1	1	89S36-950-500
St04	986	1.3	2	89S36-950-500
St05	4772	6.1	2	89S36-950-500
St06	4772	6.1	1	89S36-950-500
Ng01	2894	3.7	1	89S36-950-500
Ng02	372	0.5	1	89S36-950-500
Ng03	898	1.1	1	89S36-950-500
Kb01	1231	1.6	1	89S36-950-500
Kb02	1222	1.6	1	89S36-950-500
Kb03	1257	1.6	1	89S36-950-500
Kb04	1173	1.5	1	89S36-950-500
Kb05	1299	1.7	1	89S36-950-500
Kb06	1280	1.6	1	89S36-950-500
Kb07	1321	1.7	1	89S36-950-500
Hp01	2894	3.7	1	89S36-950-500
Sp01	1764	2.3	1	89S36-950-500
TOTAL	63498	81.3	25	


LB6021

AUSTRUSS
www.austruss.com.au (02) 4860 1400
DWG FILE: ####

DRAWN Mitchell.H
Ph:02 4860 1426

ISSUE	DATE	DESCRIPTION OF REVISION
0	05/03/26	IFA
A	03/05/26	IFC
B	06/05/26	IFC
C	08/05/26	IFC
D	11/05/26	IFC

Client/Company Name: Taylor
Project Name: Blayney
Building / Zone / Area: Zone 6
Job Number: 23314
Project Address: 3 Osman st, Blayney NSW 2799
Drawing Name: 90mm LB Wall production
Drawing Number: LGS-6-201
Revision: D
NOTE: USE PROVIDED DIMENSIONS ONLY. IF NOT PROVIDED, ASK.
Scale: NTS

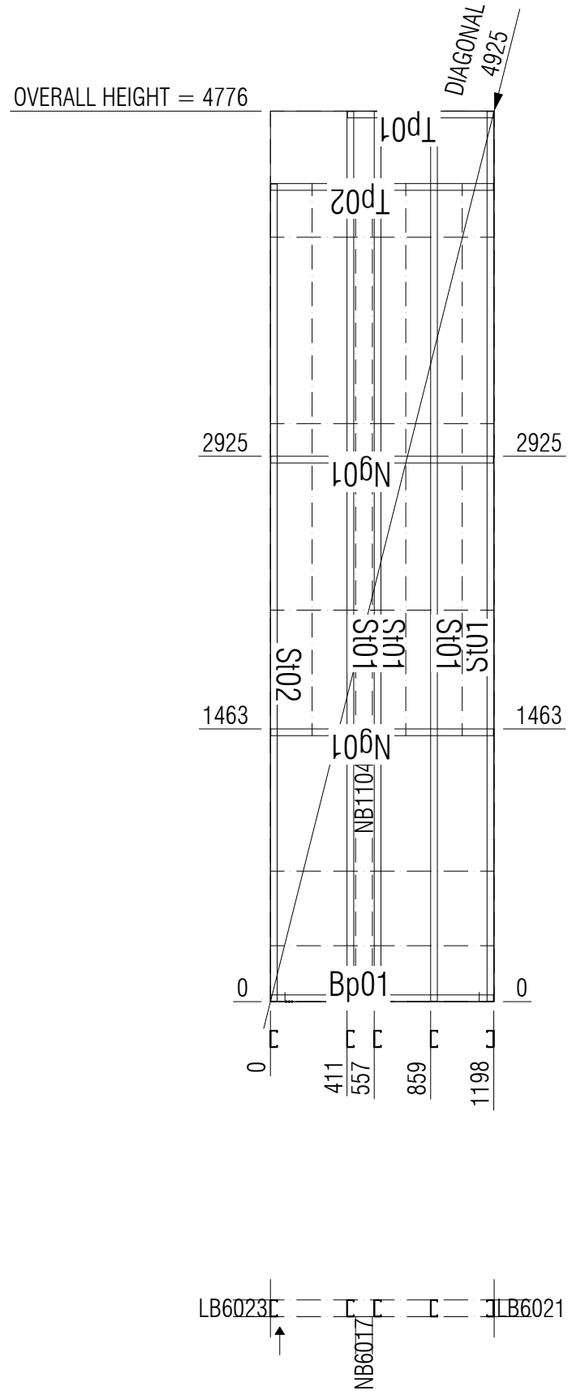

FRAME STICKS

NAME	LENGTH	WT	QTY	PROFILE
Tp01	783	1.0	1	89S36-950-500
Tp02	1194	1.5	1	89S36-950-500
Bp01	1194	1.5	1	89S36-950-500
St01	4772	6.1	4	89S36-950-500
St02	4384	5.6	1	89S36-950-500
Ng01	1194	1.5	2	89S36-950-500
TOTAL	29033	37.2	10	

LB6022


AUSTRUSS
www.austruss.com.au (02) 4860 1400

DWG FILE: ####

DRAWN
Mitchell.H
Ph:02 4860 1426

ISSUE	DATE	DESCRIPTION OF REVISION
0	05/03/26	IFA
A	03/05/26	IFC
B	06/05/26	IFC
C	08/05/26	IFC
D	11/05/26	IFC

Client/Company Name: Taylor
Project Name: Blayney
Building / Zone / Area: Zone 6
Job Number: 23314
Project Address: 3 Osman st, Blayney NSW 2799
NOTE: USE PROVIDED DIMENSIONS ONLY. IF NOT PROVIDED, ASK.
Scale: NTS
Drawing Name: 90mm LB Wall production
Drawing Number: LGS-6-201
Revision: D

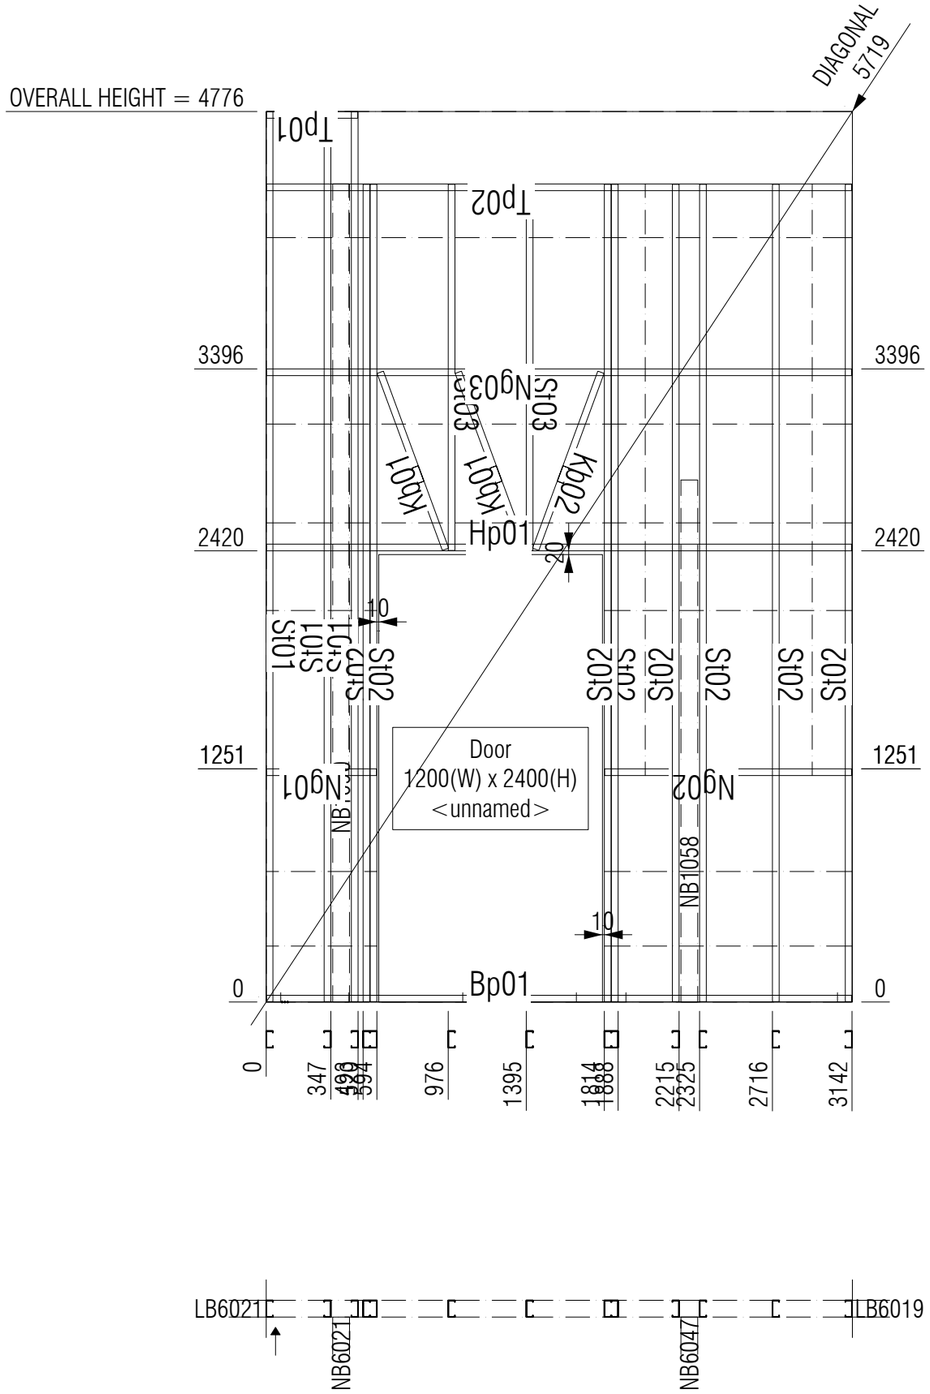

FRAME STICKS

NAME	LENGTH	WT	QTY	PROFILE
Tp01	489	0.6	1	89S36-950-500
Tp02	3138	4.0	1	89S36-950-500
Bp01	3138	4.0	1	89S36-950-500
St01	4772	6.1	3	89S36-950-500
St02	4384	5.6	8	89S36-950-500
St03	1964	2.5	2	89S36-950-500
Ng01	590	0.8	1	89S36-950-500
Ng02	1325	1.7	1	89S36-950-500
Ng03	3138	4.0	1	89S36-950-500
Kb01	1012	1.3	2	89S36-950-500
Kb02	1012	1.3	1	89S36-950-500
Hp01	3138	4.0	1	89S36-950-500
TOTAL	71310	91.3	23	

LB6020


AUSTRUSS
www.austruss.com.au (02) 4860 1400

DWG FILE: ####

DRAWN
Mitchell.H
Ph:02 4860 1426

ISSUE	DATE	DESCRIPTION OF REVISION
0	05/03/26	IFA
A	03/05/26	IFC
B	06/05/26	IFC
C	08/05/26	IFC
D	11/05/26	IFC

Client/Company Name: Taylor
Project Name: Blayney
Building / Zone / Area: Zone 6
Job Number: 23314
Project Address: 3 Osman st, Blayney NSW 2799
Drawing Name: 90mm LB Wall production
Drawing Number: LGS-6-201
Revision: D
NOTE: USE PROVIDED DIMENSIONS ONLY. IF NOT PROVIDED, ASK.
Scale: NTS

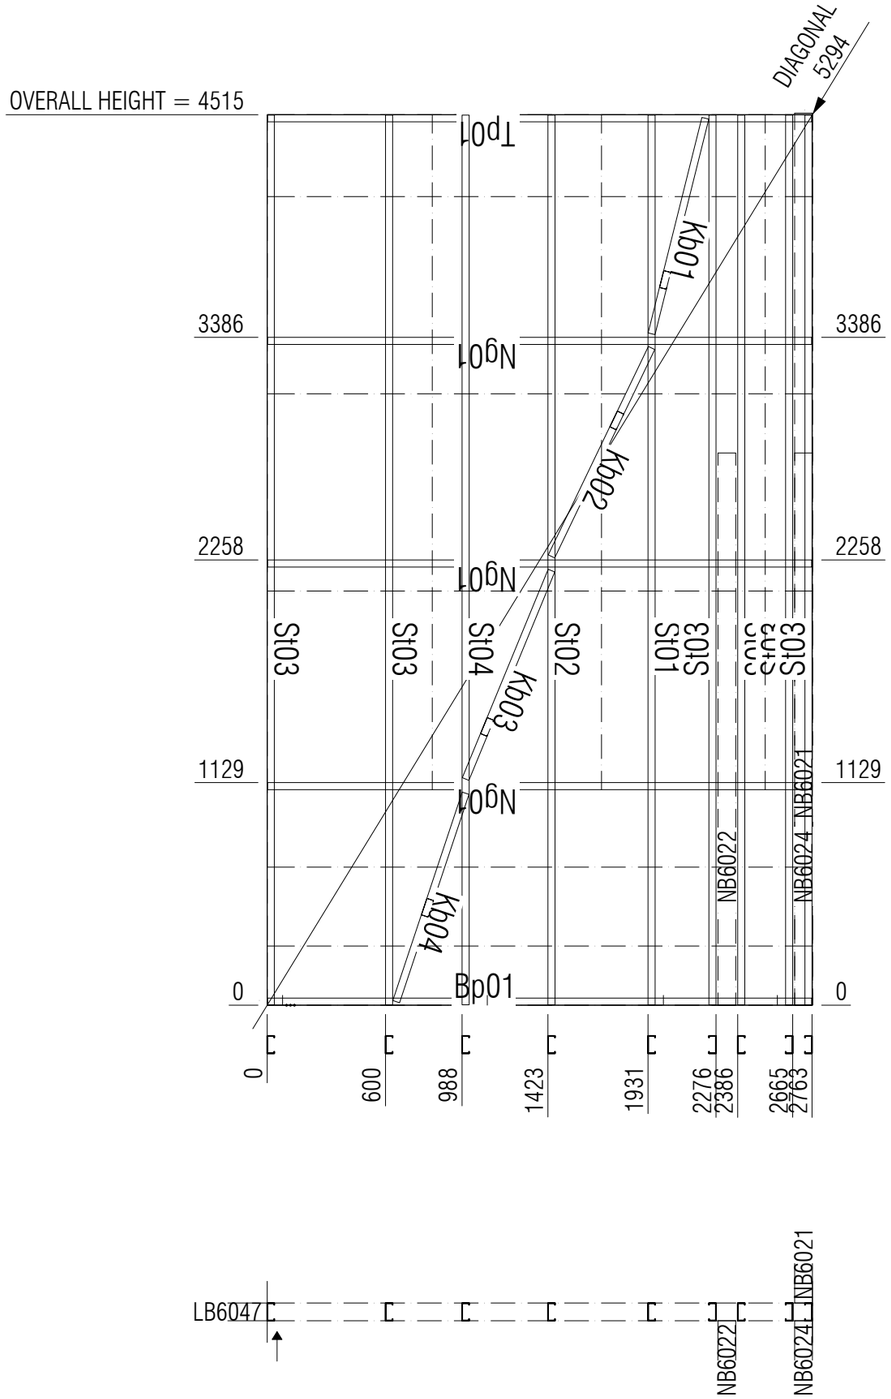

FRAME STICKS

NAME	LENGTH	WT	QTY	PROFILE
Tp01	2759	3.5	1	89S36-950-500
Bp01	2759	3.5	1	89S36-950-500
St01	4511	5.8	1	89S36-950-500
St02	4511	5.8	1	89S36-950-500
St03	4511	5.8	6	89S36-950-500
St04	4511	5.8	1	89S36-950-500
Ng01	2759	3.5	3	89S36-950-500
Kb01	1126	1.4	1	89S36-950-500
Kb02	1172	1.5	1	89S36-950-500
Kb03	1143	1.5	1	89S36-950-500
Kb04	1114	1.4	1	89S36-950-500
TOTAL	58949	75.5	18	

LB6046


AUSTRUSS
www.austruss.com.au (02) 4860 1400

DWG FILE: ####

DRAWN Mitchell.H Ph:02 4860 1426

ISSUE	DATE	DESCRIPTION OF REVISION
0	05/03/26	IFA
A	03/05/26	IFC
B	06/05/26	IFC
C	08/05/26	IFC
D	11/05/26	IFC

Client/Company Name: Taylor
Project Name: Blayney
Building / Zone / Area: Zone 6
Job Number: 23314
Project Address: 3 Osman st, Blayney NSW 2799
Drawing Name: 90mm LB Wall production
Drawing Number: LGS-6-201
Revision: D
NOTE: USE PROVIDED DIMENSIONS ONLY. IF NOT PROVIDED, ASK.
Scale: NTS

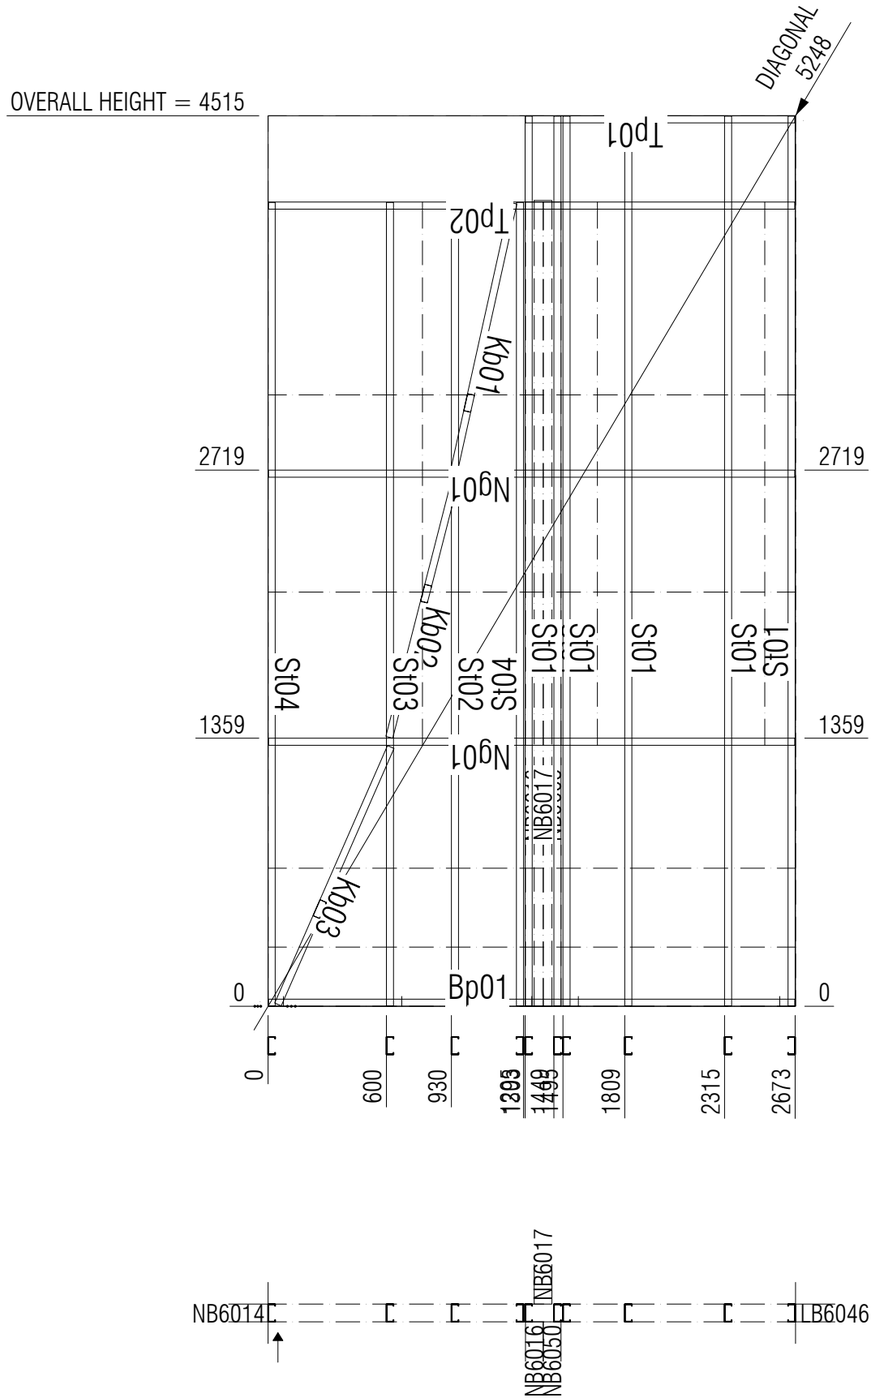

FRAME STICKS

NAME	LENGTH	WT	QTY	PROFILE
Tp01	1365	1.7	1	89S36-950-500
Tp02	2669	3.4	1	89S36-950-500
Bp01	2669	3.4	1	89S36-950-500
St01	4511	5.8	6	89S36-950-500
St02	4074	5.2	1	89S36-950-500
St03	4074	5.2	1	89S36-950-500
St04	4074	5.2	2	89S36-950-500
Ng01	2669	3.4	2	89S36-950-500
Kb01	1383	1.8	1	89S36-950-500
Kb02	1356	1.7	1	89S36-950-500
Kb03	1425	1.8	1	89S36-950-500
TOTAL	59566	76.2	18	


LB6047

AUSTRUSS
www.austruss.com.au (02) 4860 1400
DWG FILE: ####

DRAWN
Mitchell.H
Ph:02 4860 1426

ISSUE	DATE	DESCRIPTION OF REVISION
0	05/03/26	IFA
A	03/05/26	IFC
B	06/05/26	IFC
C	08/05/26	IFC
D	11/05/26	IFC

Client/Company Name: Taylor
Project Name: Blayney
Project Address: 3 Osman st, Blayney NSW 2799
NOTE: USE PROVIDED DIMENSIONS ONLY. IF NOT PROVIDED, ASK.
Scale: NTS
Building / Zone / Area: Zone 6
Drawing Name: 90mm LB Wall production
Job Number: 23314
Drawing Number: LGS-6-201
Revision: D

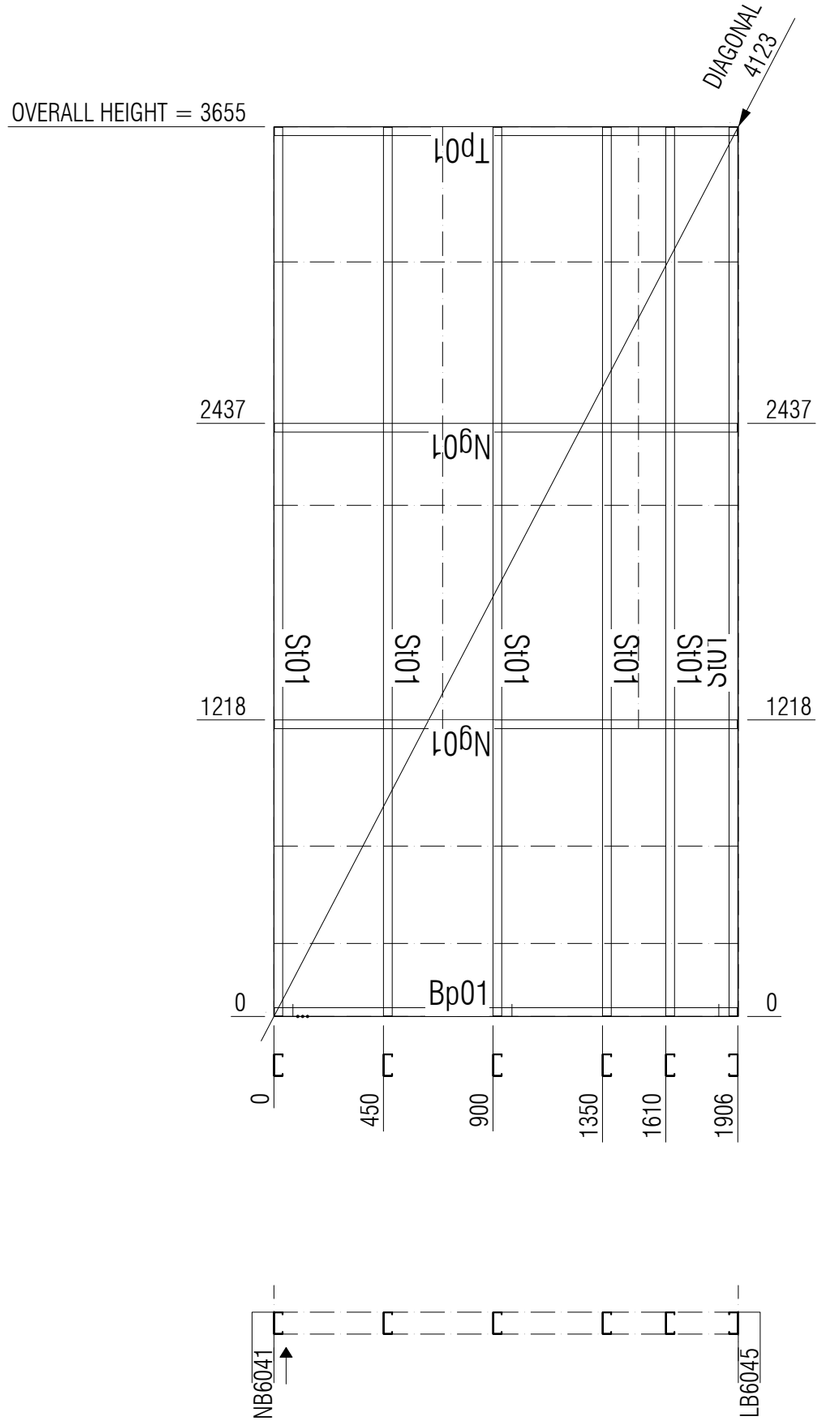

FRAME STICKS

NAME	LENGTH	WT	QTY	PROFILE
Tp01	1902	2.4	1	89S36-950-500
Bp01	1902	2.4	1	89S36-950-500
St01	3651	4.7	6	89S36-950-500
Ng01	1902	2.4	2	89S36-950-500
TOTAL	29516	37.8	10	

LB6037


AUSTRUSS
www.austruss.com.au (02) 4860 1400

DWG FILE: ####

DRAWN
Mitchell.H
Ph:02 4860 1426

ISSUE	DATE	DESCRIPTION OF REVISION
0	05/03/26	IFA
A	03/05/26	IFC
B	06/05/26	IFC
C	08/05/26	IFC
D	11/05/26	IFC

Client/Company Name: Taylor
Project Name: Blayney
Building / Zone / Area: Zone 6
Job Number: 23314
Project Address: 3 Osman st, Blayney NSW 2799
Drawing Name: 90mm LB Wall production
Drawing Number: LGS-6-201
Revision: D
NOTE: USE PROVIDED DIMENSIONS ONLY. IF NOT PROVIDED, ASK.
Scale: NTS

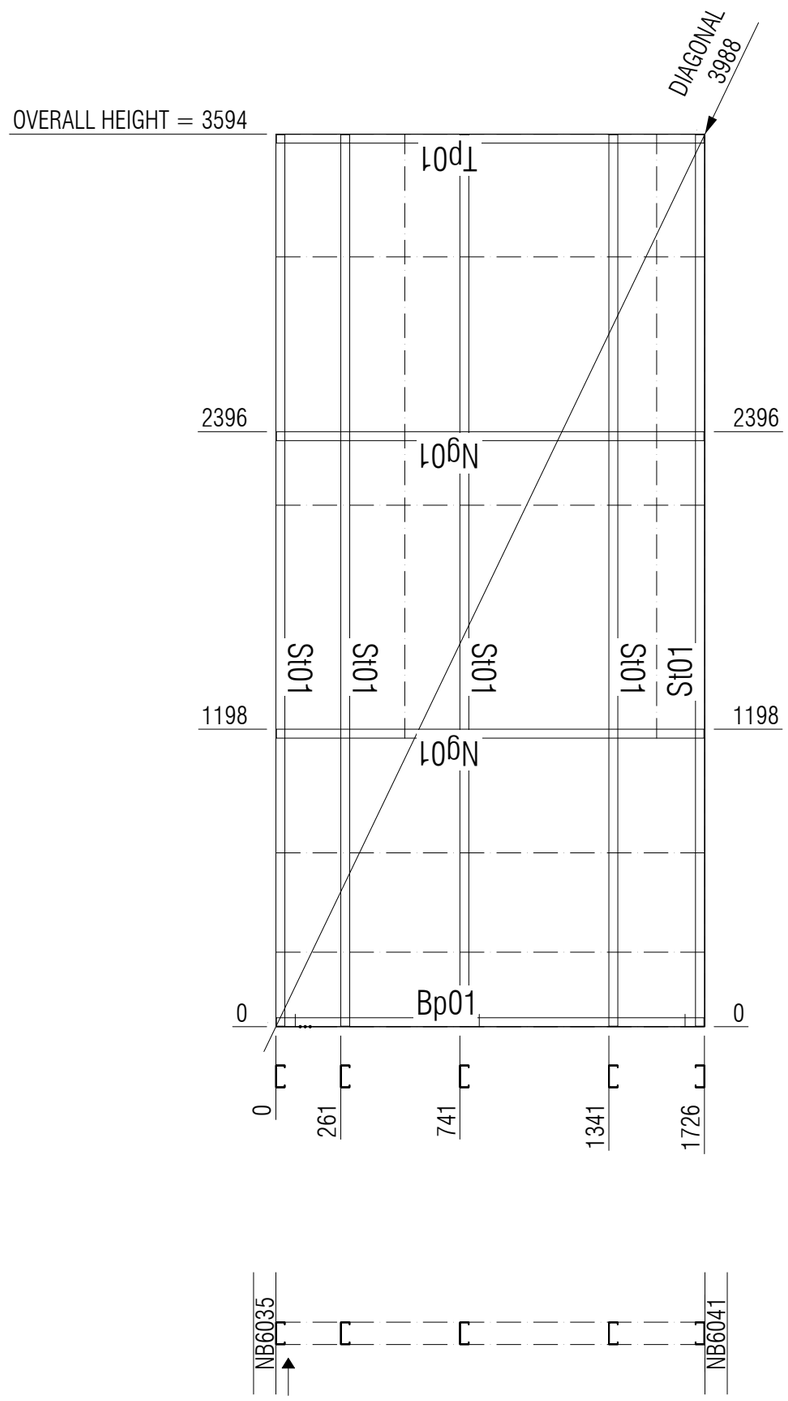

FRAME STICKS

NAME	LENGTH	WT	QTY	PROFILE
Tp01	1722	2.2	1	89S36-950-500
Bp01	1722	2.2	1	89S36-950-500
St01	3590	4.6	5	89S36-950-500
Ng01	1722	2.2	2	89S36-950-500
TOTAL	24838	31.8	9	

LB6035

AUSTRUSS
www.austruss.com.au (02) 4860 1400

DRAWN Mitchell.H Ph:02 4860 1426

DWG FILE: ####

ISSUE	DATE	DESCRIPTION OF REVISION
0	05/03/26	IFA
A	03/05/26	IFC
B	06/05/26	IFC
C	08/05/26	IFC
D	11/05/26	IFC

Client/Company Name: Taylor

Project Name: Blayney

Building / Zone / Area: Zone 6

Job Number: 23314

Project Address: 3 Osman st, Blayney NSW 2799

NOTE: USE PROVIDED DIMENSIONS ONLY. IF NOT PROVIDED, ASK.


Scale: NTS

Drawing Name: 90mm LB Wall production

Drawing Number: LGS-6-201

Revision: D

WELD ALL

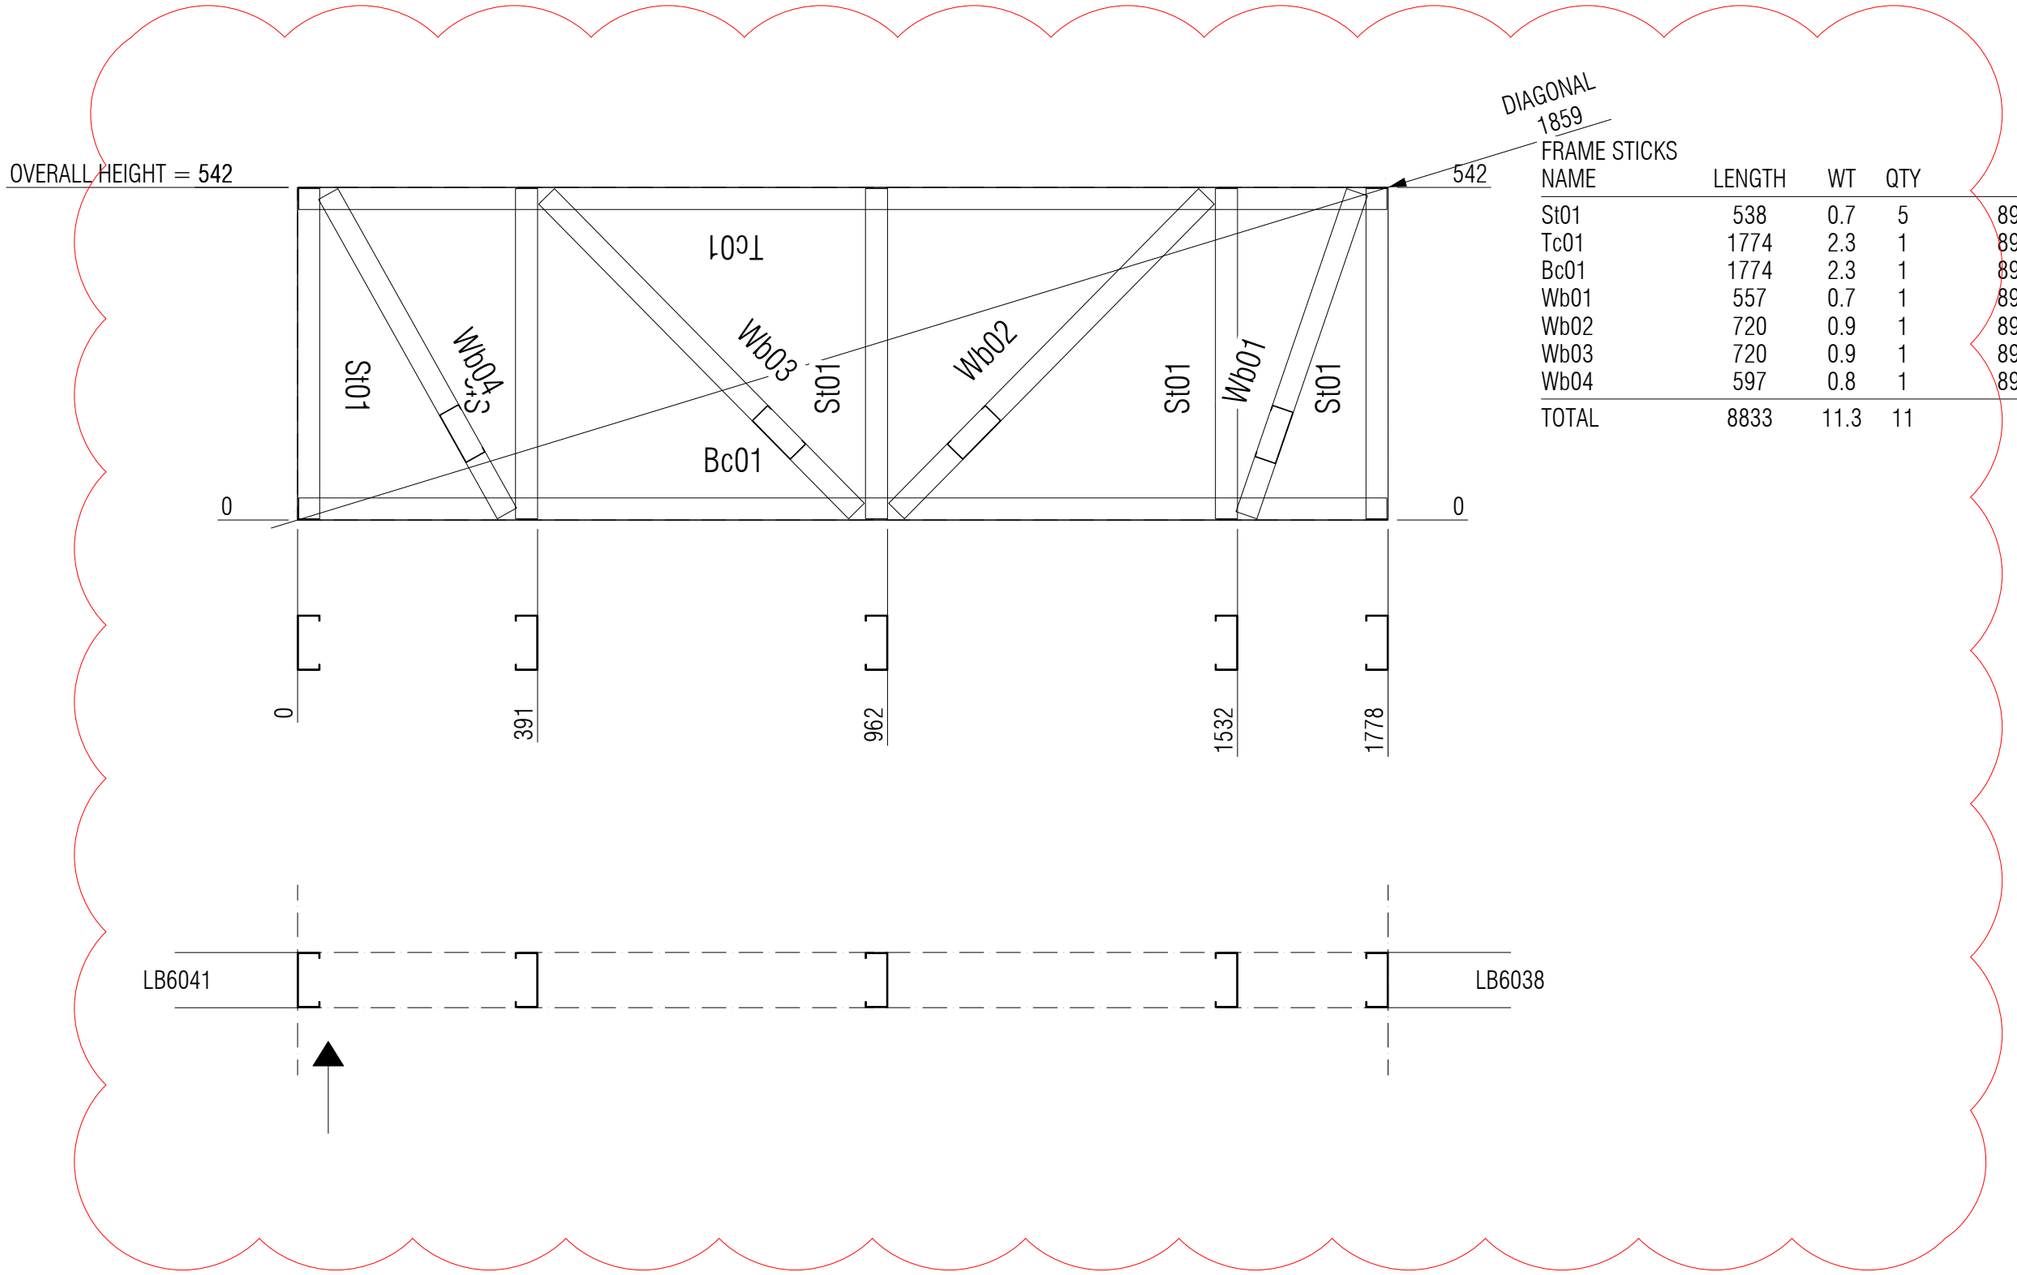

FRAME STICKS

NAME	LENGTH	WT	QTY	PROFILE
St01	538	0.7	5	89S36-950-500
Tc01	1774	2.3	1	89S36-950-500
Bc01	1774	2.3	1	89S36-950-500
Wb01	557	0.7	1	89S36-950-500
Wb02	720	0.9	1	89S36-950-500
Wb03	720	0.9	1	89S36-950-500
Wb04	597	0.8	1	89S36-950-500
TOTAL	8833	11.3	11	

GI6002


AUSTRUSS
www.austruss.com.au (02) 4860 1400
DWG FILE: ####

DRAWN Mitchell.H
Ph:02 4860 1426


ISSUE	DATE	DESCRIPTION OF REVISION
0	05/03/26	IFA
A	03/05/26	IFC
B	06/05/26	IFC
C	08/05/26	IFC
D	11/05/26	IFC

Client/Company Name: Taylor
Project Name: Blayney
Building / Zone / Area: Zone 6
Job Number: 23314
Project Address: 3 Osman st, Blayney NSW 2799
NOTE: USE PROVIDED DIMENSIONS ONLY. IF NOT PROVIDED, ASK.
Scale: NTS
Drawing Name: 90mm LB Wall production
Drawing Number: LGS-6-201
Revision: D

WELD ALL

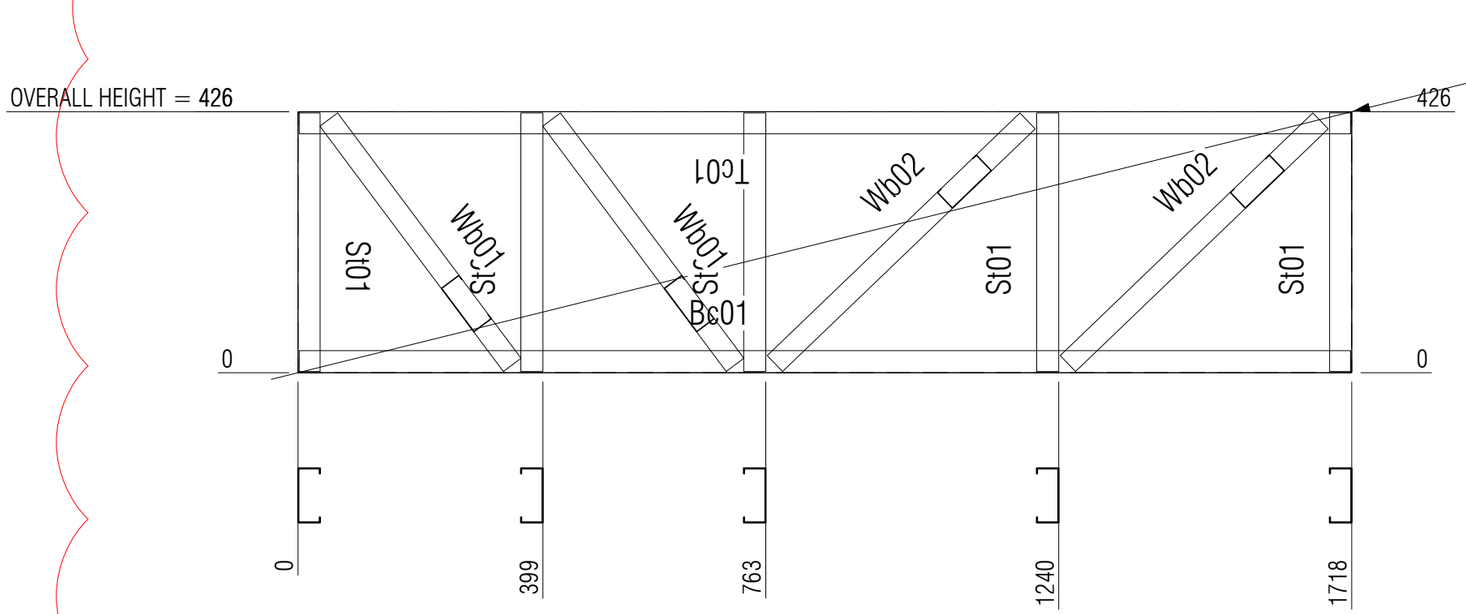

NAME	LENGTH	WT	QTY	PROFILE
St01	422	0.5	5	89S36-950-500
Tc01	1714	2.2	1	89S36-950-500
Bc01	1714	2.2	1	89S36-950-500
Wb01	499	0.6	2	89S36-950-500
Wb02	571	0.7	2	89S36-950-500
TOTAL	7677	9.8	11	

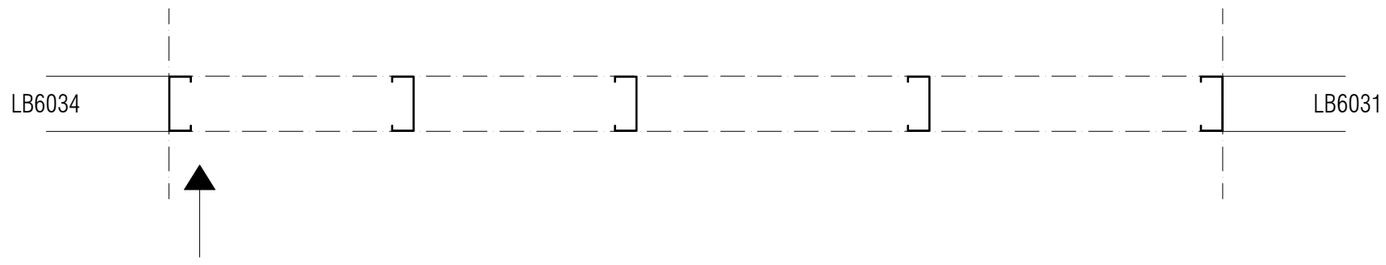

GI6001

AUSTRUSS
www.austruss.com.au (02) 4860 1400


DWG FILE: ####

DRAWN
Mitchell.H
Ph:02 4860 1426

ISSUE	DATE	DESCRIPTION OF REVISION
0	05/03/26	IFA
A	03/05/26	IFC
B	06/05/26	IFC
C	08/05/26	IFC
D	11/05/26	IFC

Client/Company Name: Taylor
Project Name: Blayney
Building / Zone / Area: Zone 6
Job Number: 23314
Project Address: 3 Osman st, Blayney NSW 2799
Drawing Name: 90mm LB Wall production
Drawing Number: LGS-6-201
Revision: D
NOTE: USE PROVIDED DIMENSIONS ONLY. IF NOT PROVIDED, ASK.
Scale: NTS

WELD ALL

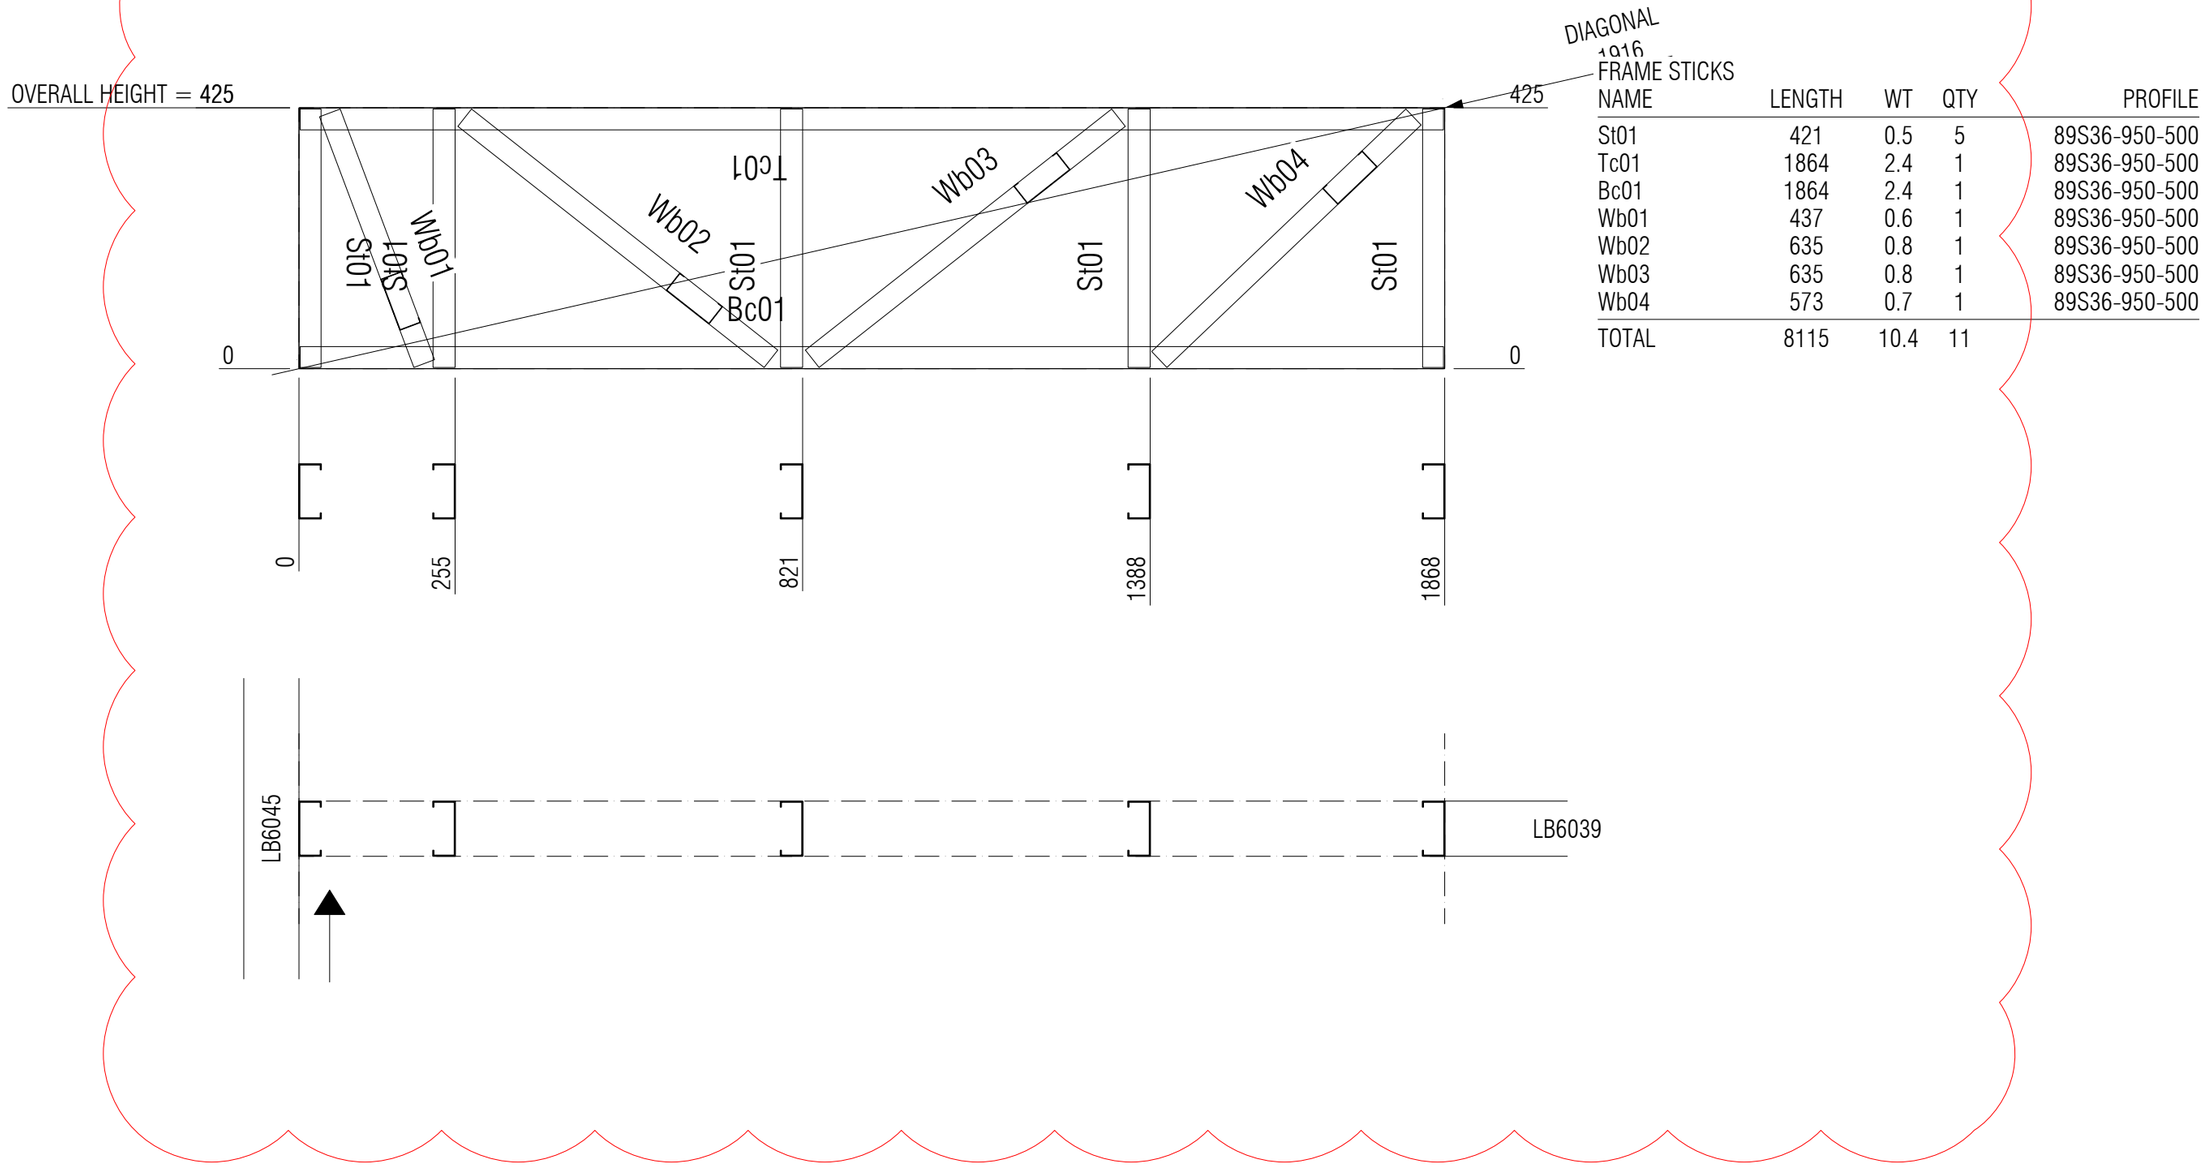

NAME	LENGTH	WT	QTY	PROFILE
St01	421	0.5	5	89S36-950-500
Tc01	1864	2.4	1	89S36-950-500
Bc01	1864	2.4	1	89S36-950-500
Wb01	437	0.6	1	89S36-950-500
Wb02	635	0.8	1	89S36-950-500
Wb03	635	0.8	1	89S36-950-500
Wb04	573	0.7	1	89S36-950-500
TOTAL	8115	10.4	11	

GI6003

AUSTRUSS
www.austruss.com.au (02) 4860 1400
DWG FILE: ####

DRAWN
Mitchell.H
Ph:02 4860 1426

ISSUE	DATE	DESCRIPTION OF REVISION
0	05/03/26	IFA
A	03/05/26	IFC
B	06/05/26	IFC
C	08/05/26	IFC
D	11/05/26	IFC

Client/Company Name: Taylor
Project Name: Blayney
Project Address: 3 Osman st, Blayney NSW 2799
NOTE: USE PROVIDED DIMENSIONS ONLY. IF NOT PROVIDED, ASK.
Scale: NTS
Building / Zone / Area: Zone 6
Job Number: 23314
Drawing Name: 90mm LB Wall production
Drawing Number: LGS-6-201
Revision: D